



PORTFOLIO

Renya Niinuma



Contact

+81 60351764
niinuma.r52c8@m.isct.ac.jp
644-4-603, Naganuma-cho, Sakae-ku, Yokohama-shi, Kanagawa, JAPAN

Languages

- Japanese (native)
- English (intermediate, IELTS band 6.0)
- German (beginner)
- French (beginner)

Biography

04.2025 -	Institute of Science Tokyo (former name : Tokyo Institute of Technology) Master degree in architecture, Shin-ichi Okuyama Lab.
04.2020 - 03.2024	Meiji University Bachelor degree in Architecture
07.12.2001	Born in Kanagawa, Japan

Skills

- Model making
- Rhinoceros
- AutoCAD
- Vector Works
- Twinmotion
- Photoshop
- Illustrator
- Indesign
- Lightroom
- Blender
- Word
- Excel
- Powerpoint

Experience

11.2025	Joint Design Workshop with Tongji University, Shanghai, China
05.2025 -	Tokyo Research Facility Implementation Design Project Shin-ichi Okuyama Lab.
07.2022 -	Miki Motohashi Architects And Associates (MMAAA), Tokyo, Japan Internship(3 months), Part-time job
2022, 2023	Koyart(=koya+art) project Implementation design of unstaffed vegetable stall(koya), Representative of the design

Hobbies

- Playing the drums
- Model making
- Fashion
- Drawing pictures
- Traveling
- Going for a walk



掲載作品

Featured Works

奥山研究室 研究施設実施設計プロジェクト

Research Facility Detailed Design Project in Okuyama Lab.

p.4~12

格子のすきま

Lattice Dwelling

p.13~21

境界の作法

Baunday Manners

p.22~30

パブリックドロ잉 東京計画 1960 丹下健三

Public Drawing A Plan for Tokyo 1960 by Kenzo Tange

p.31~32

過去案の模型

Models of previous ideas

p.33~34

奥山研究室
研究施設実施設計プロジェクト

Research Facility Detailed Design Project
in Okuyama Lab.



作品概要

奥山研究室で行っている研究施設の実施設計プロジェクト。奥山教授がデザイナー・アーキテクトを務め、複数の設計事務所と協働して 2030 年の竣工を目指して現在進行中のプロジェクトである。

プロジェクト参加前に基本設計が完了しており、自分の担当範囲は基本設計の修正と、具体的な実施設計である。図面・模型・パースを用いて、毎月教授とのエスキスを行っている。

来年の 3 月までには設計資料をまとめ、実施設計が終了する予定である。

Project Overview

This is a working design project for a research facility undertaken within the Okuyama Laboratory. Professor Okuyama serves as design architect, and the project is currently in progress in collaboration with multiple architectural practices, with a target completion date of 2030.

The schematic design had already been finalised prior to my involvement; my responsibilities encompass revisions to the schematic design and the development of the working drawings. Monthly discussions are held with the professor using drawings, physical models, and rendered perspectives.

The working design documentation is scheduled to be completed and compiled by March of next year.



貫通通路／エントランス

自治体により、建物の一部が公共利益に供する機能を持つよう指定されている。

この建築では、1,2F を最寄駅から続く歩行者デッキと接続した公共的な通路とすることで、広く一般に利用できるようにすることとした。これを貫通通路と呼び、施設利用者もこの空間からエントランスに入ることになる。


公共的な性格と当施設の顔としての性格を持つ空間として、多くの検討が重ねられた。

Public Pathway / Entrance

Municipal regulations require that a portion of the building serve a function contributing to the public interest.


In this project, the first and second floors are connected to a pedestrian deck extending from the nearest station, forming a publicly accessible thoroughfare open to all. This is referred to as the pedestrian passage, and visitors to the facility also enter the building through this space.

As an environment that carries both a public character and the role of representing the face of the facility, the design of this space underwent extensive study and iteration.

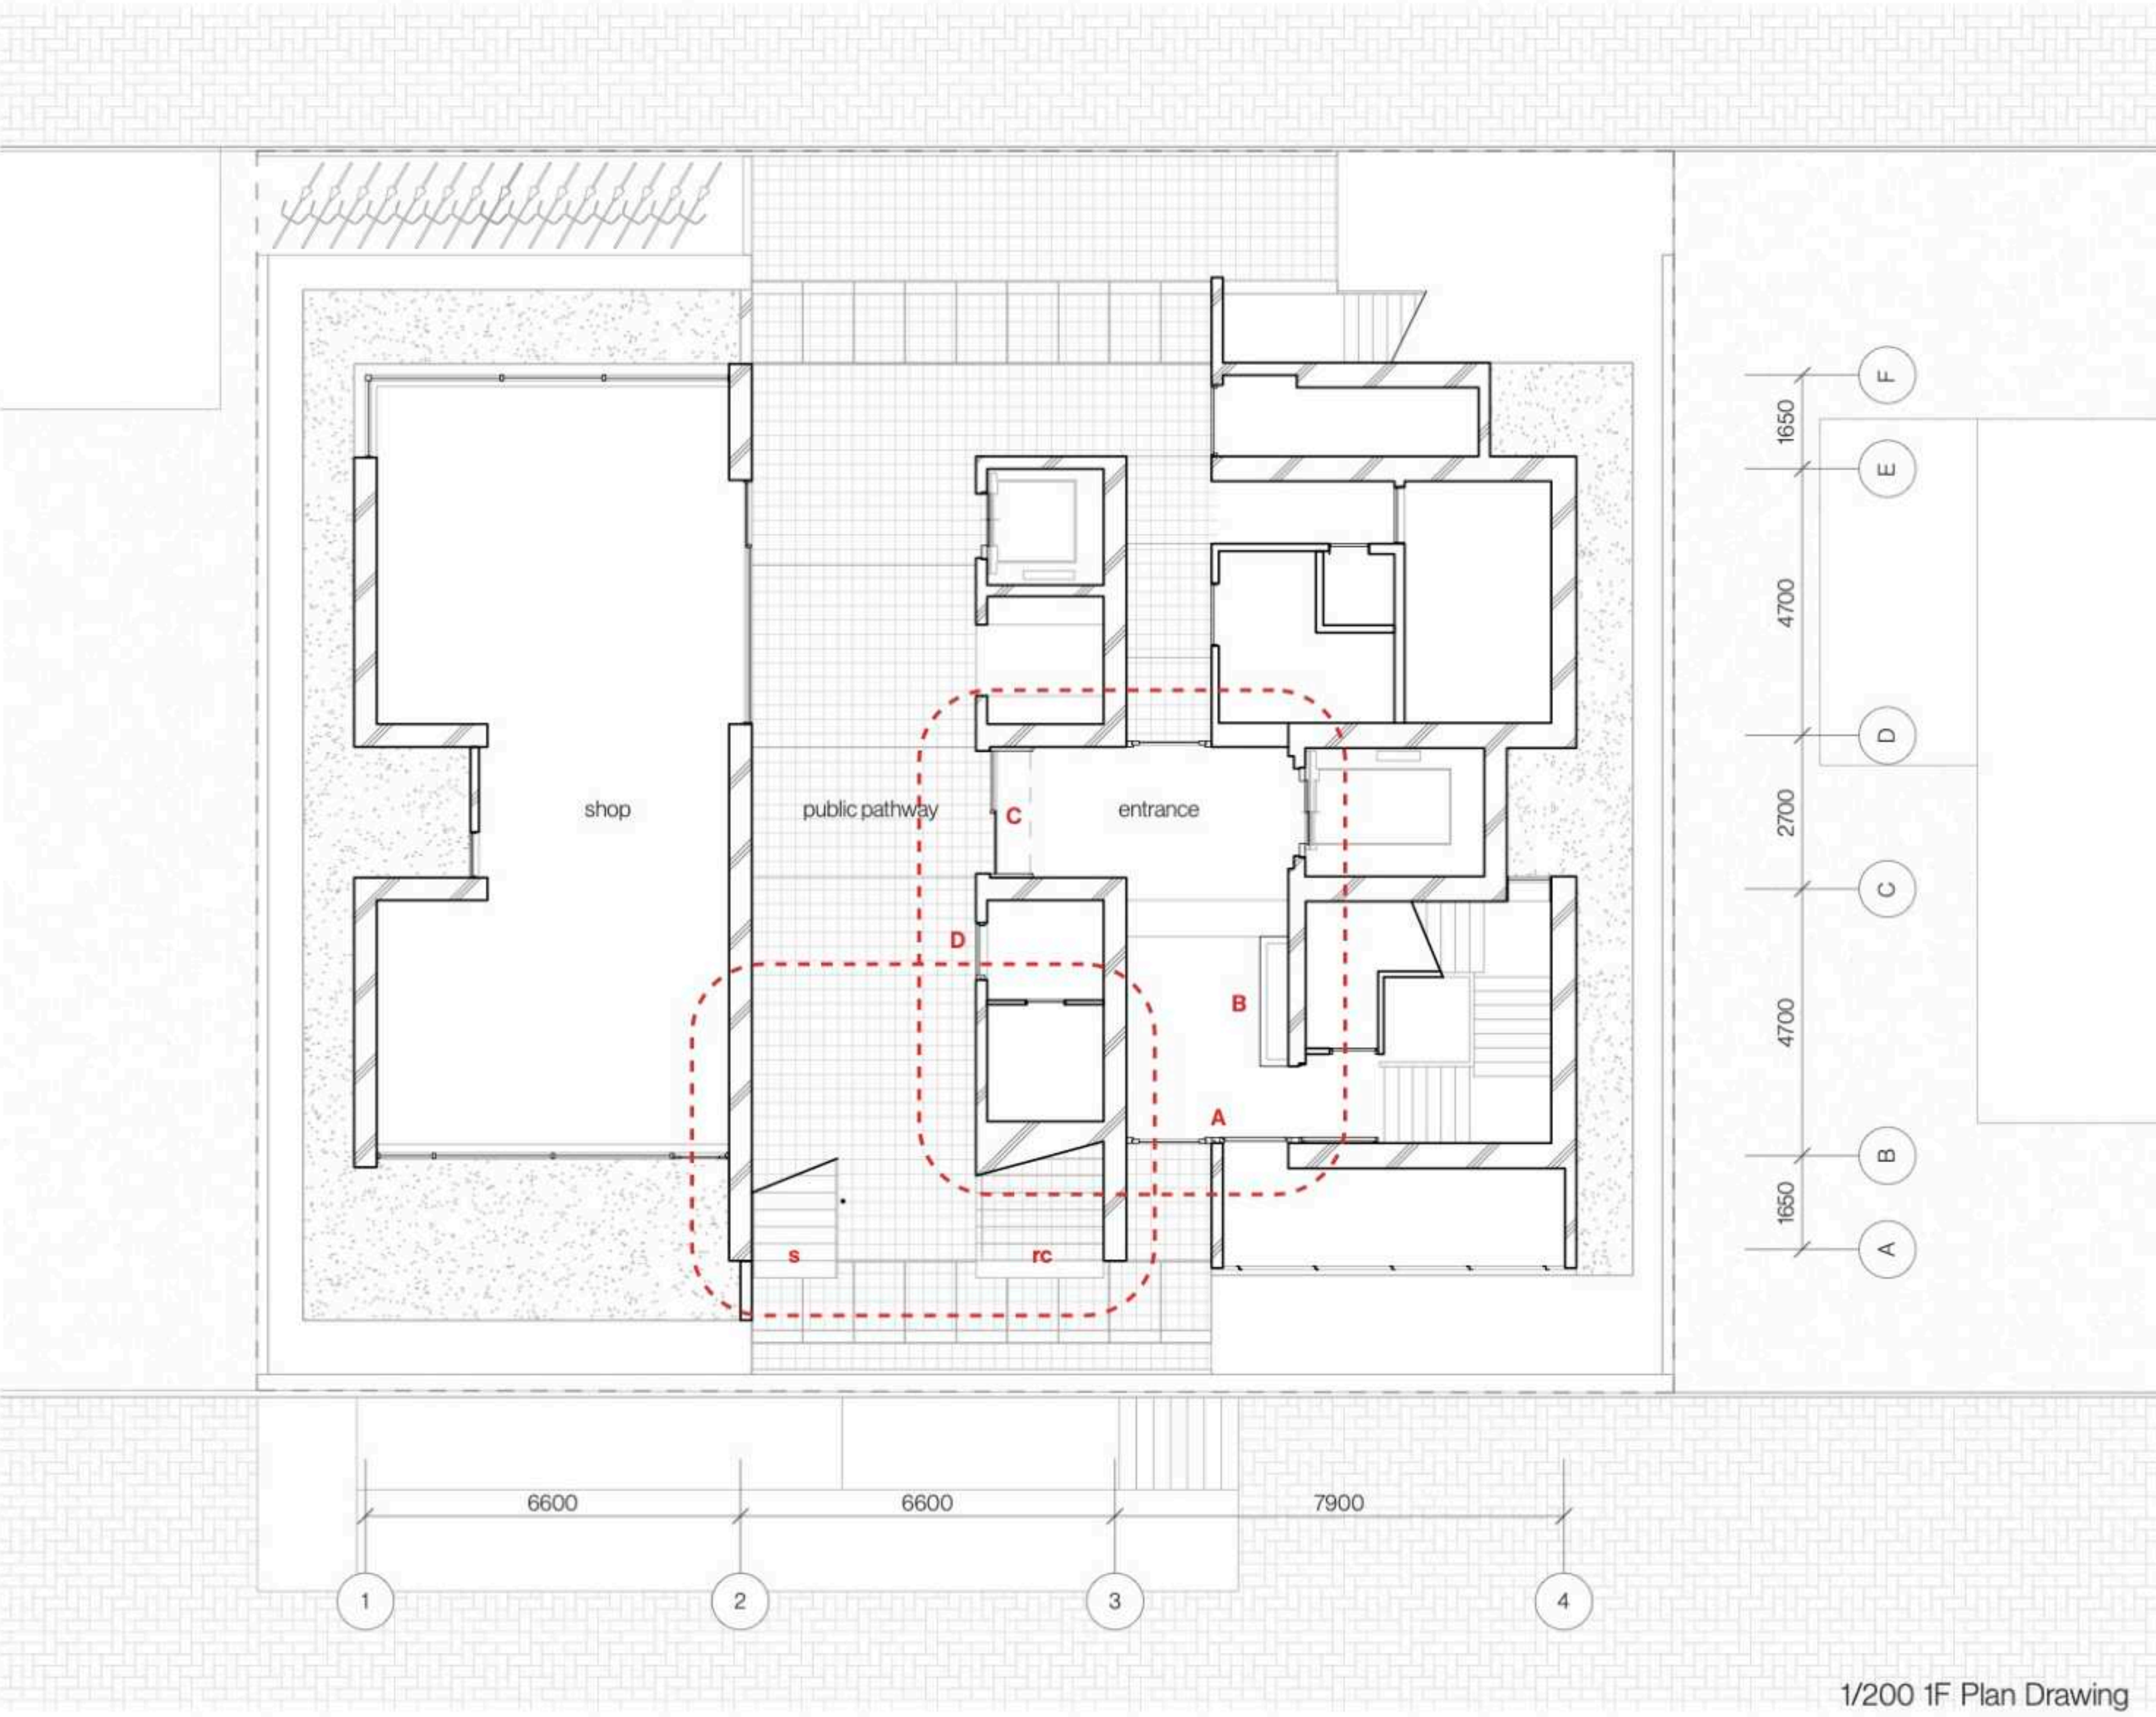

A, B. Entrance doors and inspection door in the 1st floor entrance
C, D. Automatic door and inspection door at the 1st floor entrance

- 1. 10×100mm @100mm aluminum louver
- 2. 40mm glassfiber reinforced cement insulation board
- 3. luminous ceiling
- 4. 4mm fire resistant aluminum composite panel
- 5. 100×100×10mm tile
- 6. tile finish expansion joint

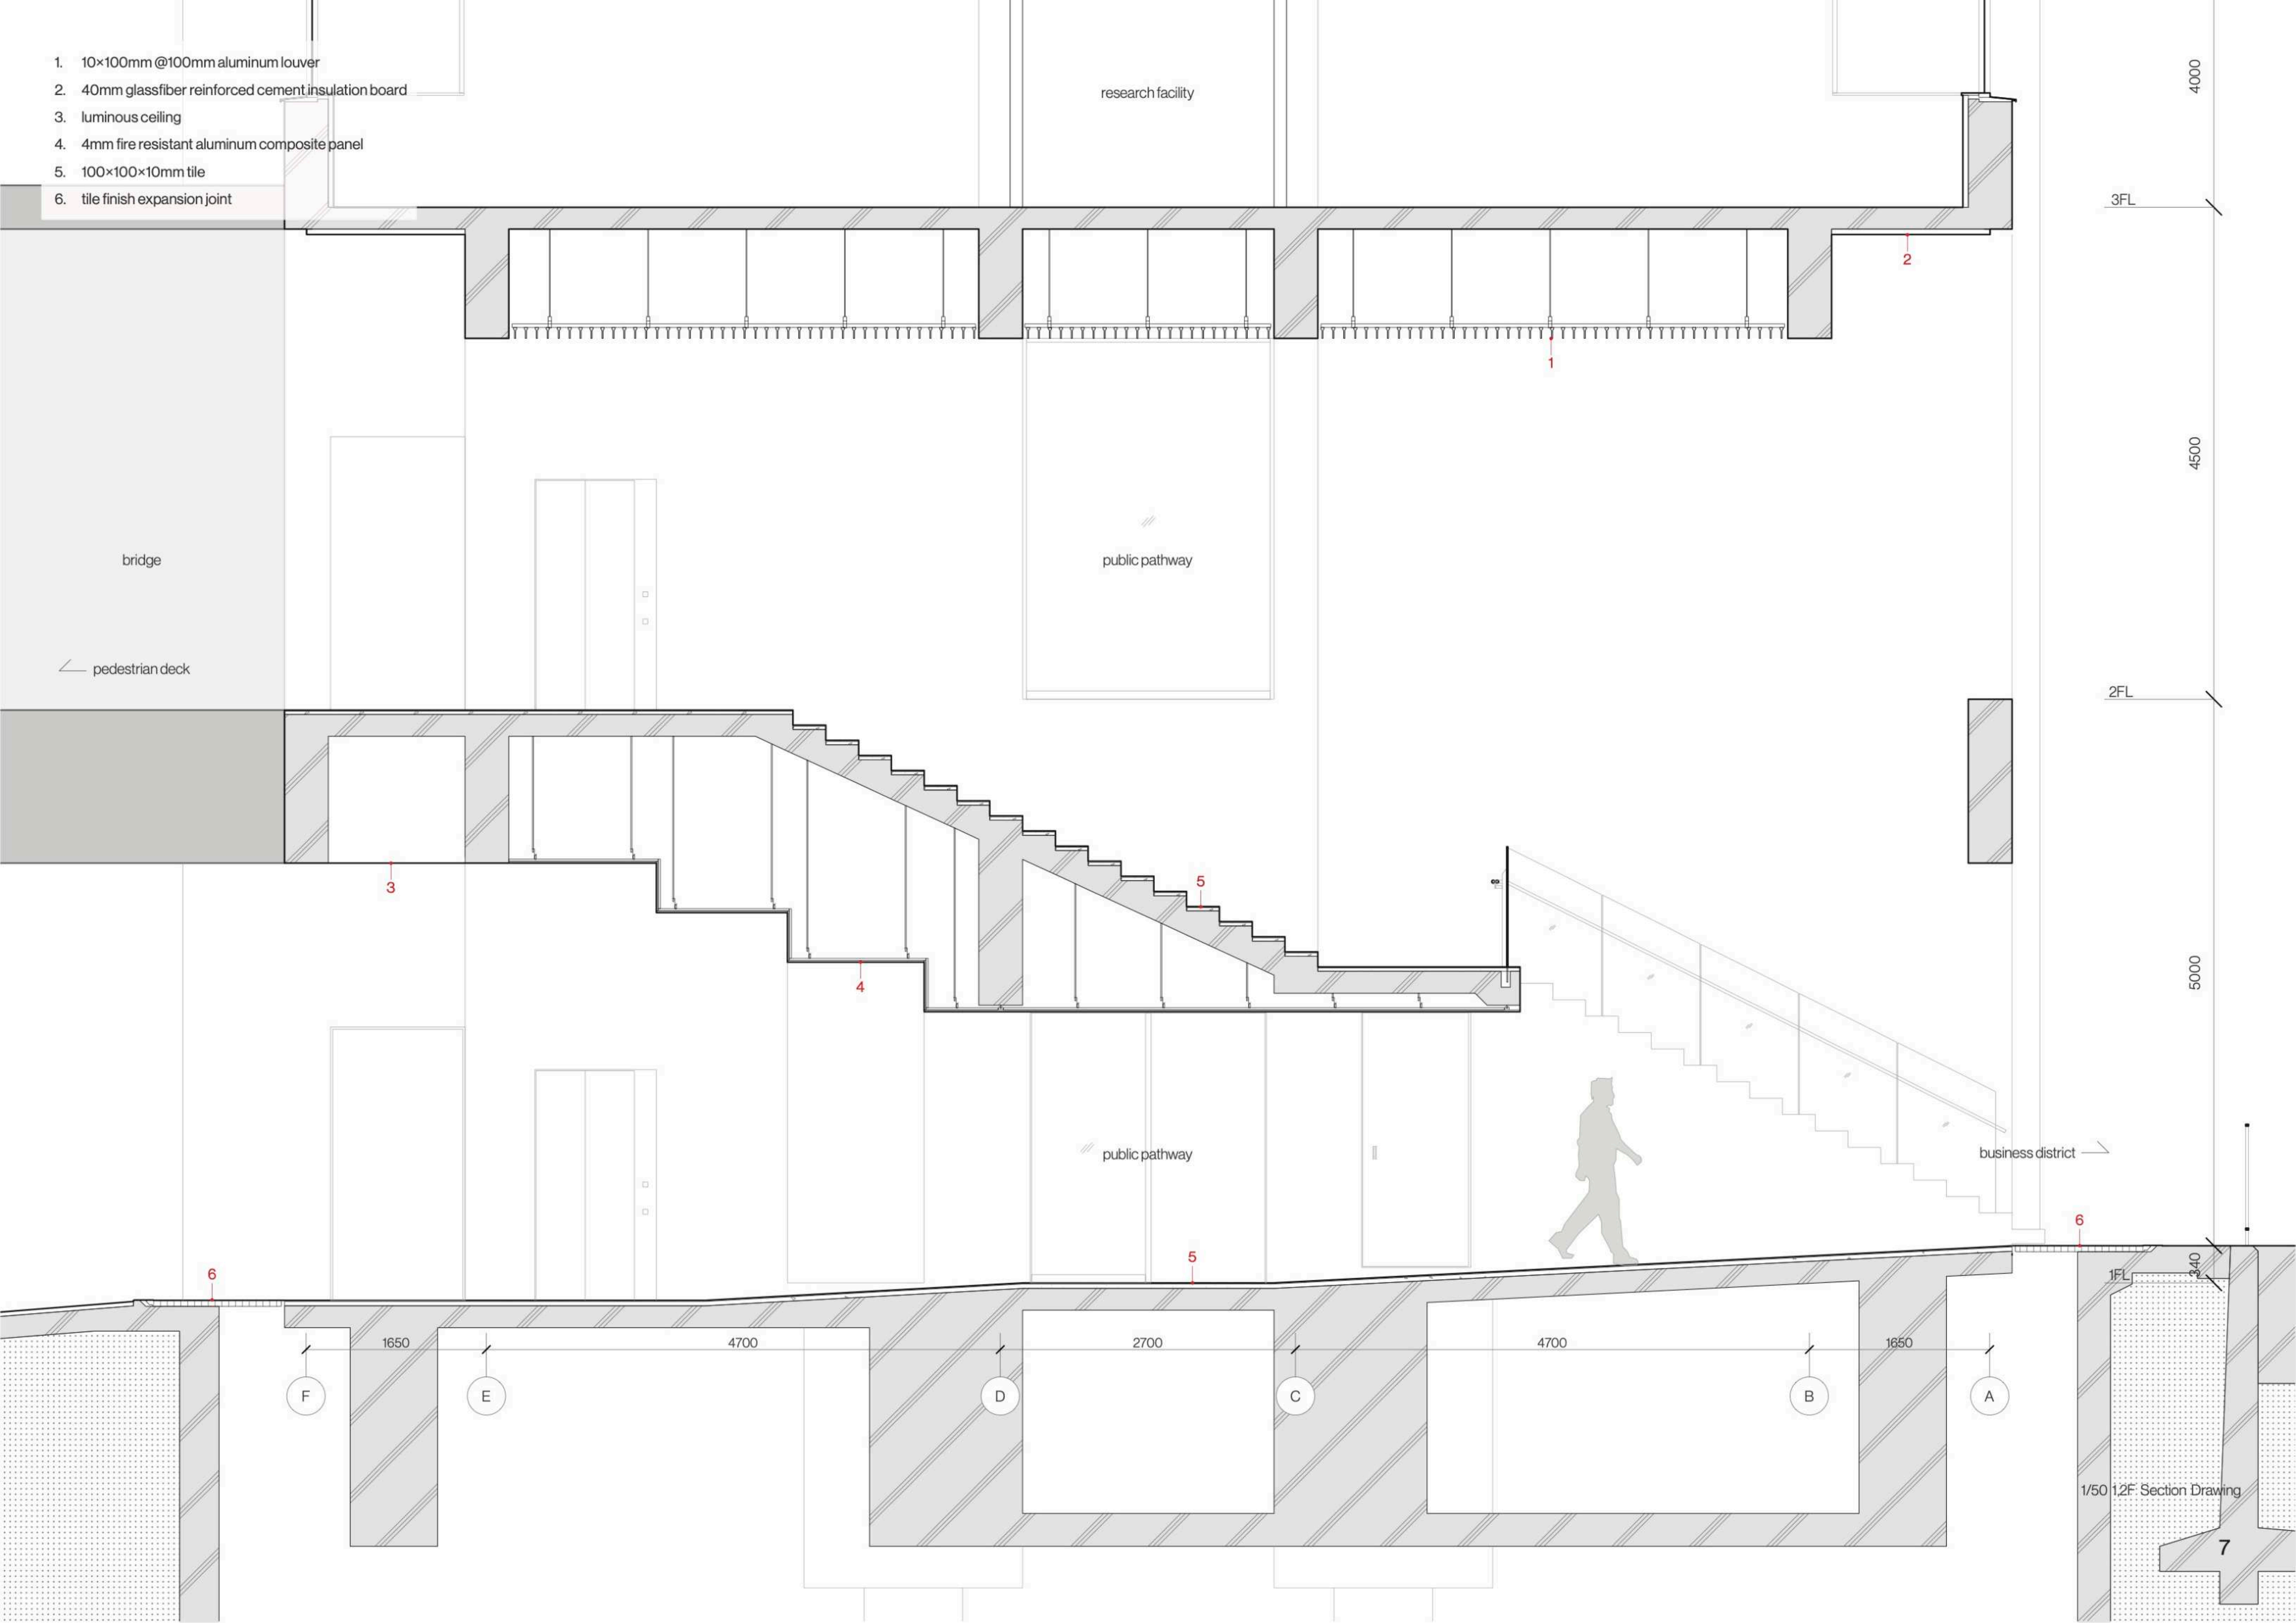

4000

3FL

4500

2FL

5000


1FL

340

1/50 1,2F Section Drawing


7

- 1. 1.6mm steel sash & frame
- 2. 1.5mm aluminum glazing bead
- 3. center pivot hinge

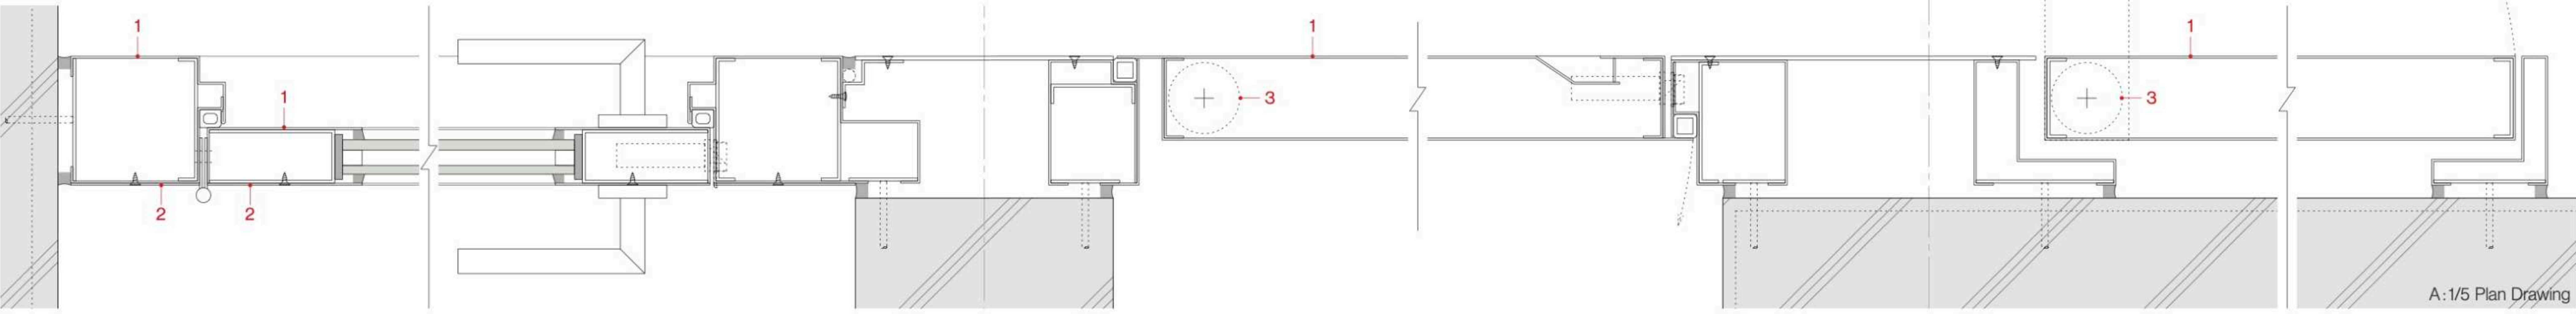

A:1/5 Plan Drawing


- 4. louver
- 5. 30×30×3mm L shaped angle door frame
- 6. 1.5mm perforated aluminum
- 7. key operated panel lock
- 8. flush bolt
- 9. 60×6mm steel plate
- 10. rubber door stop
- 11. 50×50×6mm L shaped angle pillar
- 12. 60×6mm steel plate

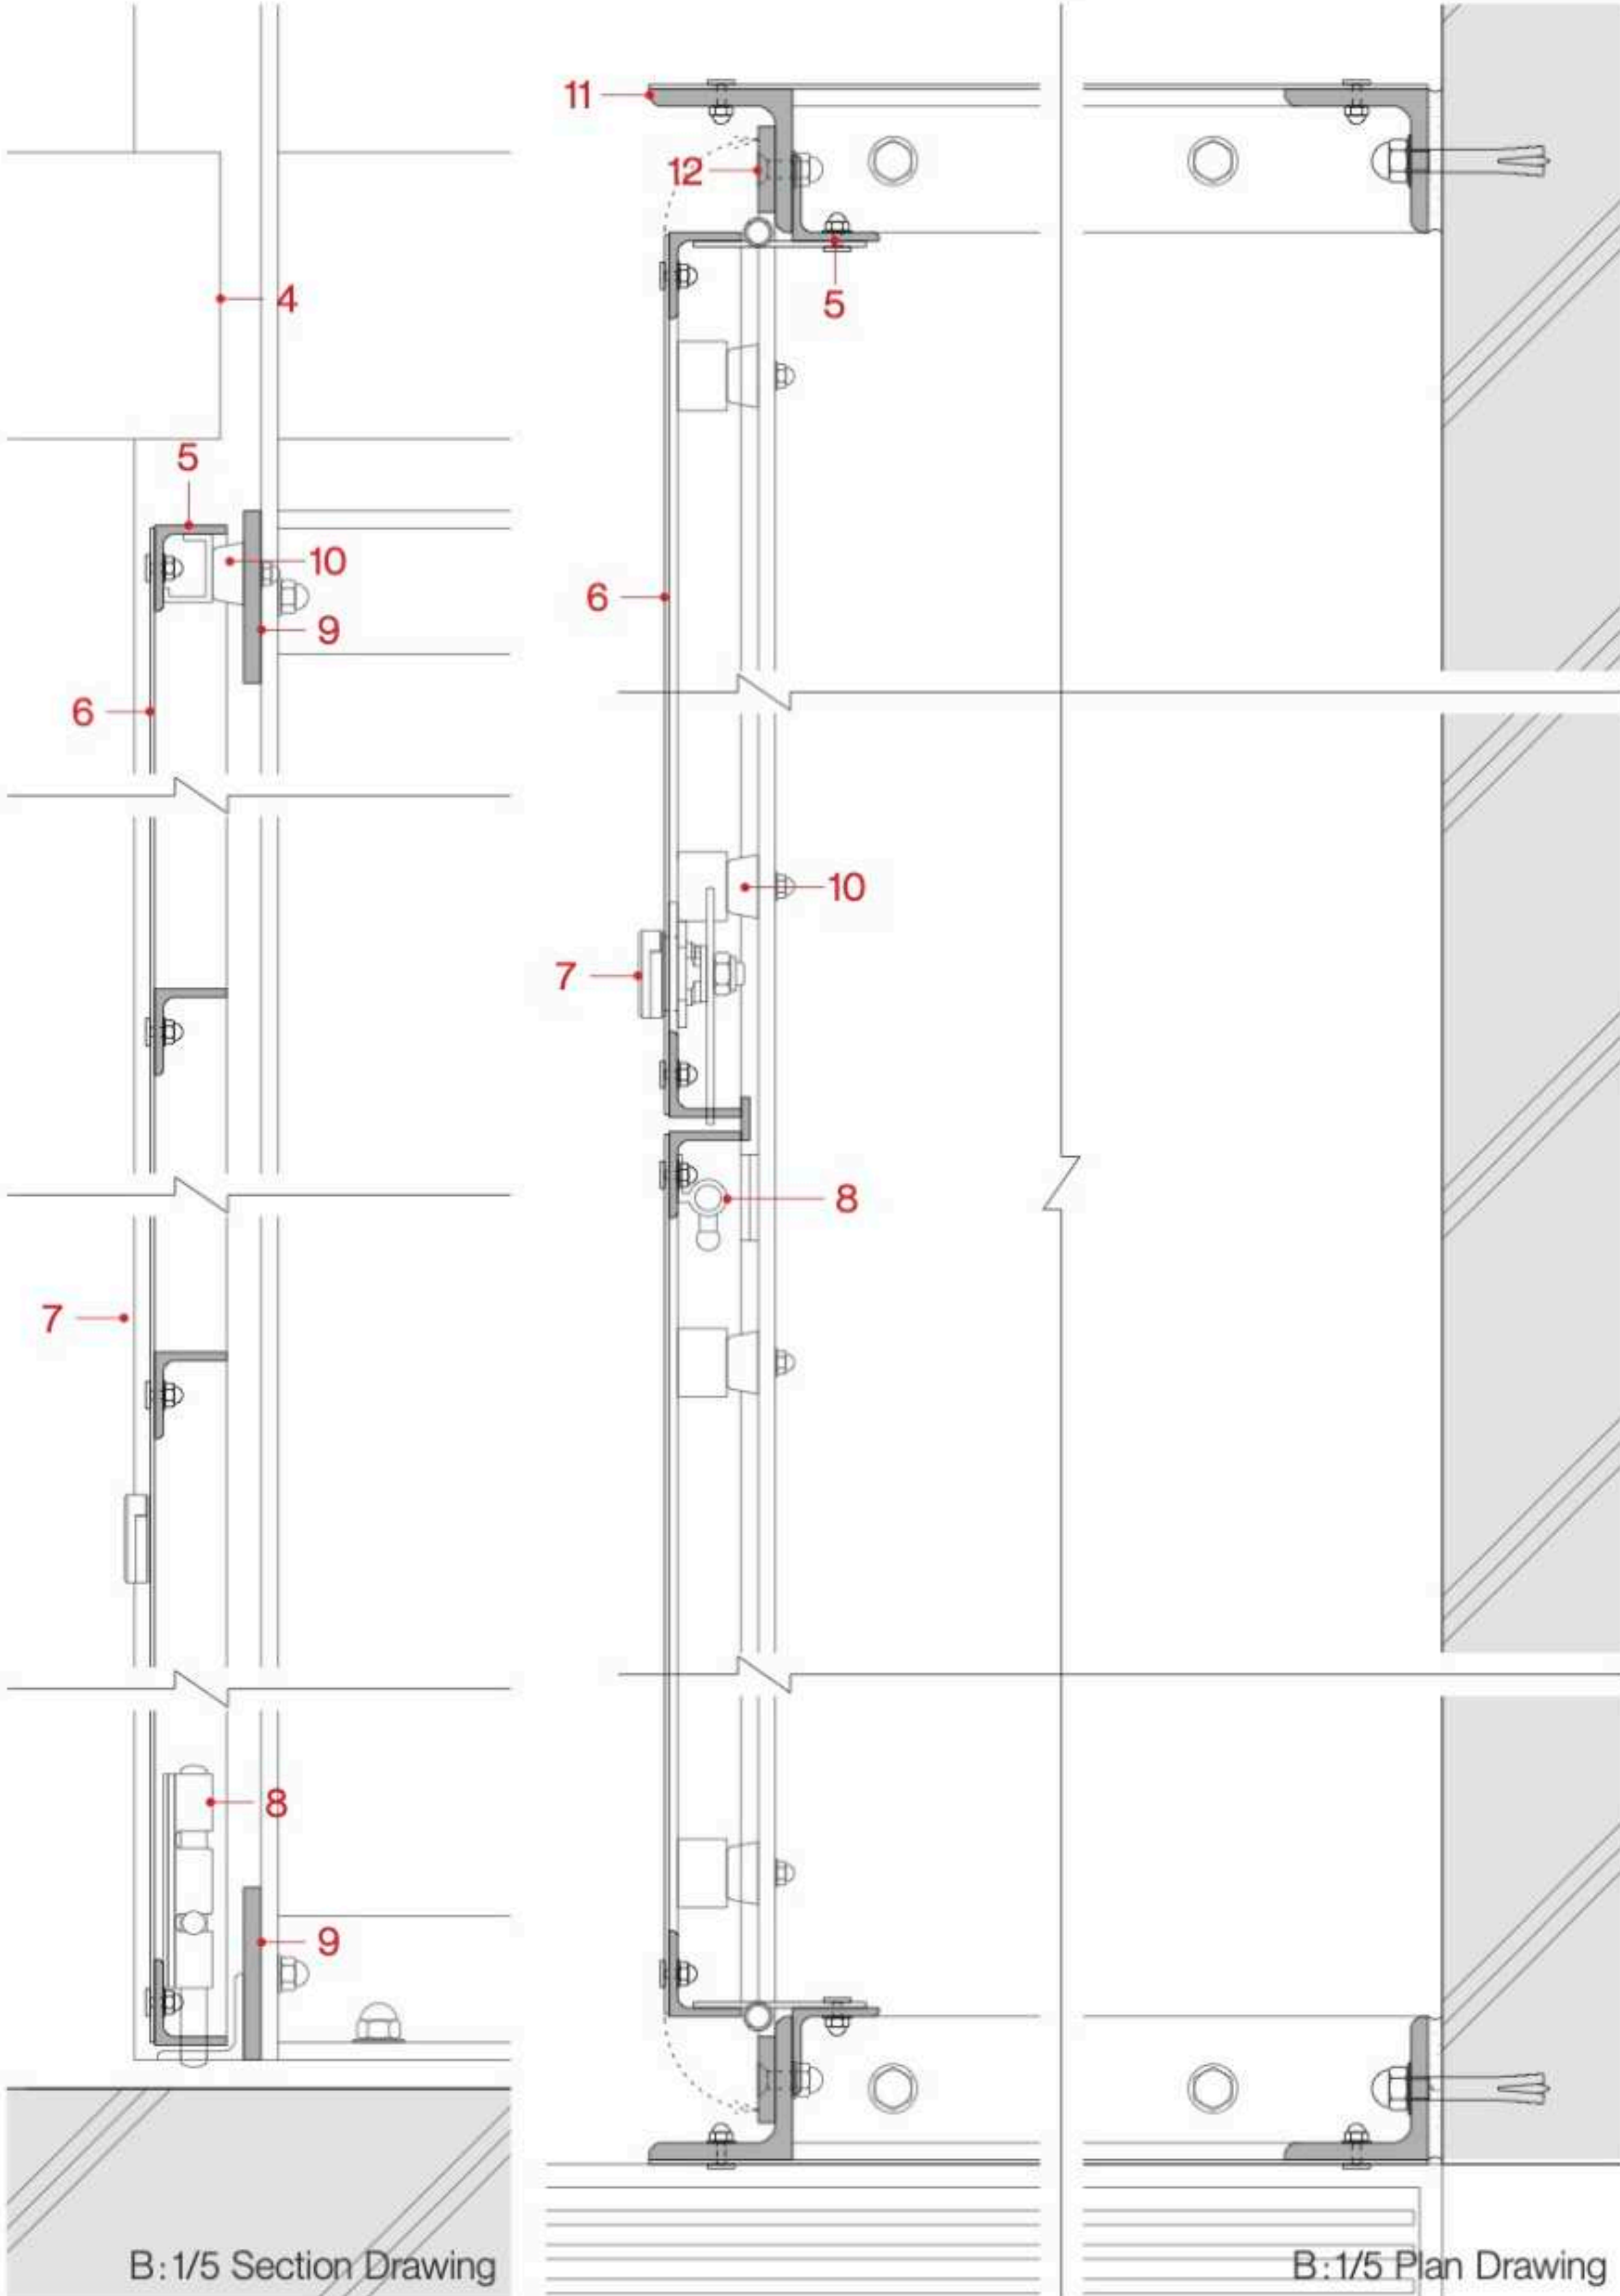

B:1/5 Section Drawing


B:1/5 Plan Drawing

- 13. automatic door
- 14. 3mm steel plate
- 15. fire shutter frame
- 16. fire shutter
- 17. automatic door inspection door

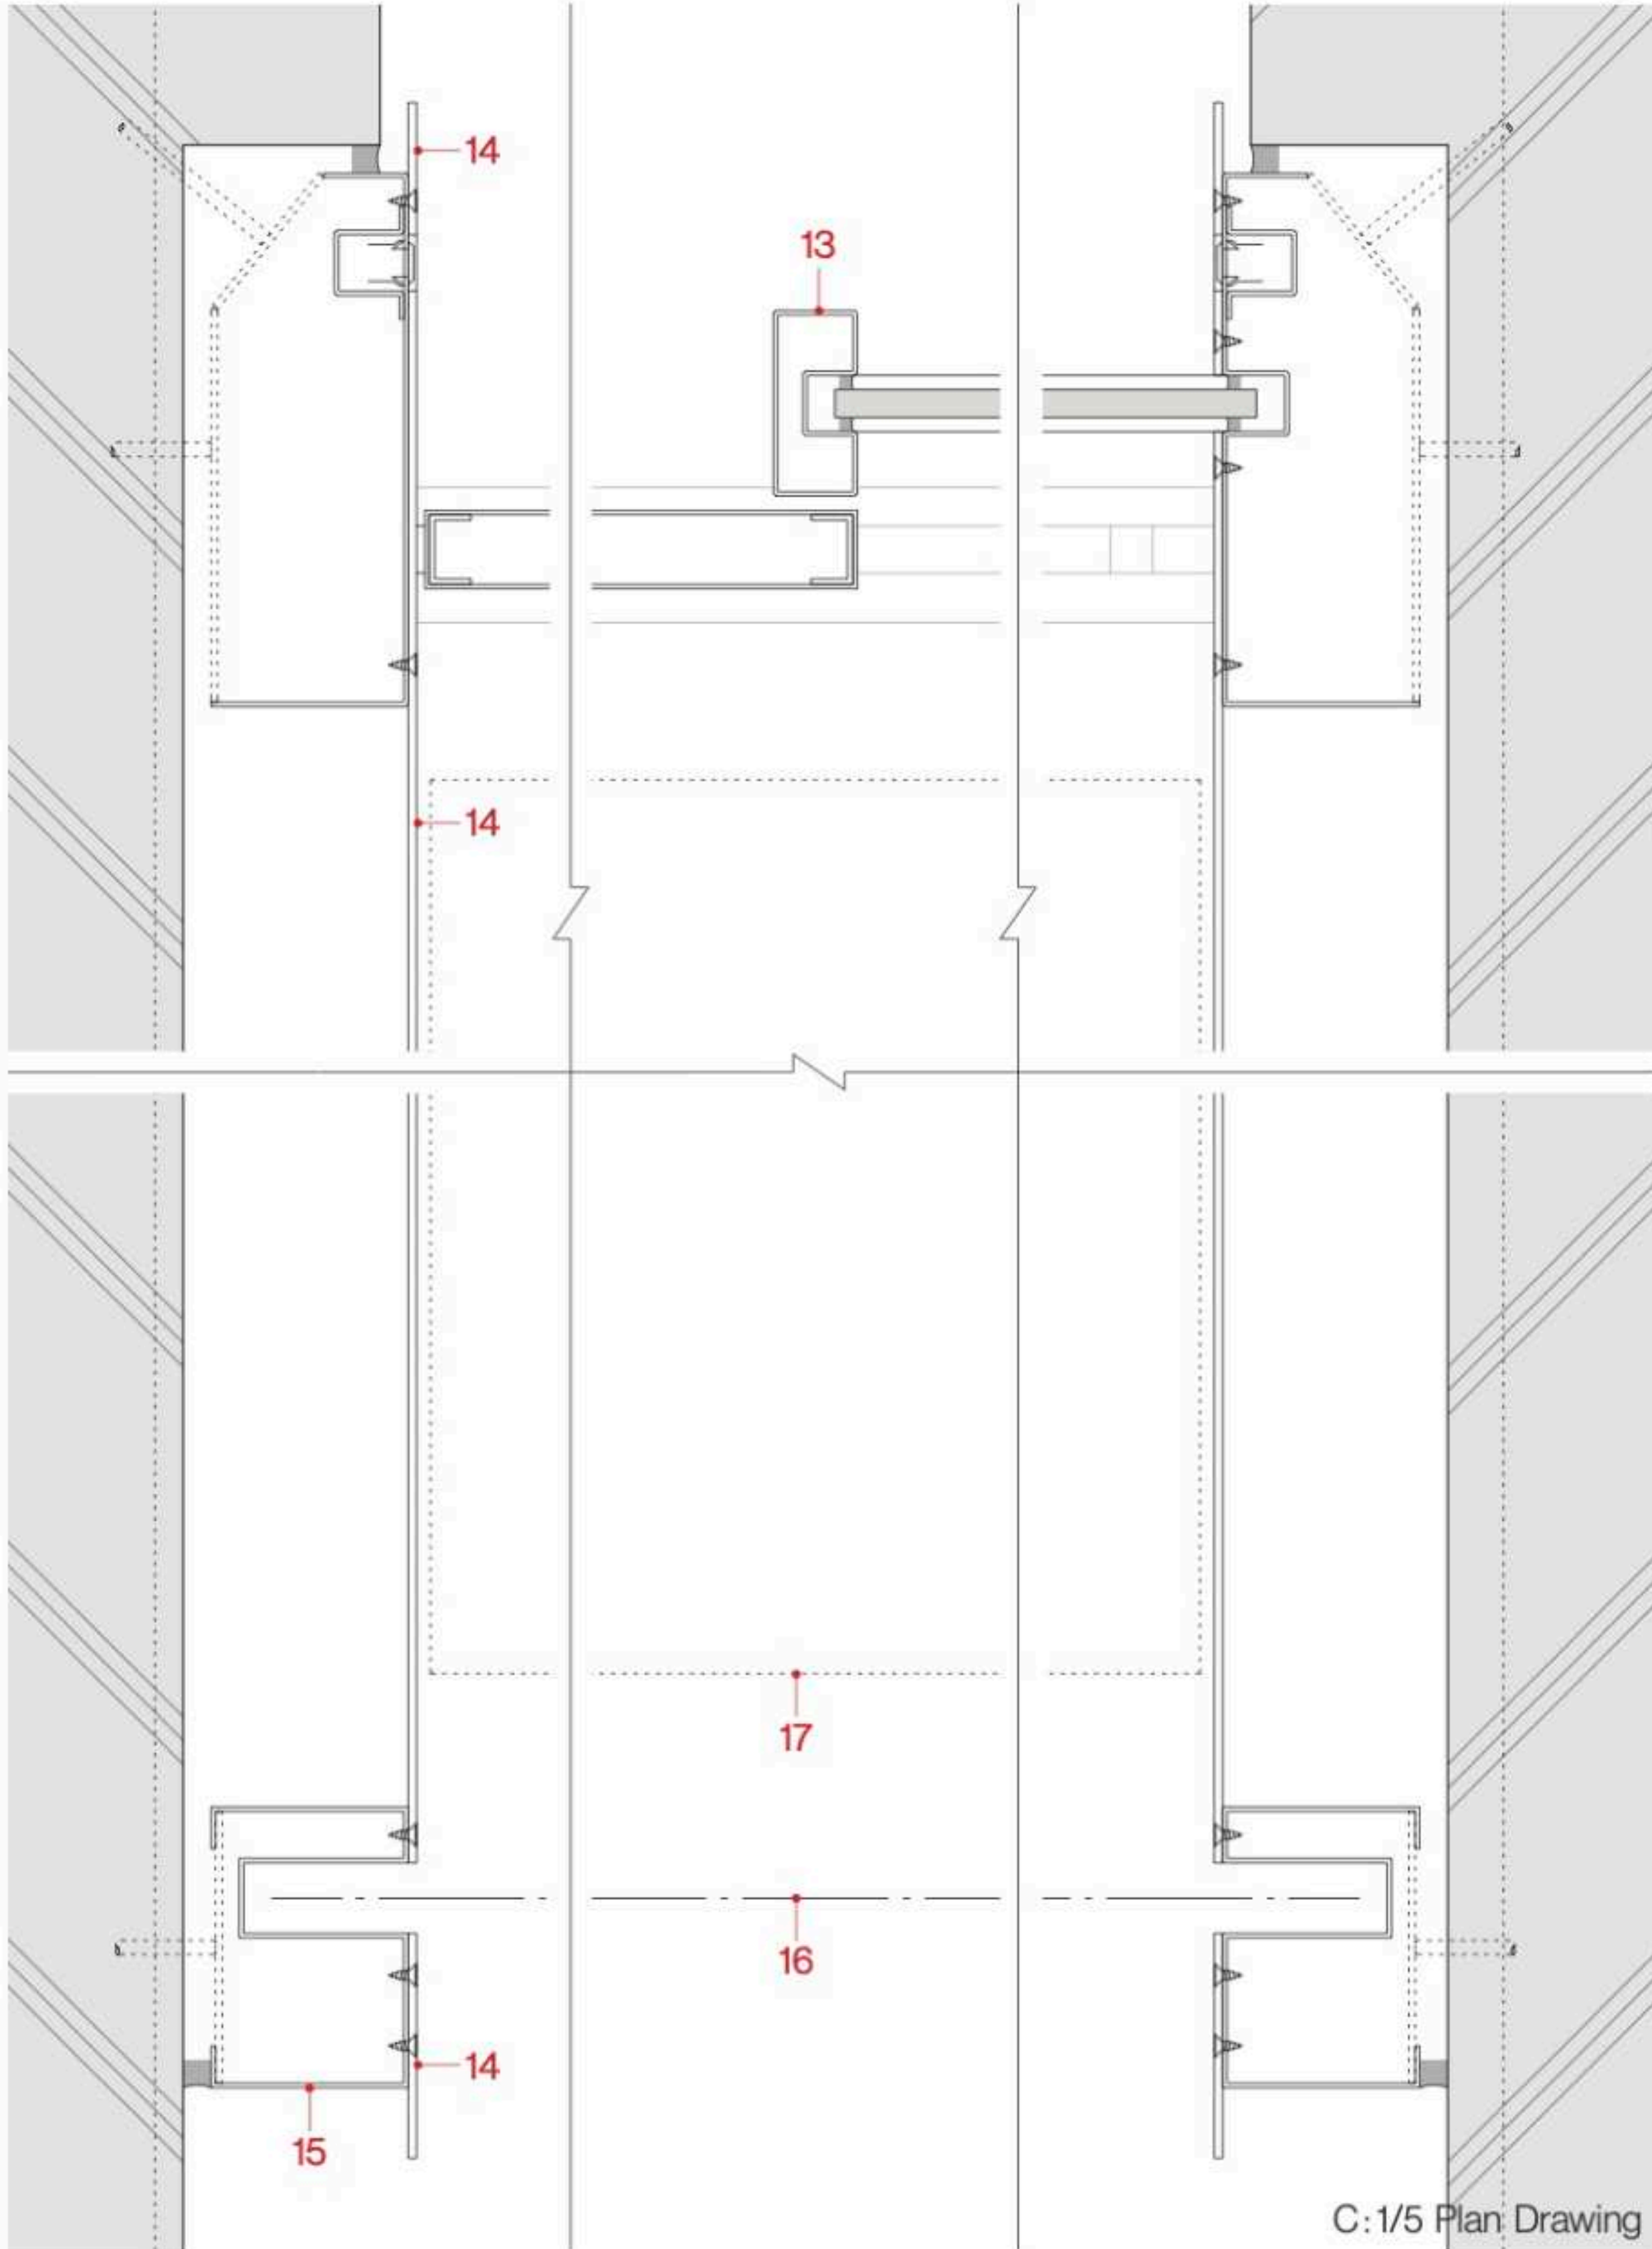

C:1/5 Plan Drawing

- 18. flush handle
- 19. surface-mounted cylinder lock
- 20. board
- 21. 65×65×5mm L shaped angle frame
- 22. 5mm steel bottom frame

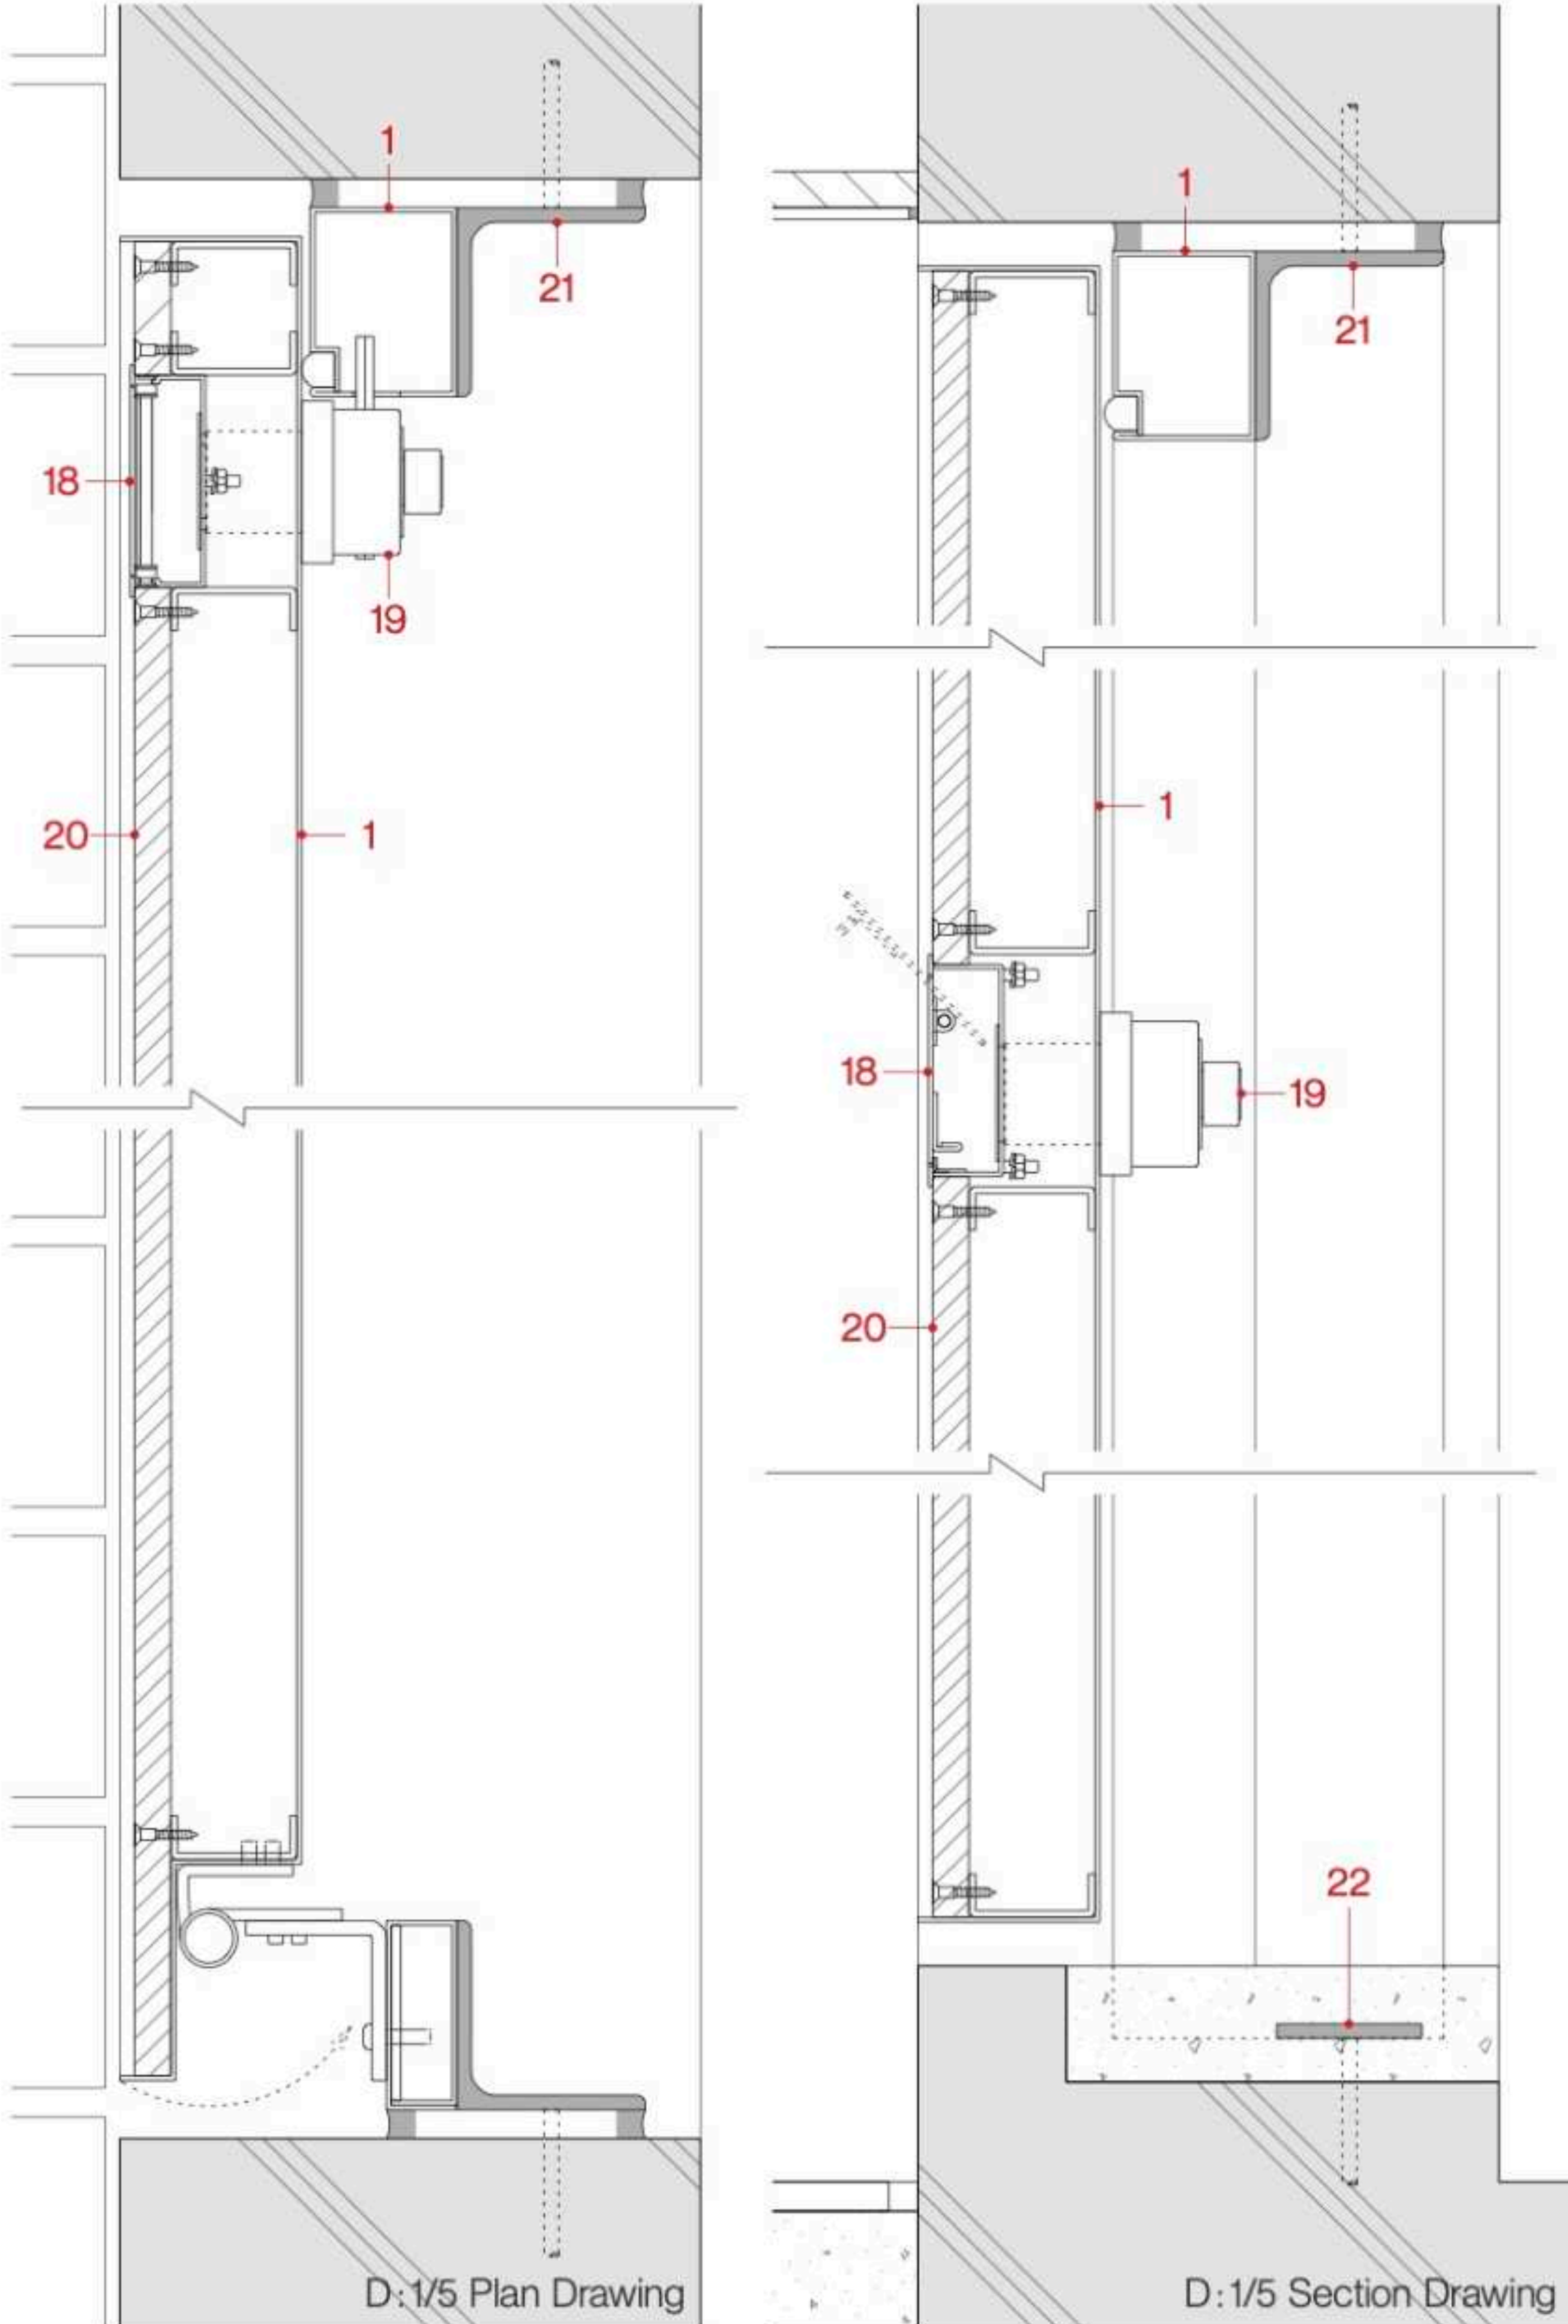

D:1/5 Plan Drawing


D:1/5 Section Drawing

鉄骨階段

貫通通路の 1F と 2F を繋ぐ鉄骨階段。自治体により設けられた階段の合計幅の基準を満たすために設けられた。この階段は、この要望に答えつつ、貫通通路の筒状の空間を阻害しないデザインとすることにした。

可能な限り薄く細い部材と浮遊感のある支持方法、さらに、タイルやコンクリートの色と対照的な暗いグレーを基調とした踏面の仕上げとメッキの色により、隣接する RC 階段や貫通通路全体とは全くの異物であるという印象を与えている。

無垢の鉄筋を用いた支持柱と、鉄パイプを用いた手摺はともに φ50mm にすることで、本来の部材のヒエラルキーに錯覚を起こす。

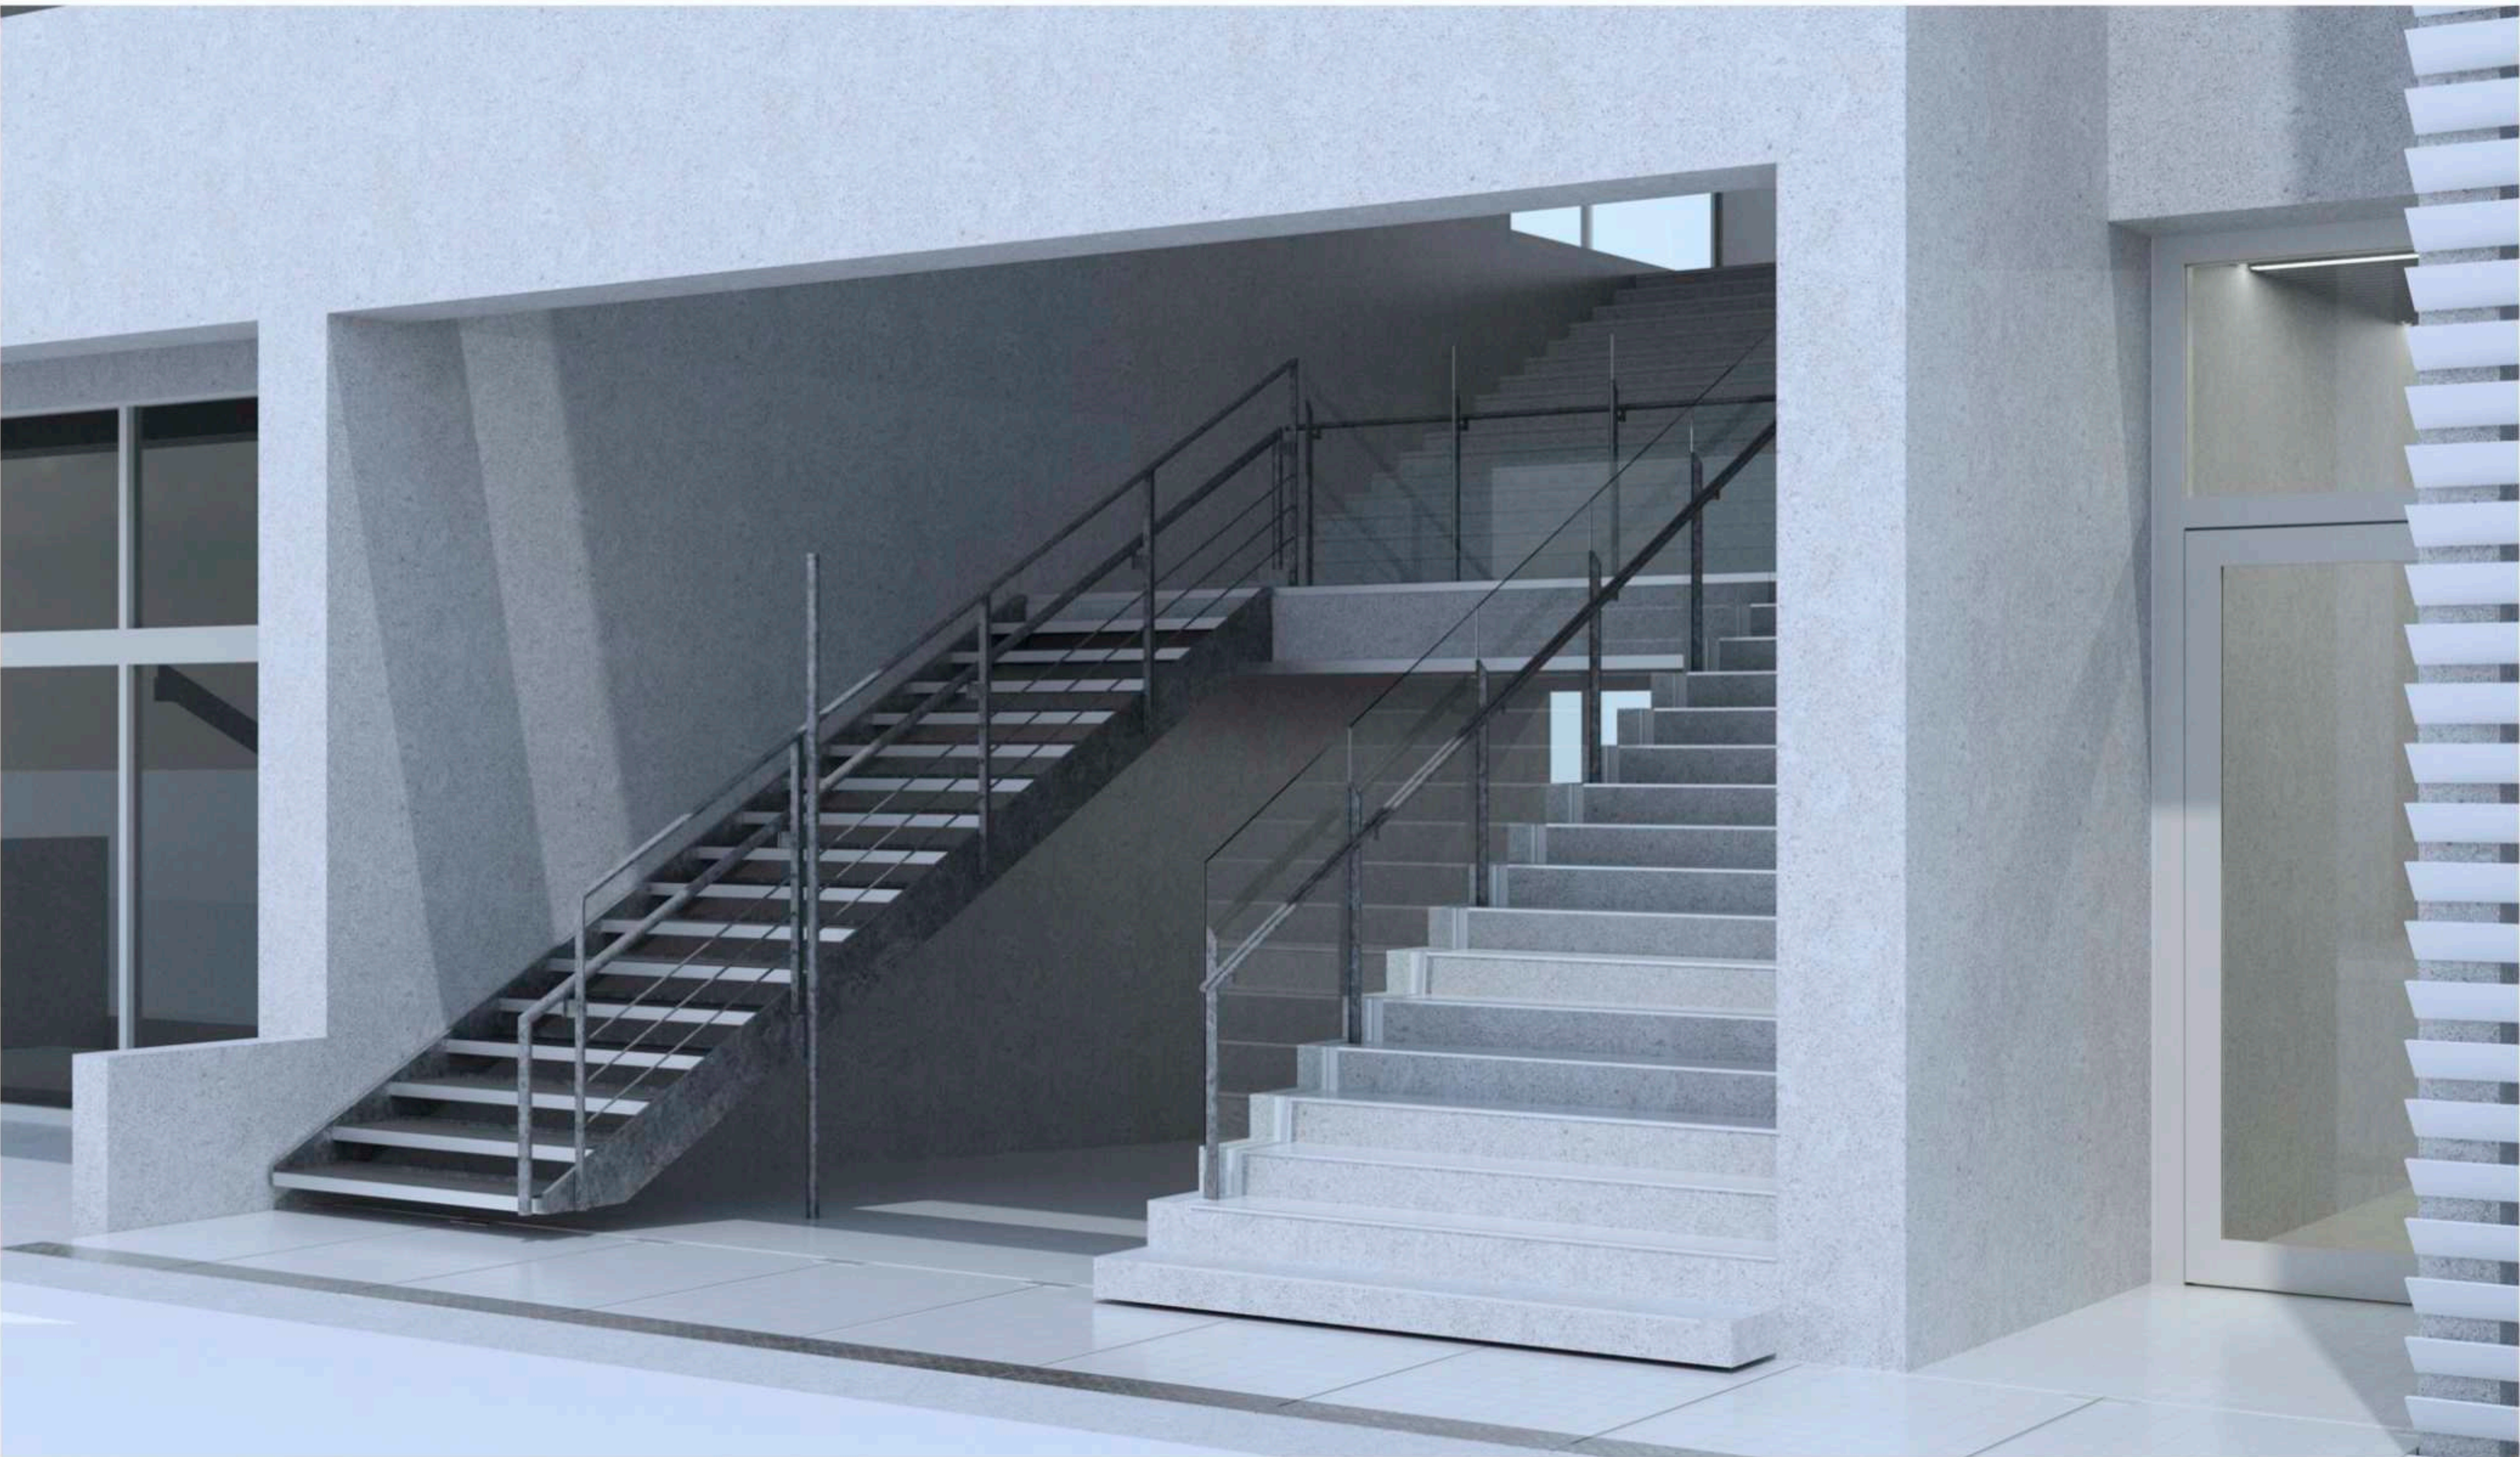

Steel Stairs

This steel staircase connects the first and second floors within the pedestrian passage and was introduced to satisfy municipal requirements for minimum aggregate stair width. While meeting this requirement, the staircase was designed so as not to interrupt the cylindrical spatial quality of the passage.

The use of members as slender and thin as possible, a visually floating means of support, and a tread finish in dark grey — chosen to contrast with the tones of tile and concrete — combined with the colour of the plating, collectively give the staircase the impression of a foreign object entirely distinct from the adjacent RC staircase and the passage as a whole.

Both the support columns, made from solid steel rods, and the handrail, constructed from steel pipe, share a diameter of ϕ 50 mm — a device that introduces a deliberate ambiguity into the perceived hierarchy of structural members.

RC 階段

貫通通路の 1F と 2F を繋ぐ RC 造の階段。この階段と踊り場の柵はガラス、手摺は華奢な鉄パイプを 2 本用いたデザインにすることで、鉄骨階段をより異化させる意匠としている。

また、最下段のみ免震エクスパンションジョイント上にあるため接地できず片持ちになっている。そのため、コンクリートのかぶり厚を確保するために踏面の仕上げはタイルではなく打ち放しとし、段鼻見切り材に関してもステンレス棒をあらかじめ鉄筋に溶接している。

Reinforced Concrete Stairs

This reinforced concrete staircase also connects the first and second floors within the pedestrian passage. The balustrades of the staircase and landing are glazed, and the handrail is composed of two slender steel pipes — a design that serves to further estrange and accentuate the distinctiveness of the steel staircase by contrast.










The bottom step alone cannot meet the floor, as it sits above a seismic isolation expansion joint, resulting in a cantilevered condition. To ensure adequate concrete cover in this situation, the tread finish was left as exposed concrete rather than tile. Additionally, the nosing trim pieces were resolved by welding stainless steel rods to the reinforcement in advance.



- 1. Ø50mm round pipe steel hand rail
- 2. Ø50mm round bar steel pillar
- 3. Ø12mm steel cross bar
- 4. 2.5mm vinyl sheet finish, 3mm stainless nosing, 9mm steel tread
- 5. 21mm steel stringer
- 6. 100×100×10mm tile finish
- 7. 12×40mm steel pillar

- 8. 10mm glass
- 9. Ø30mm round pipe steel hand rail
- 10. 12×40, 3×30mm t-shape steel pillar
- 11. 1.6mm stainless basement
- 12. 100×100×10mm tile finish
- 13. stainless bar nosing
- 14. welding before concrete pouring (only for first step)

- 15. 4mm fire resistant aluminum composite panel
- 16. tile finish expansion joint

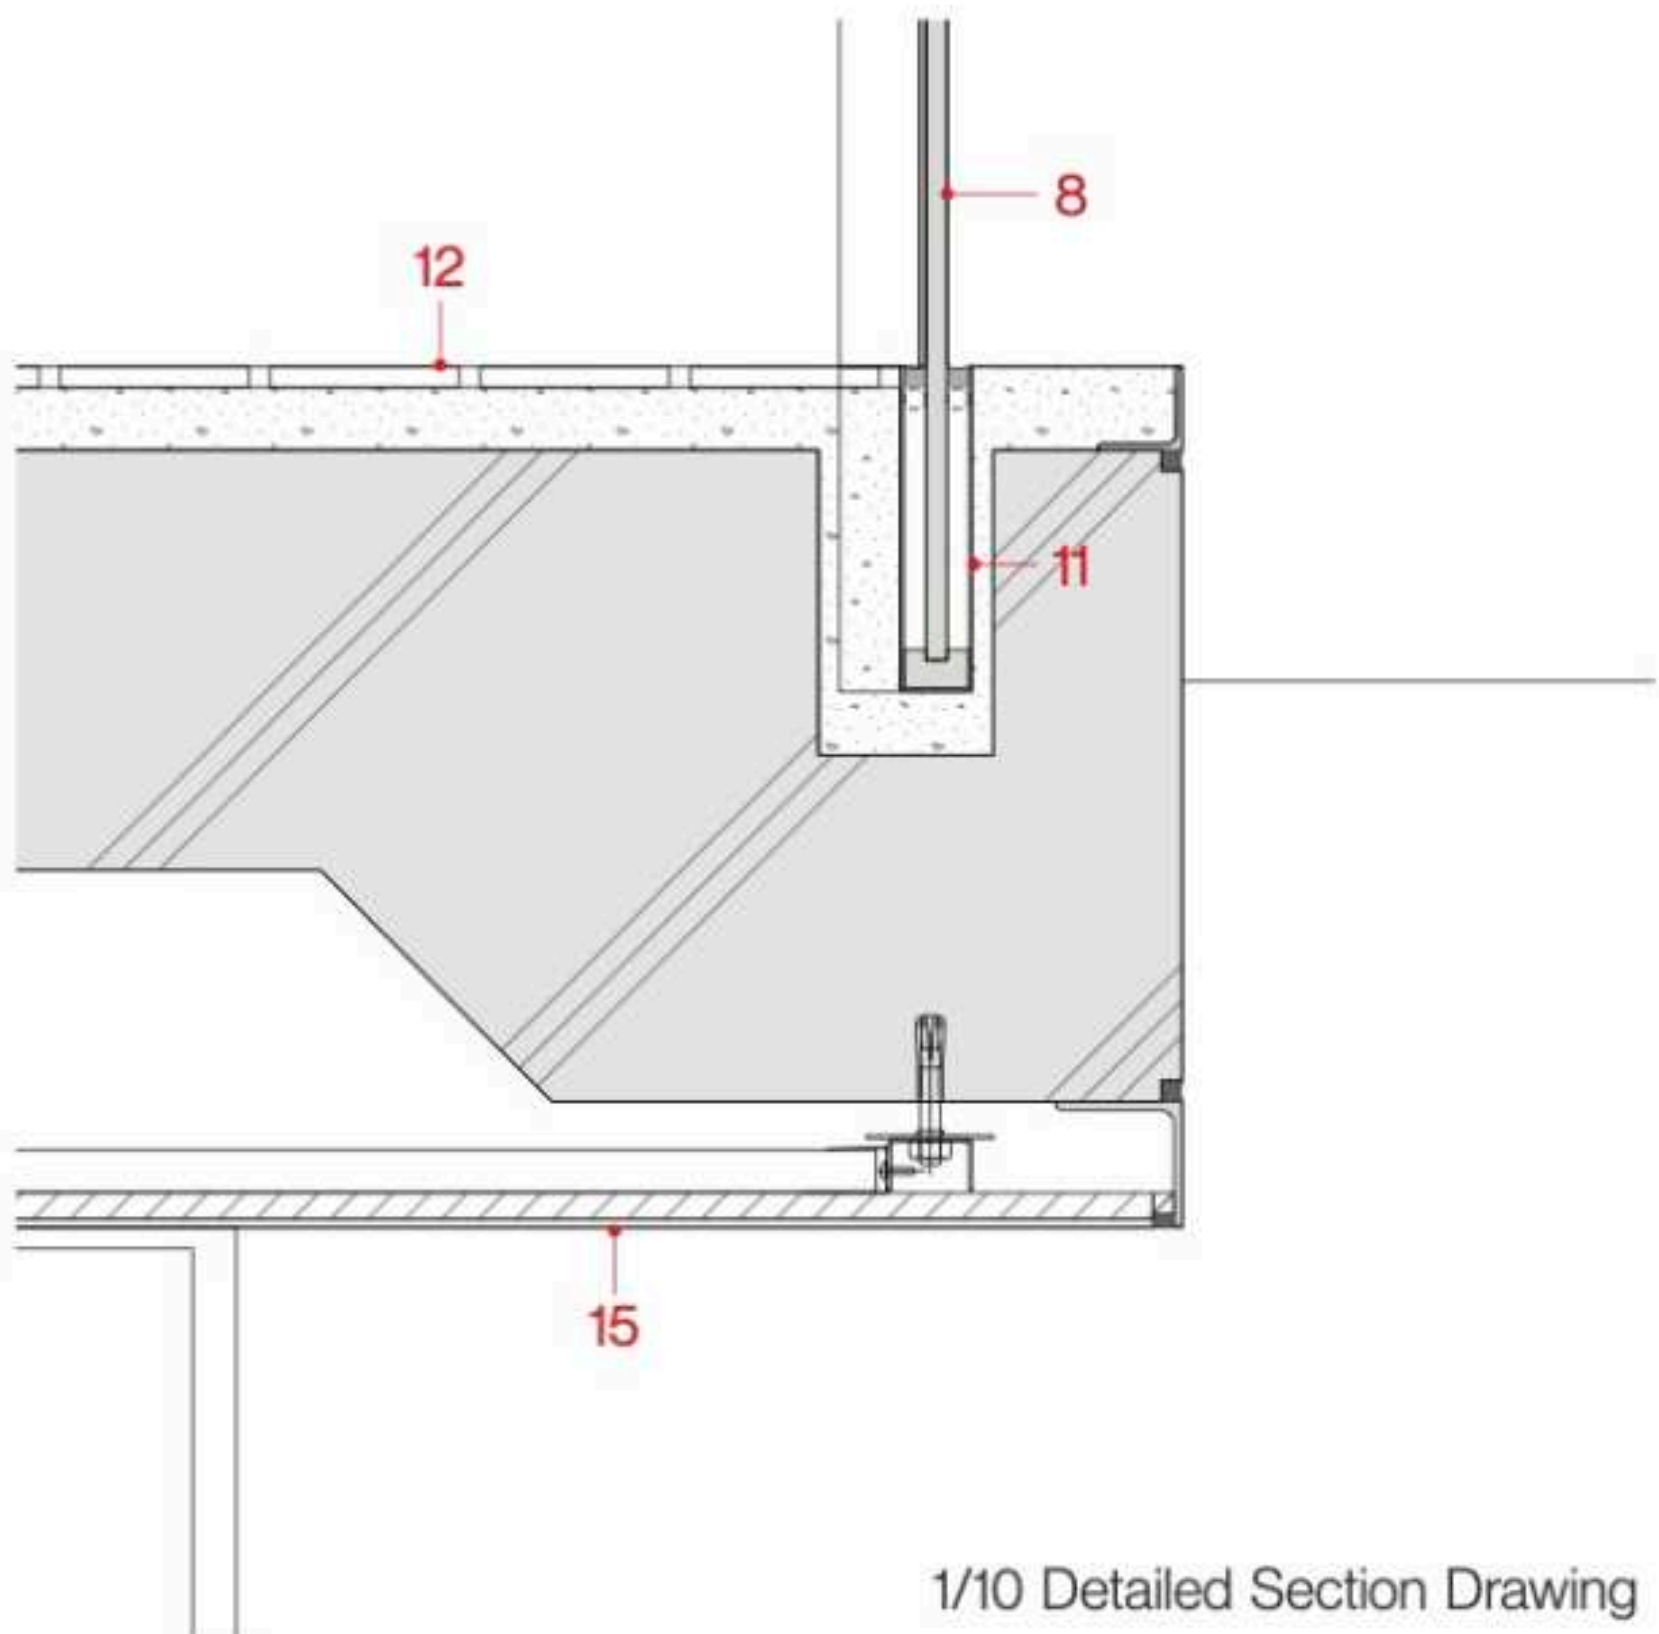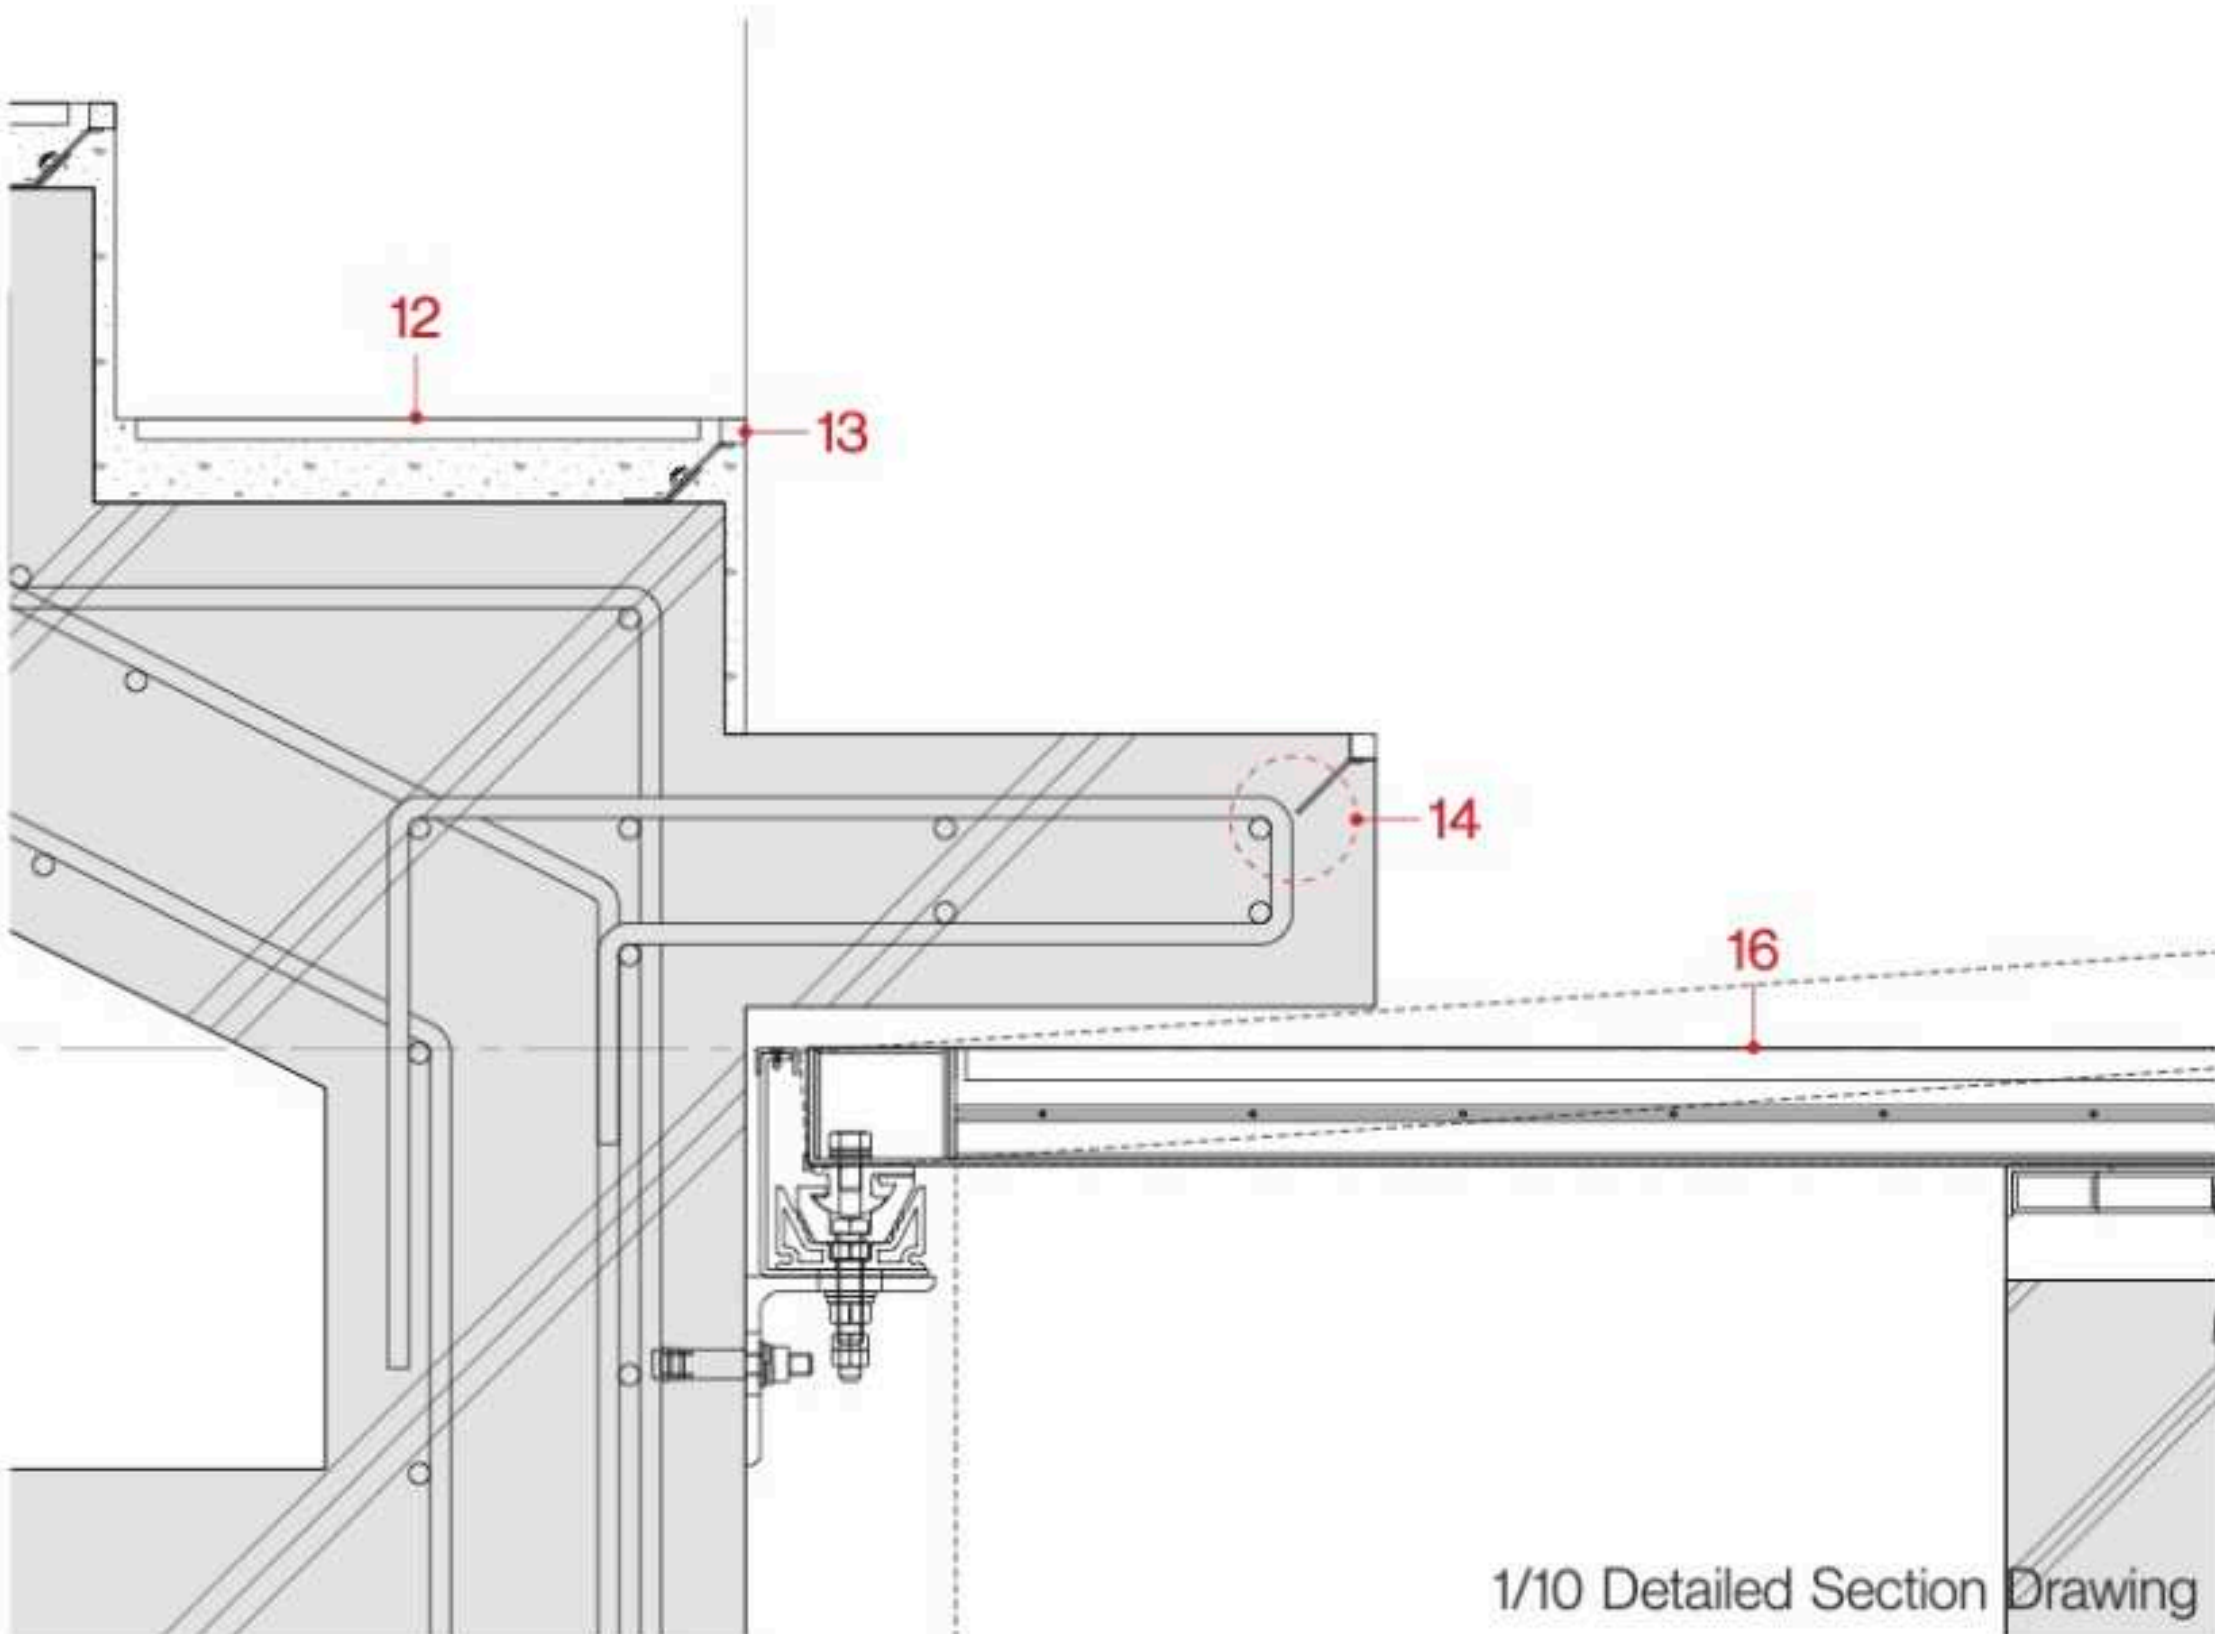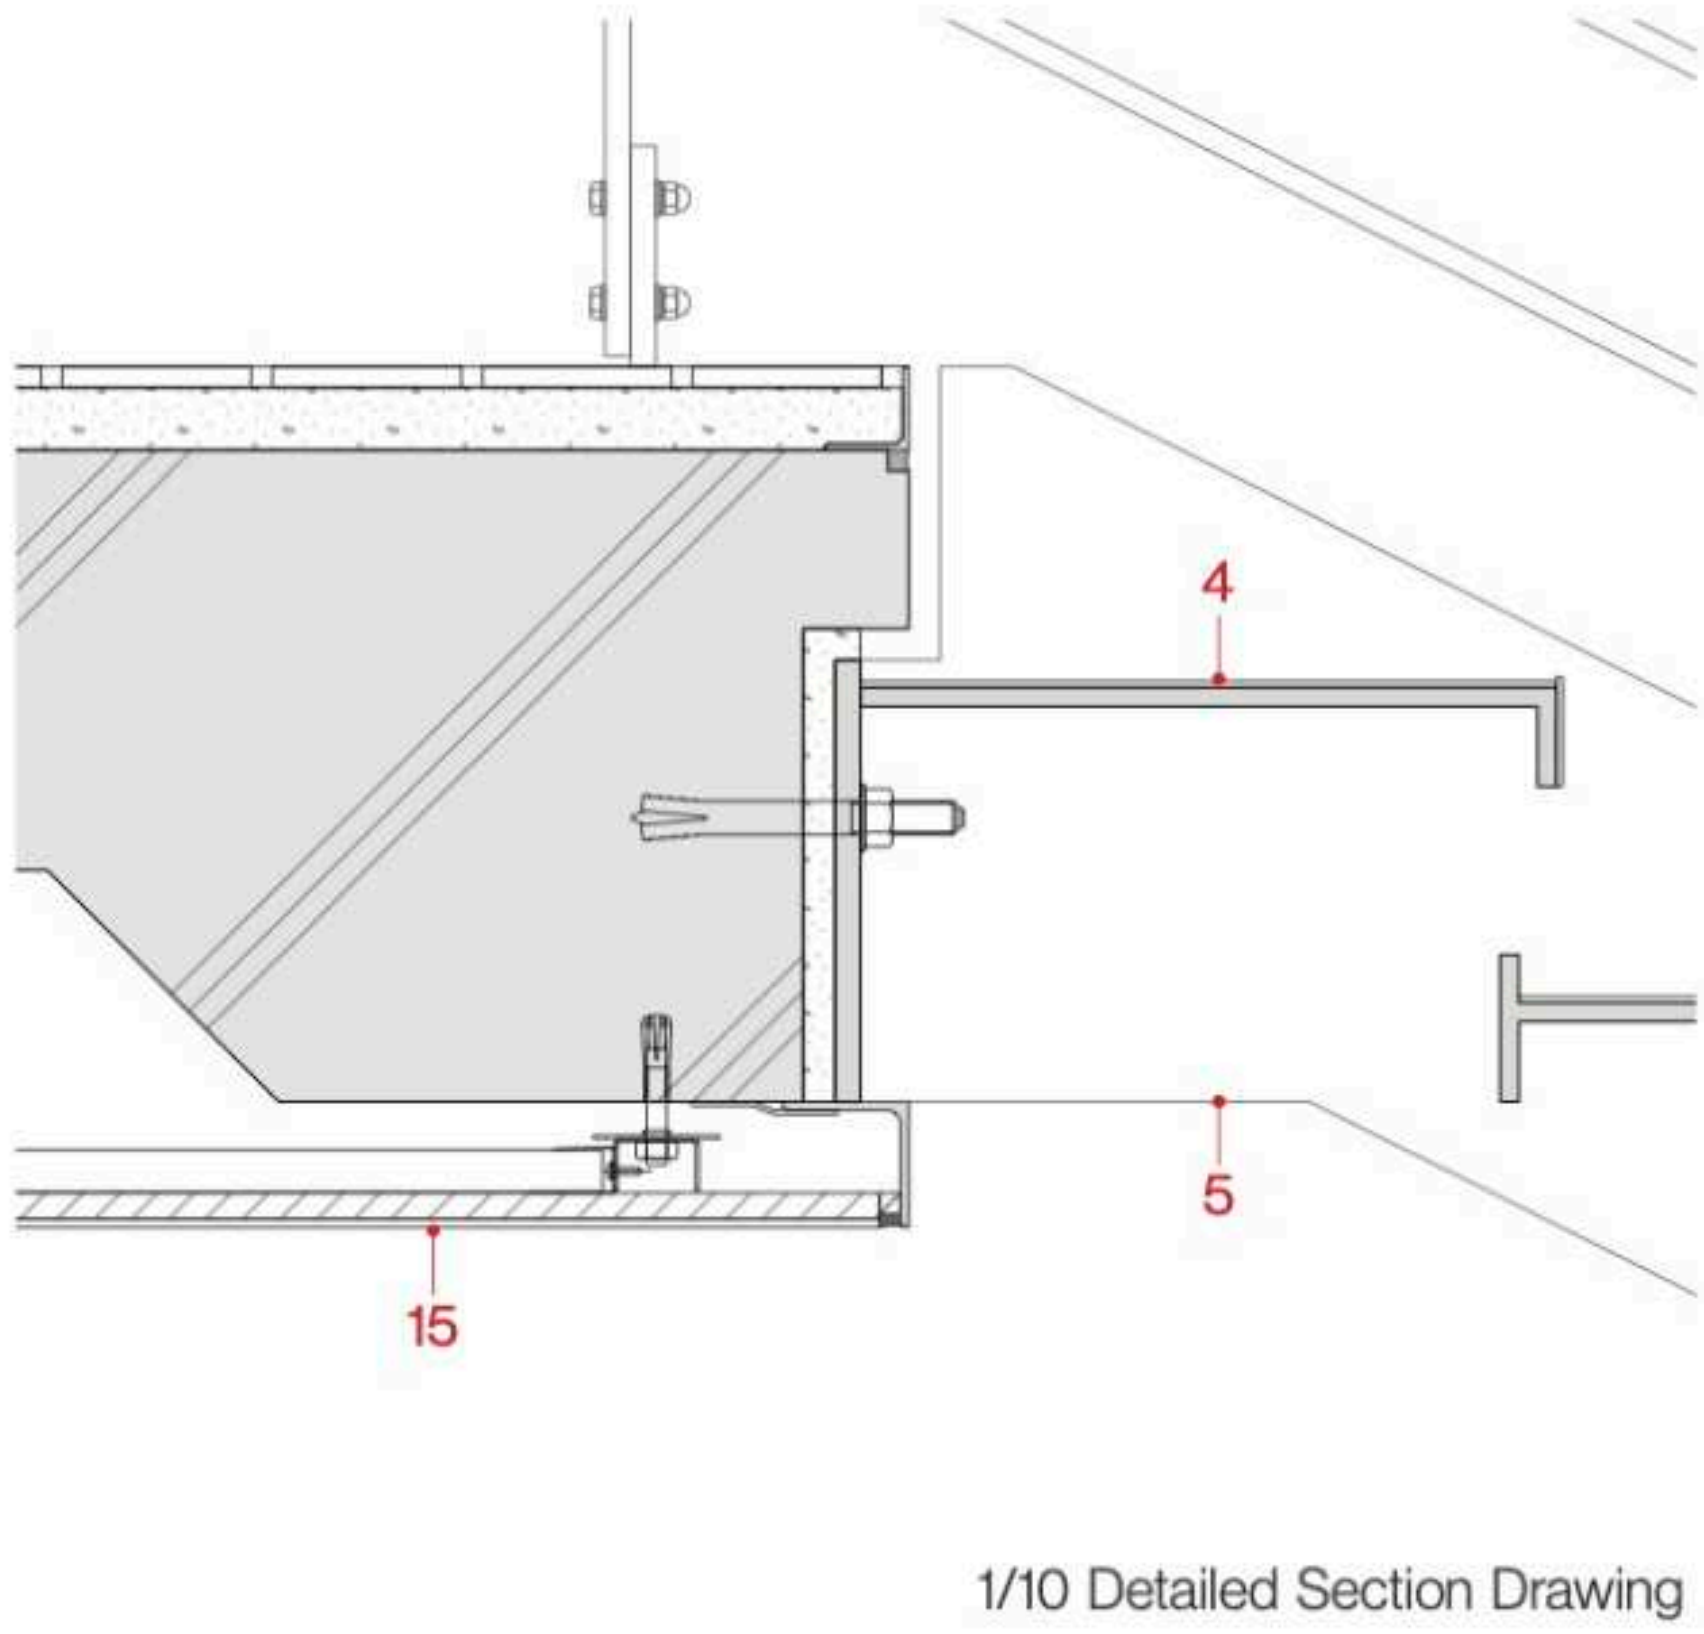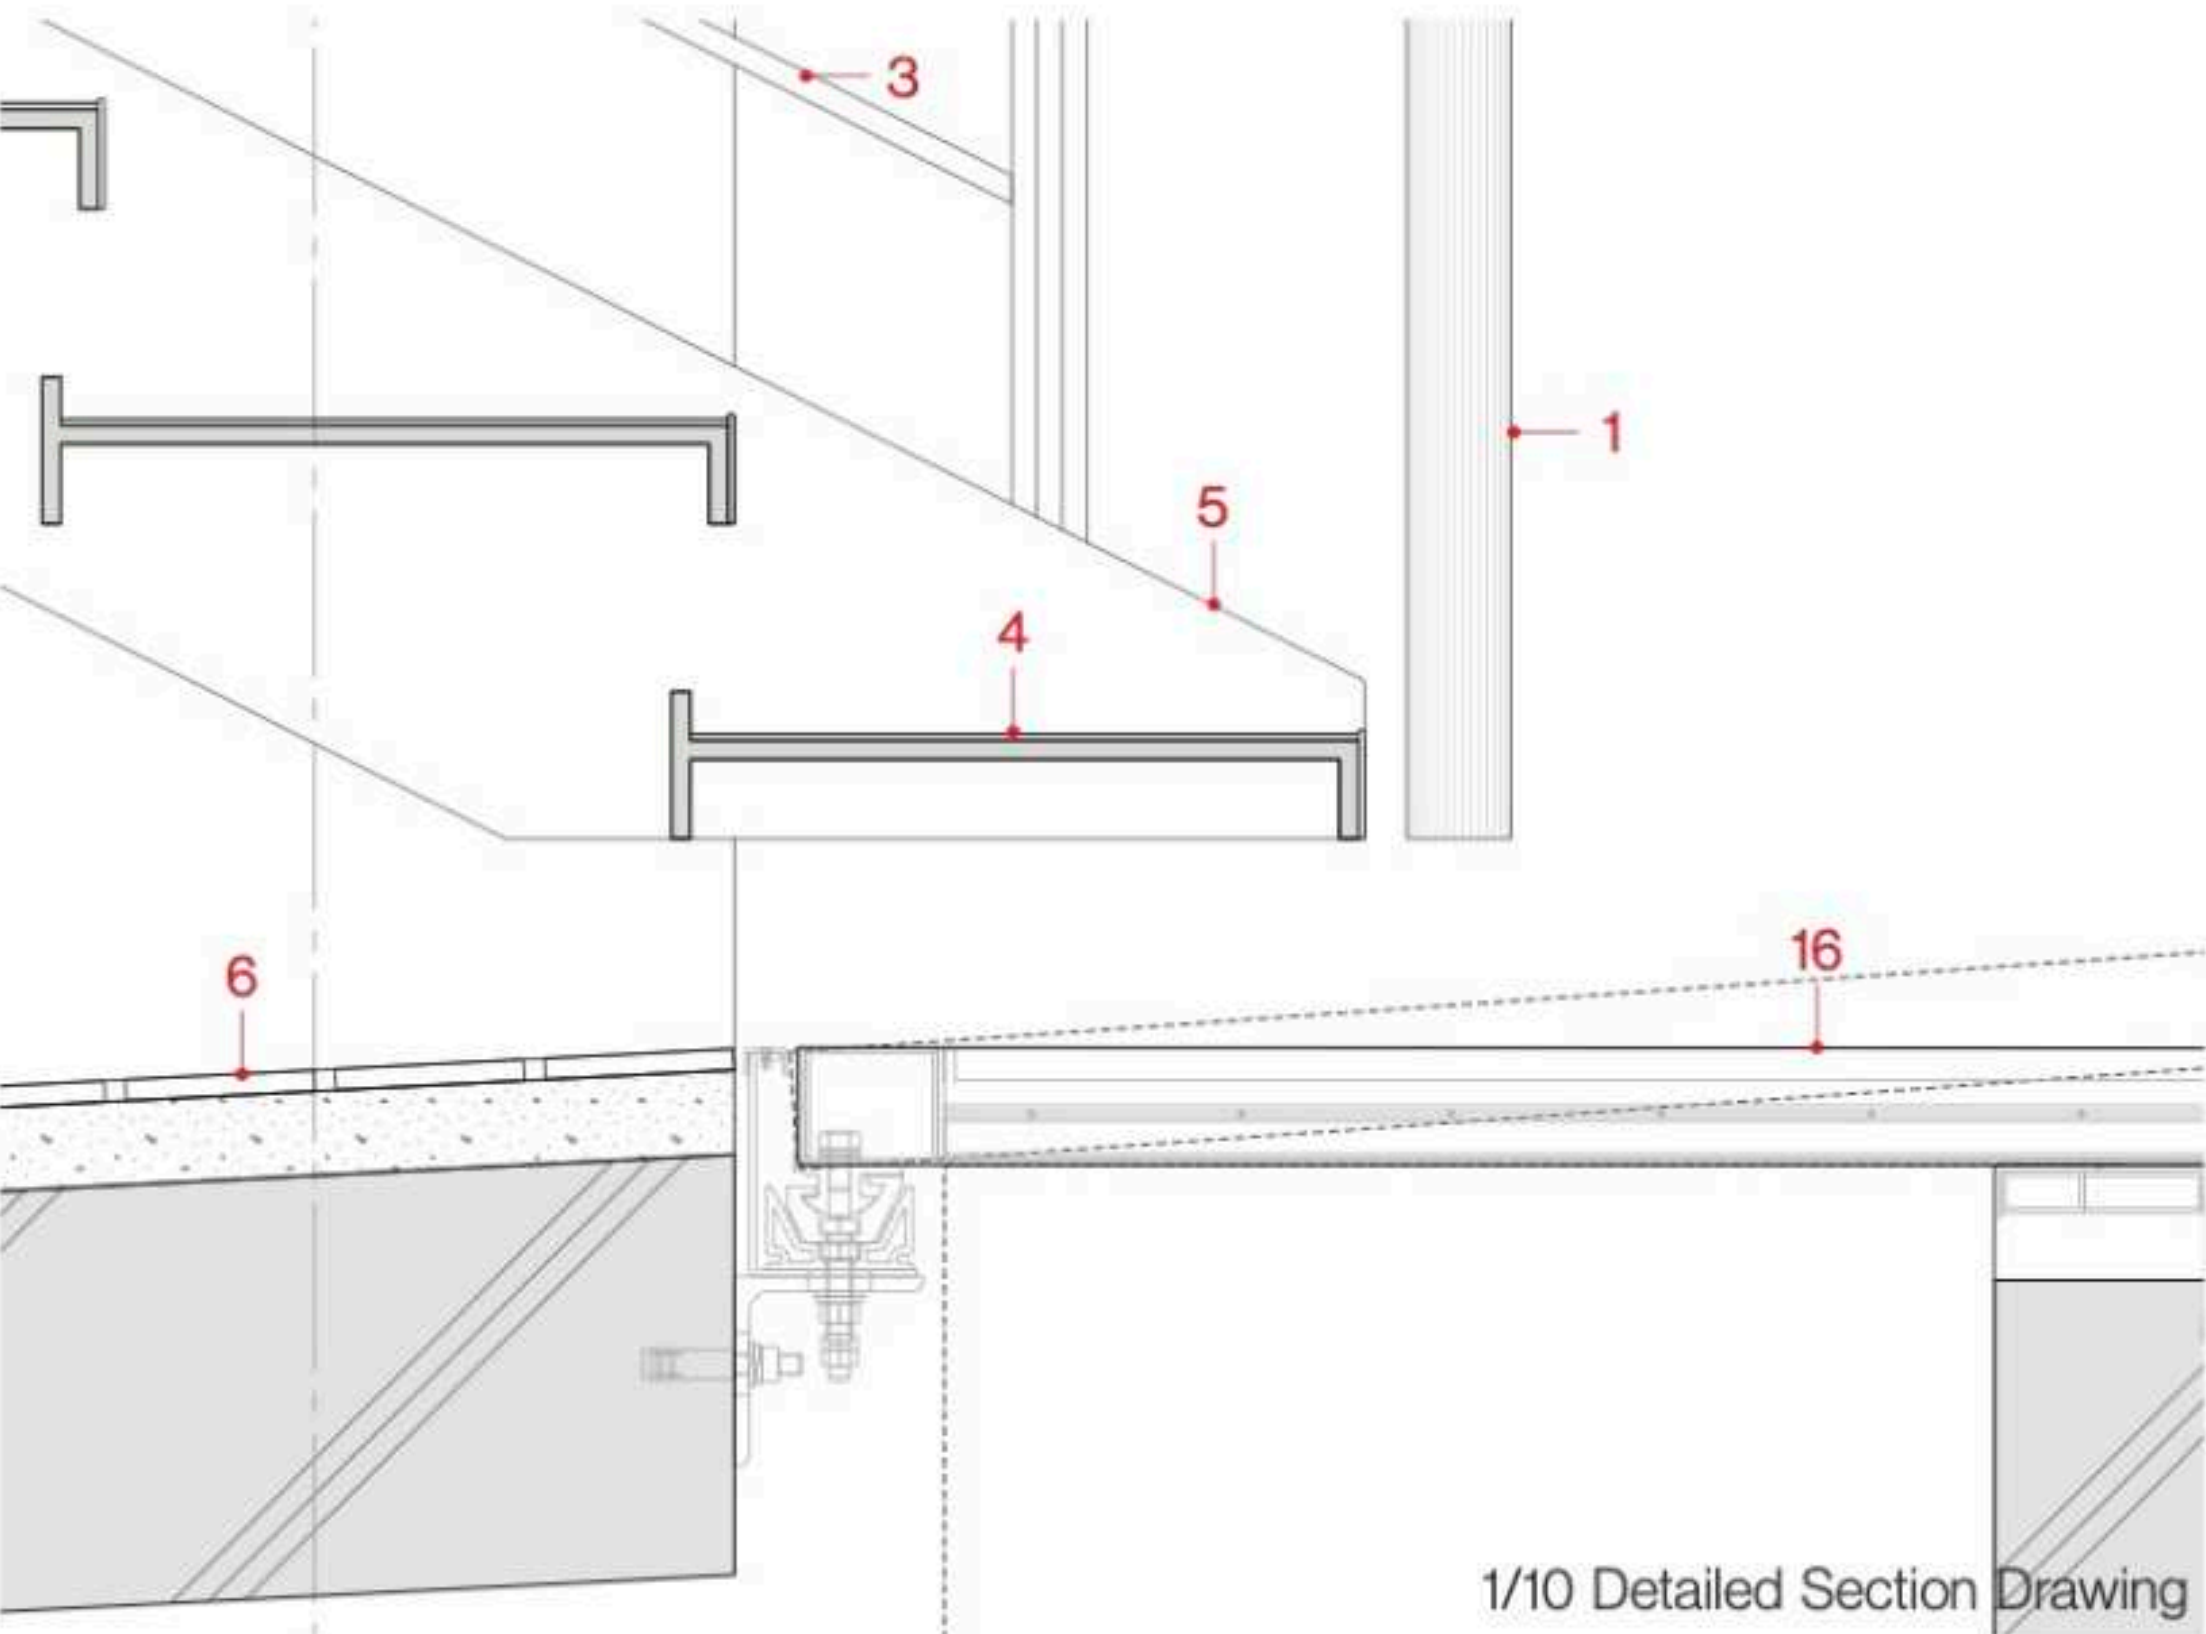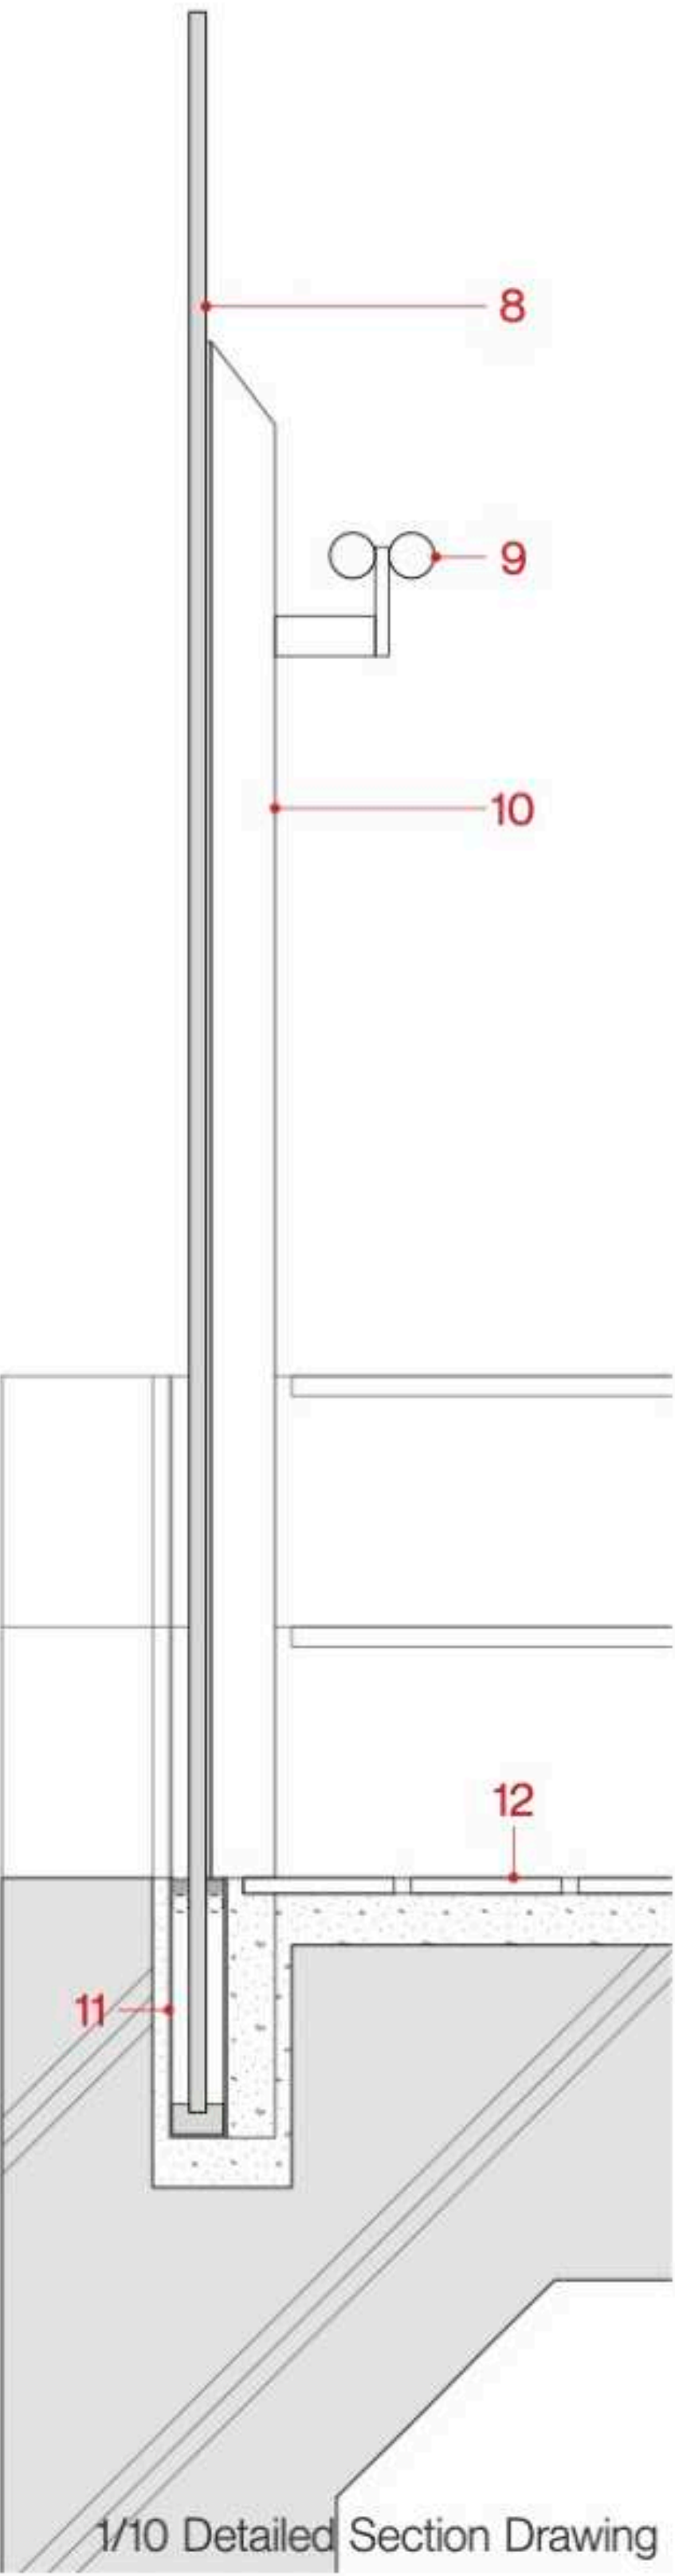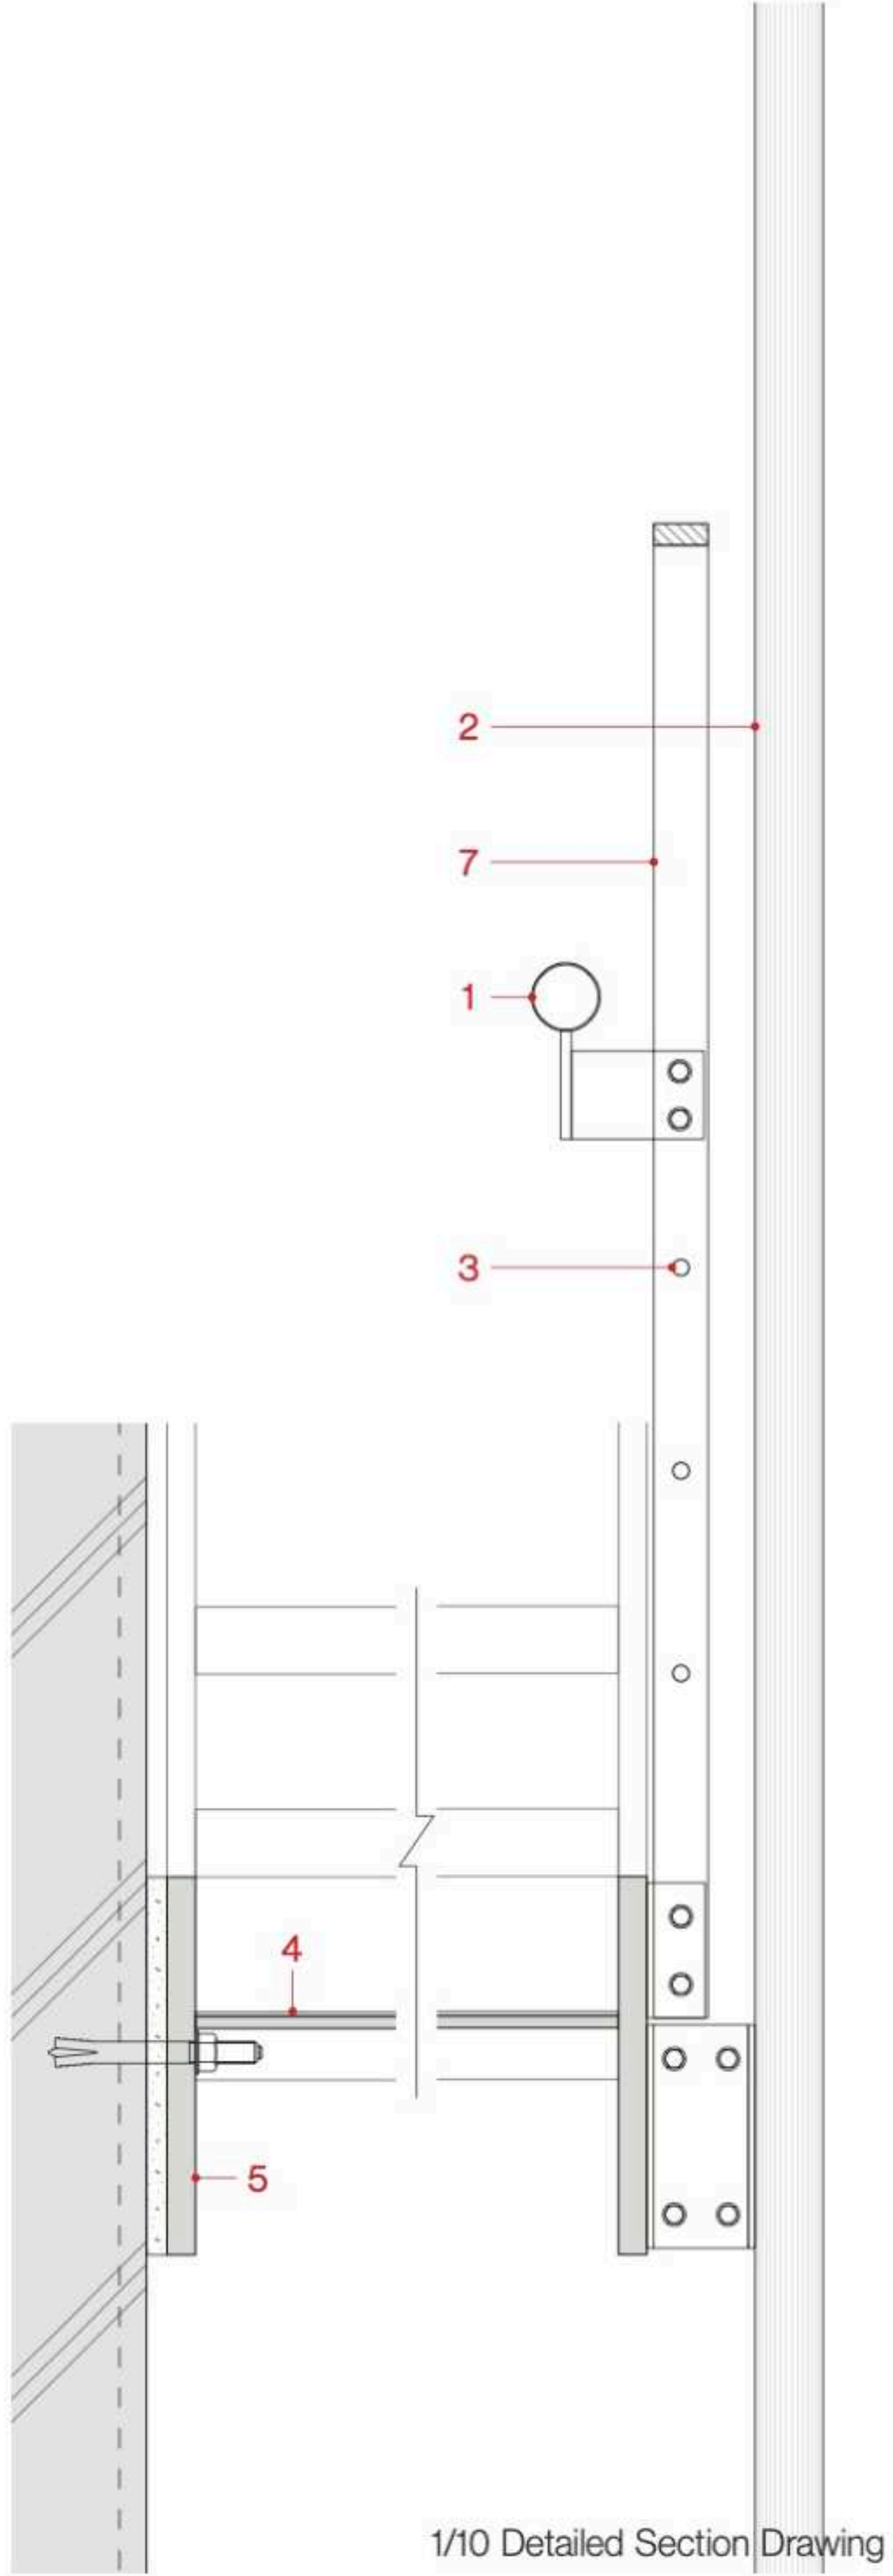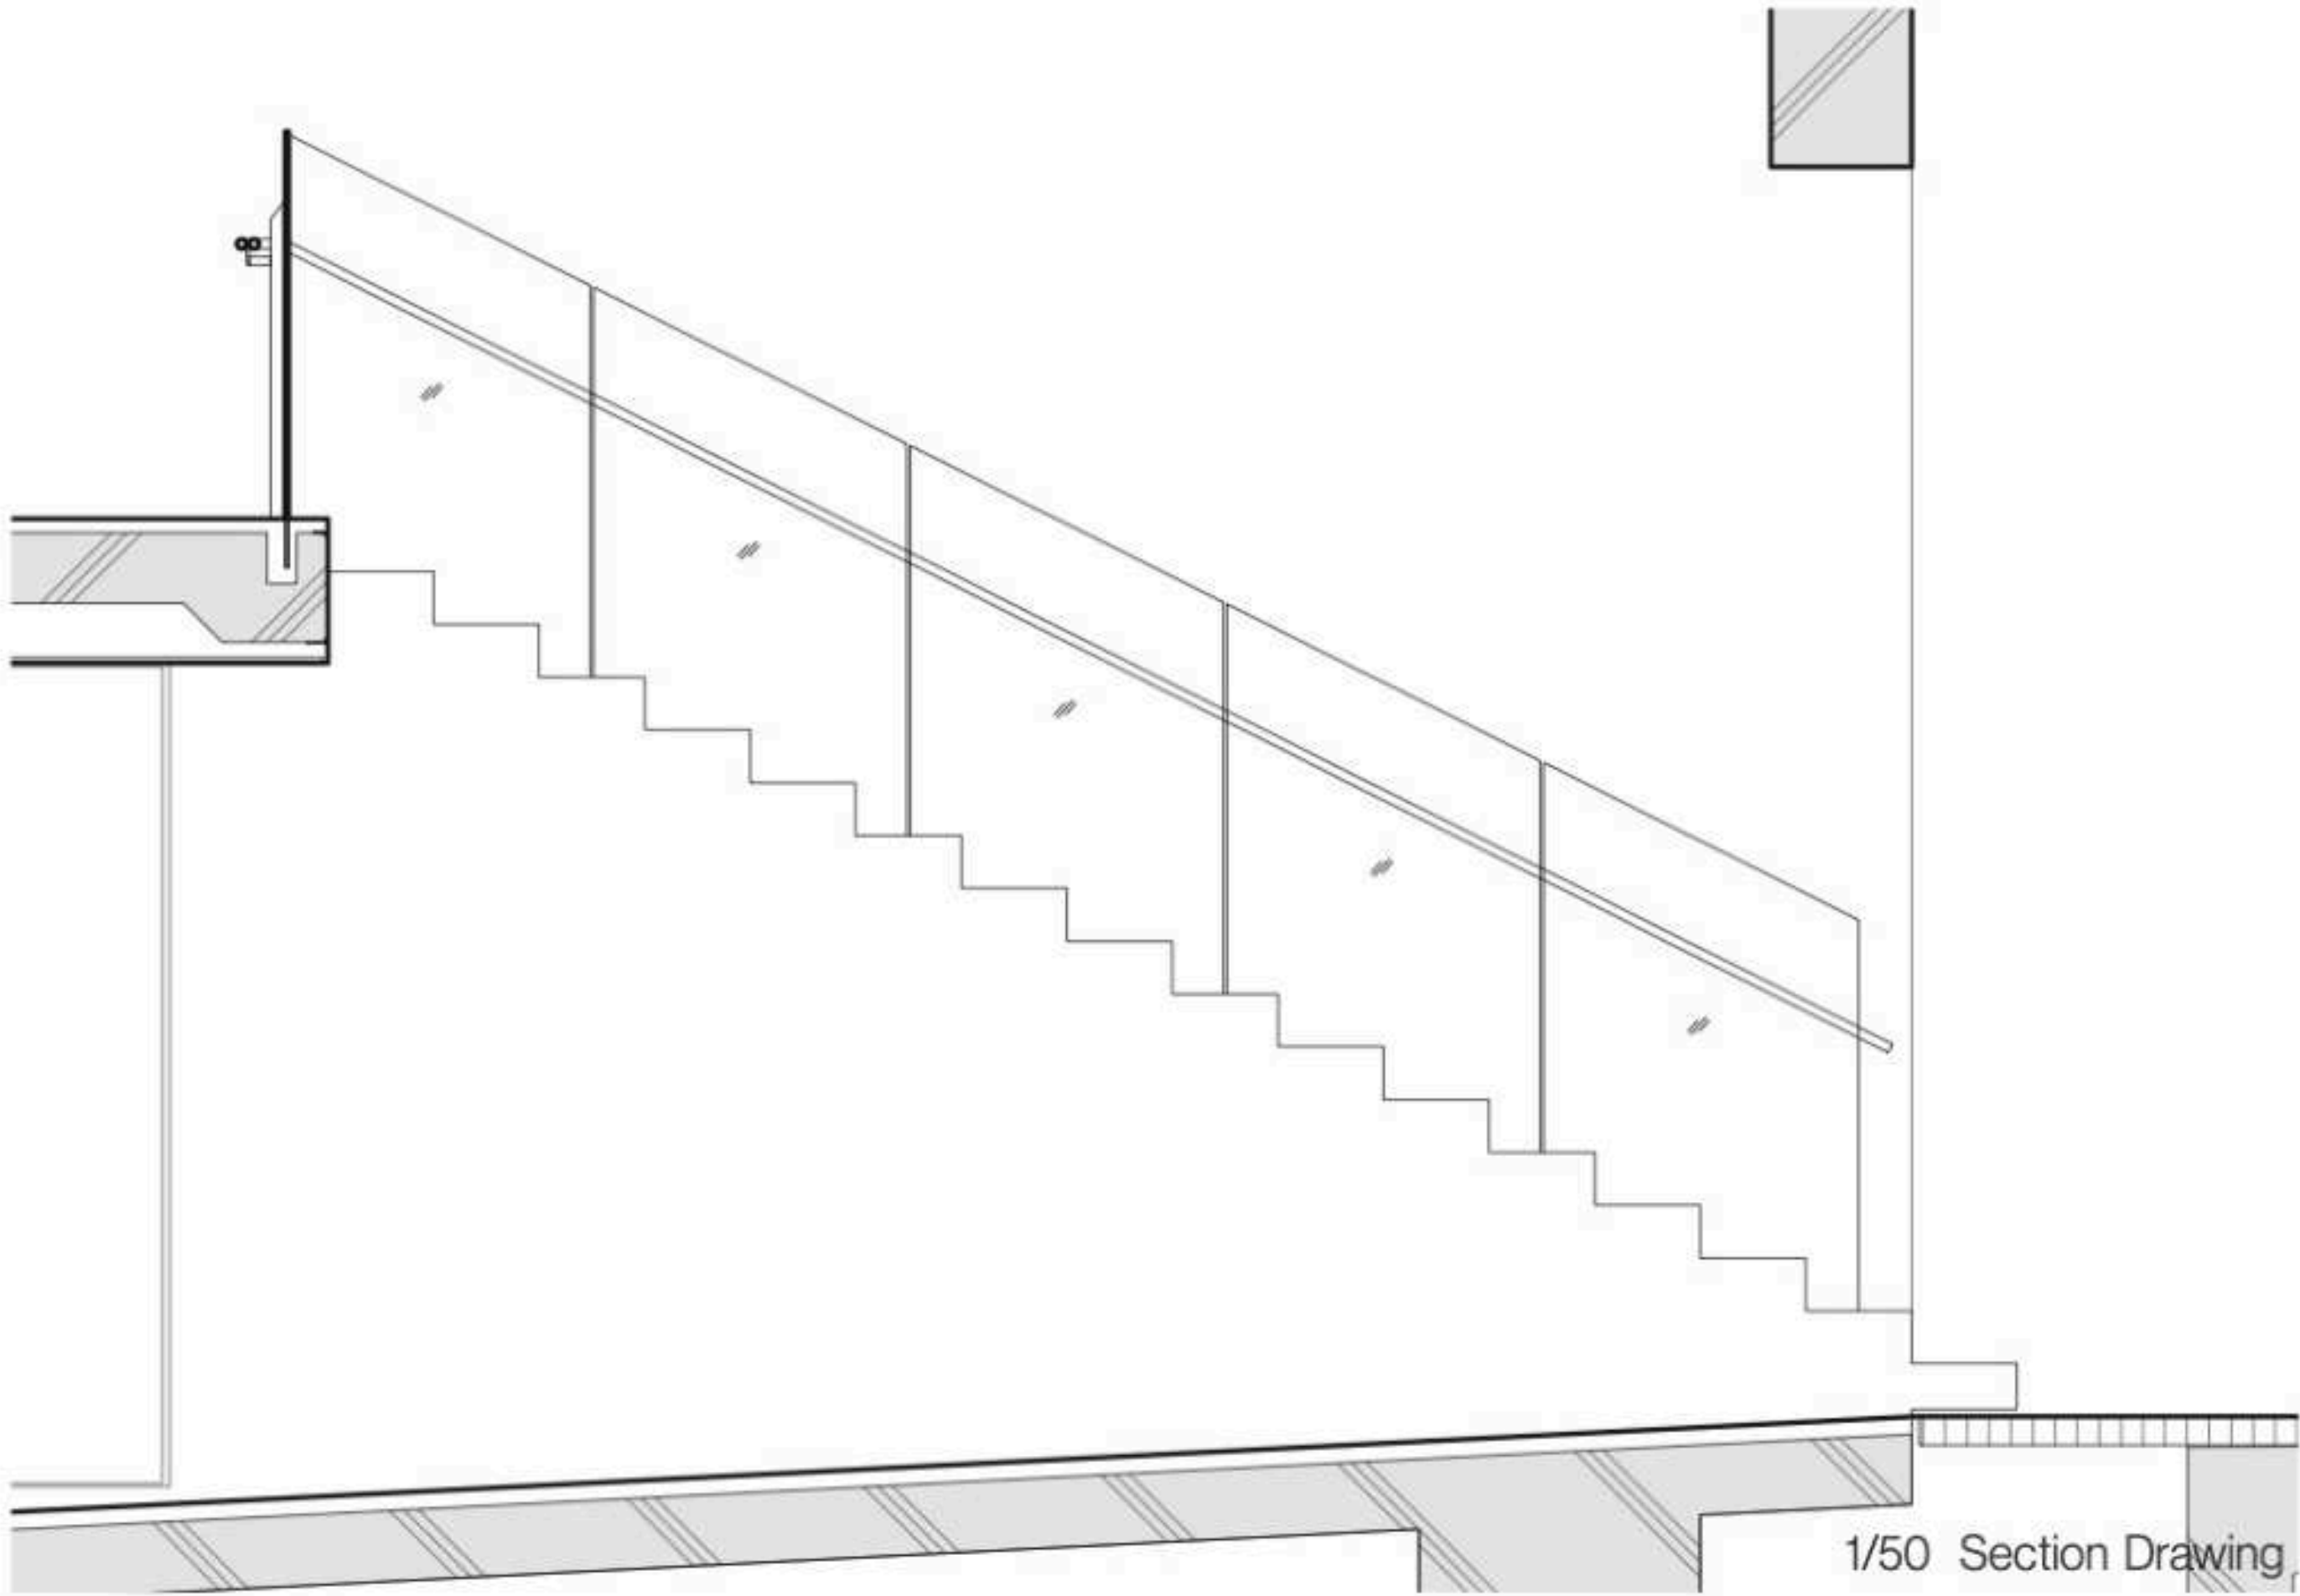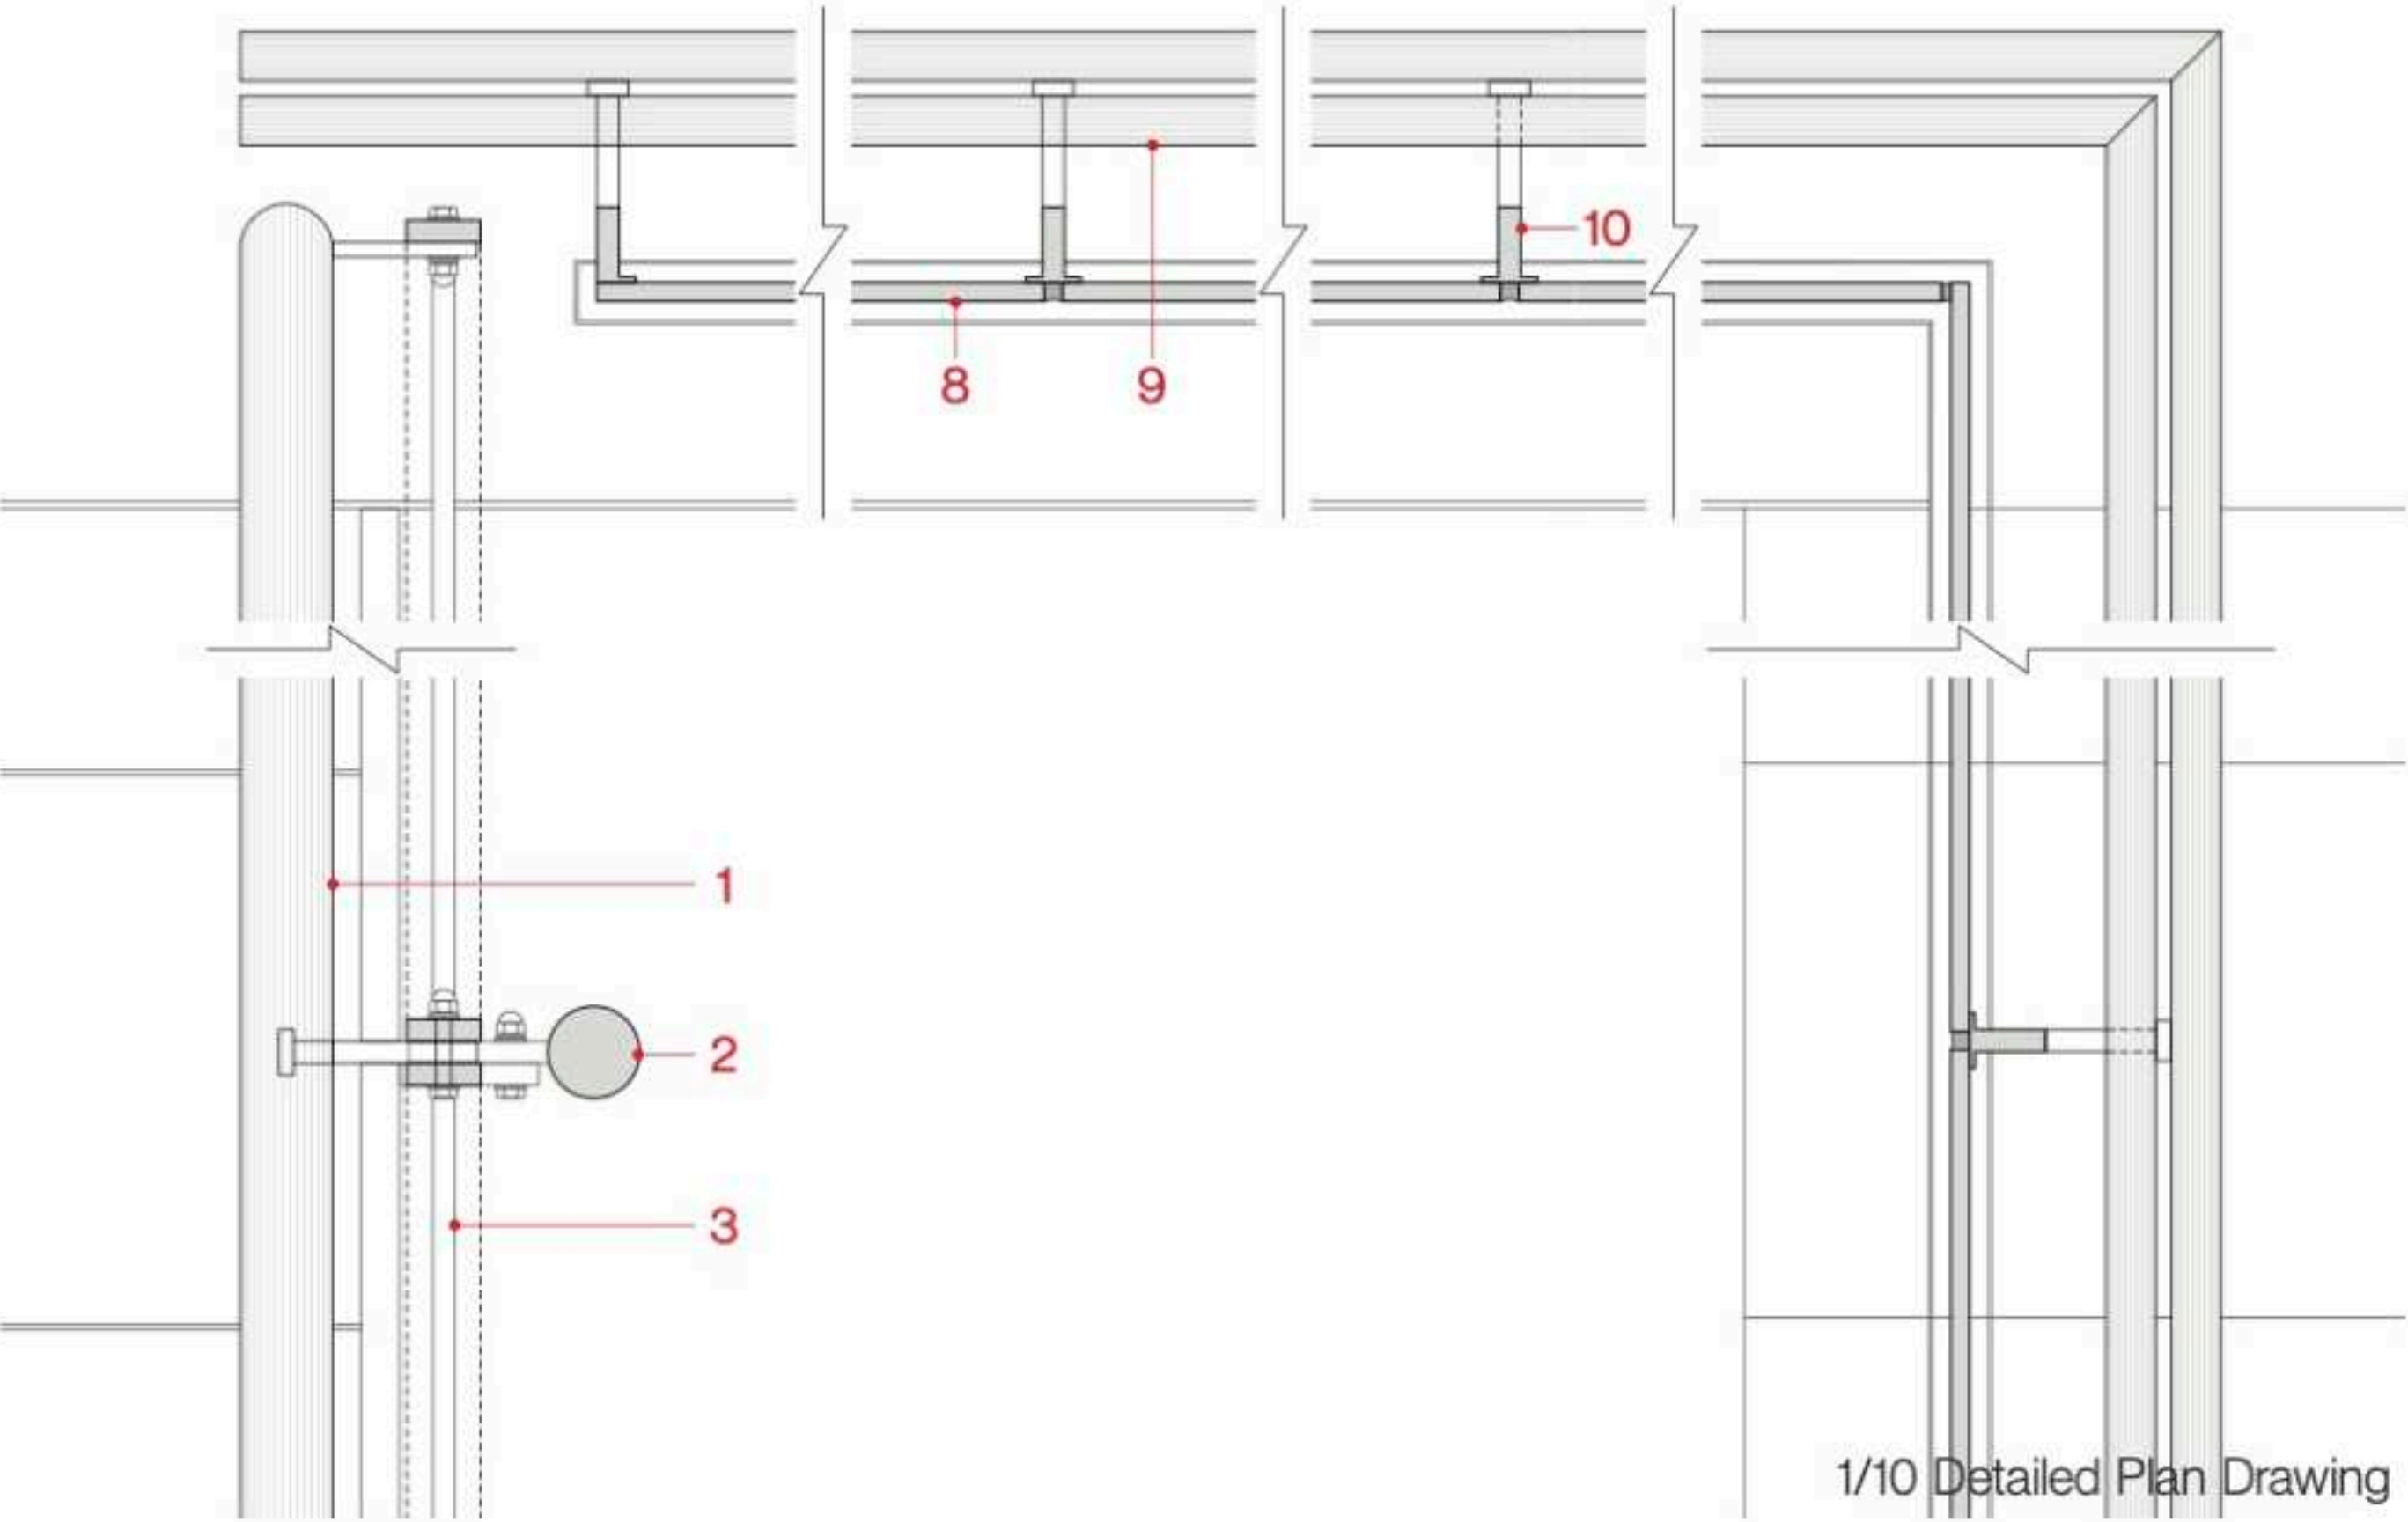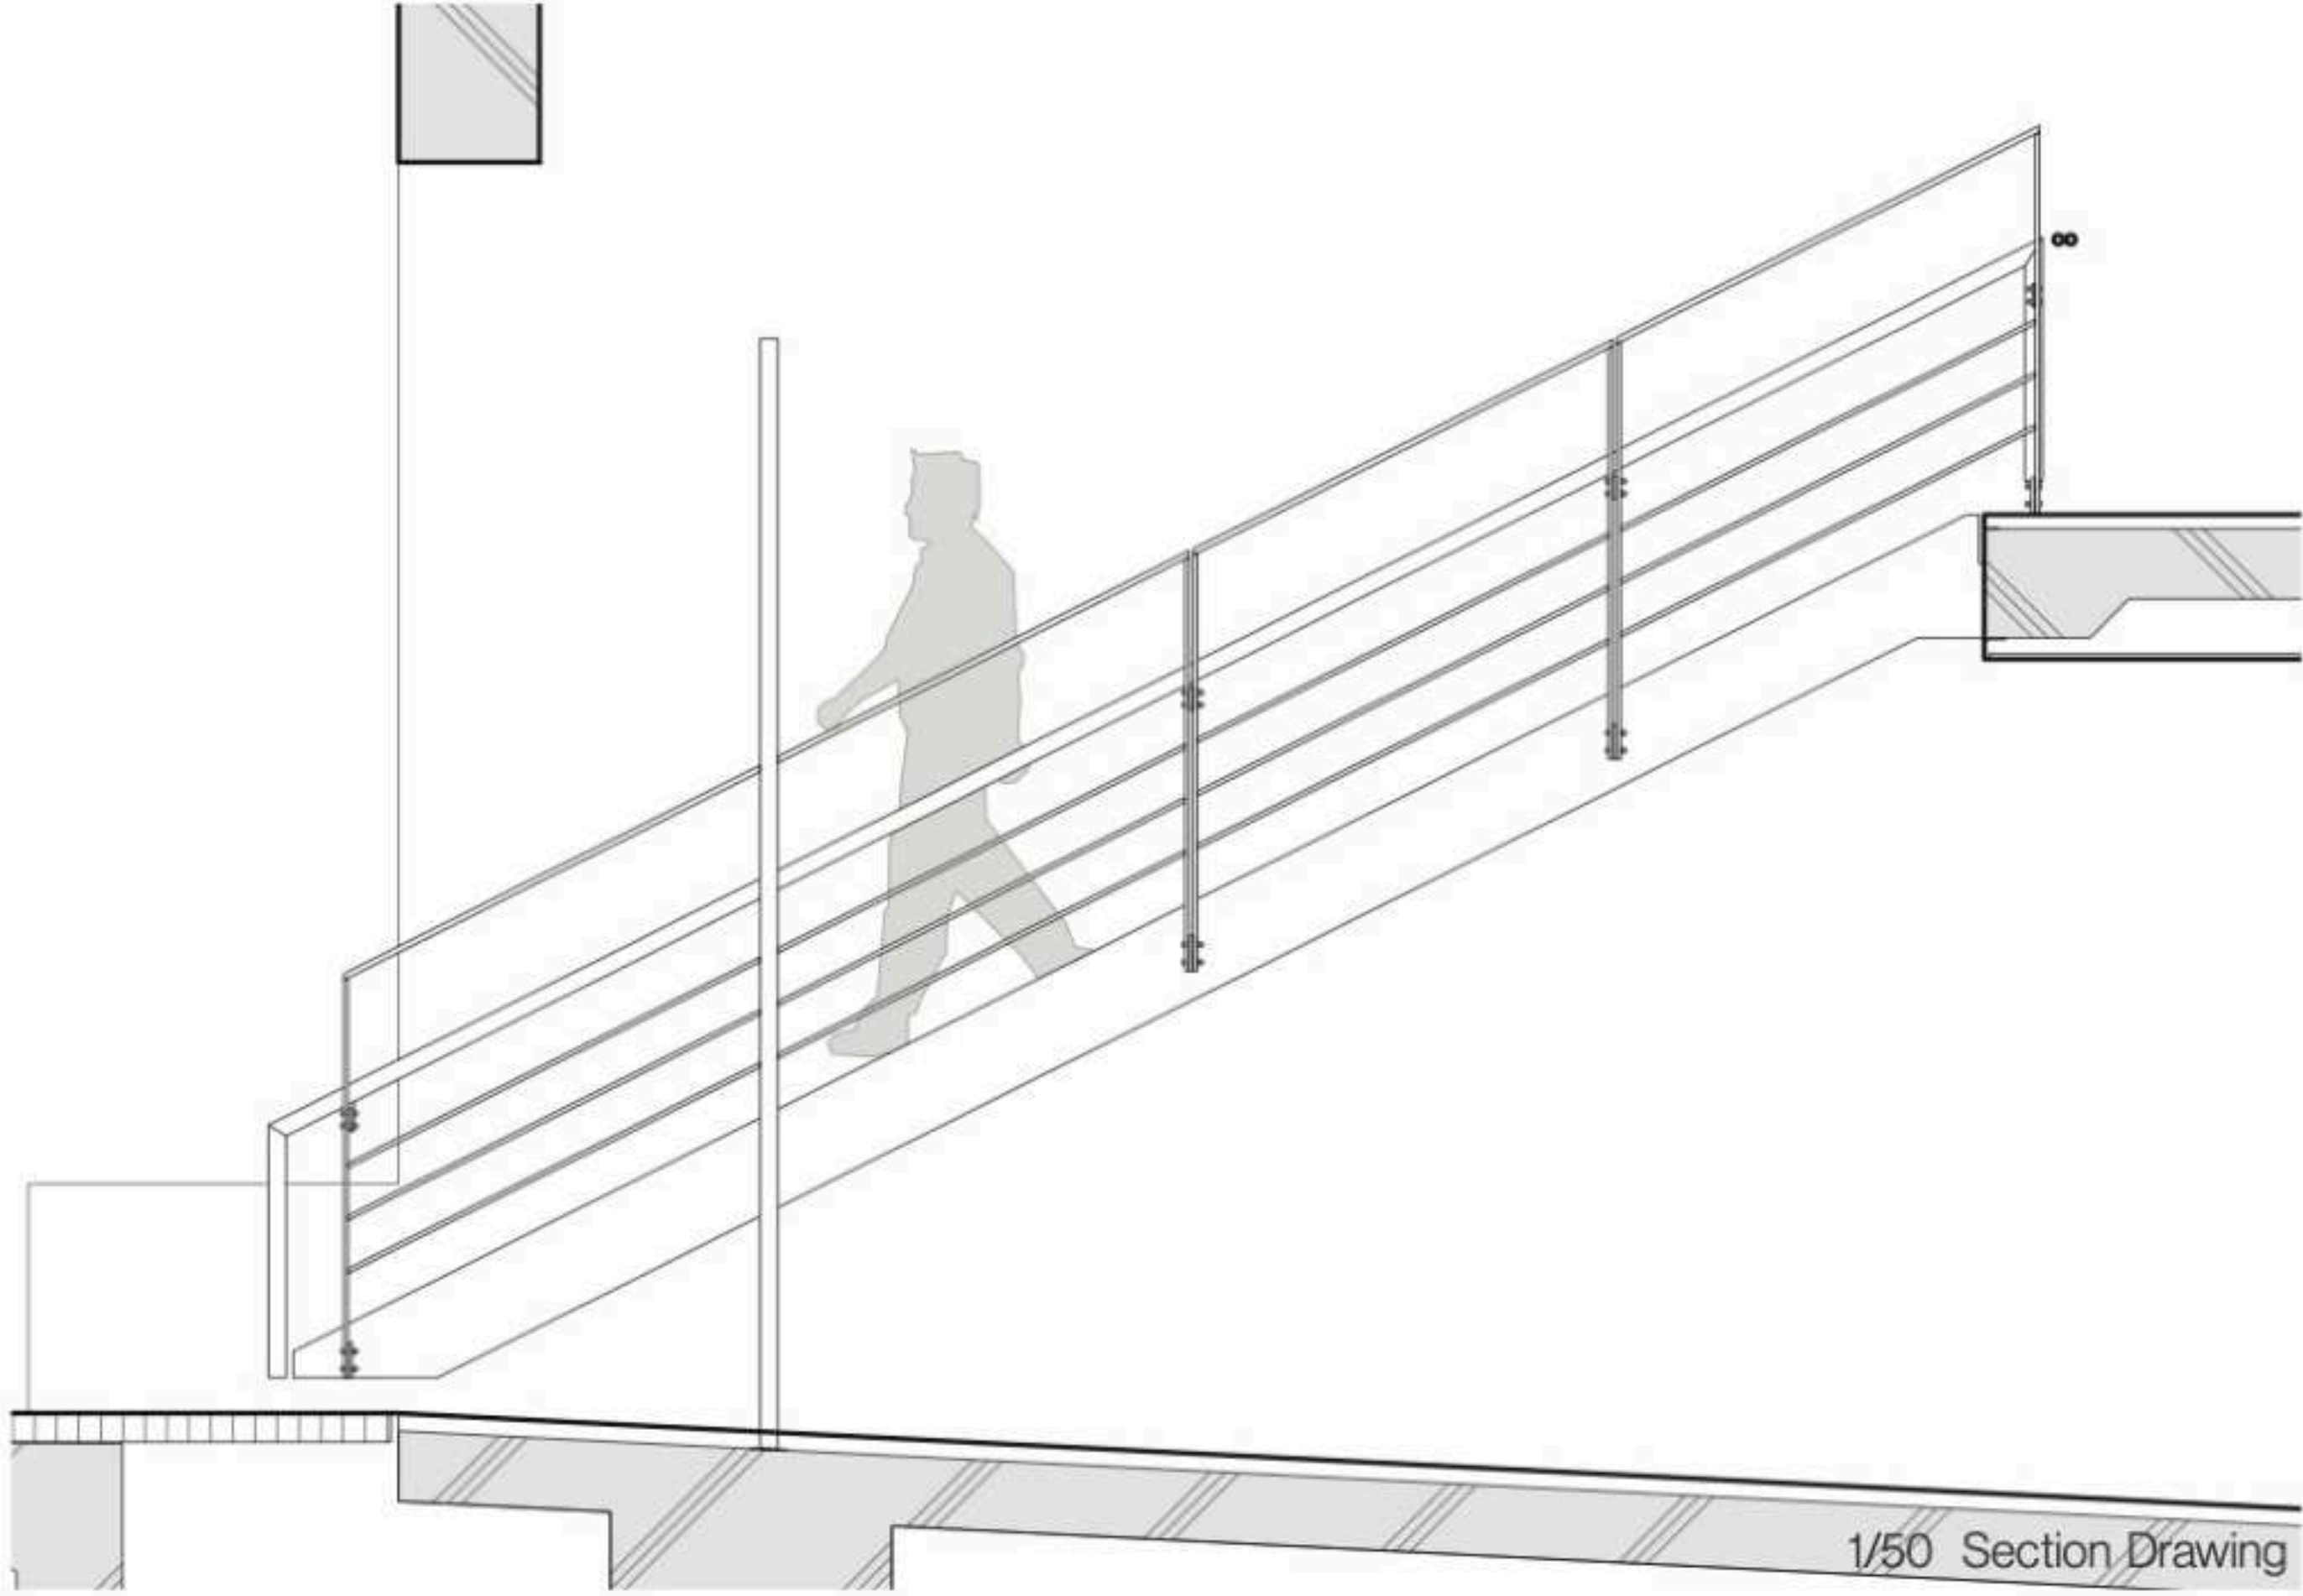

研究施設フロア




建物のコア部分と平面的に明確に分離された研究室側は、明快な RC 構造を有しており、内装においてもこの造形とコンセプトに調和するデザインを目指した。教授からの提案により、スケルトン天井と木製仕上げの間仕切り壁を採用している。

天井に関しては、唯一の仕上げと言える軽やかなパンチングメタルと、ライン照明を用いて空間の軸性を強めている。間仕切り壁に関しては、長期の利用に耐えるため、建具枠の見つけ寸法を 50mm とし、堅牢さを持たせた。また、掲示板としての利用も見込んで、壁仕上げは有孔板としている。


Laboratory

The laboratory wing, which is clearly separated in plan from the building's core, possesses a straightforward RC structure, and the interior design was developed to harmonise with this formal logic and the overall concept. At the suggestion of the professor in charge, a skeleton ceiling and timber-finished partition walls were adopted.

For the ceiling, lightweight perforated metal panels — the sole applied finish — and linear lighting are employed together to reinforce the axial quality of the space. For the partition walls, a frame reveal depth of 50 mm was specified to impart both robustness and refinement, ensuring durability over long-term use. The wall surface finish is perforated board, anticipating its use as a pinboard.

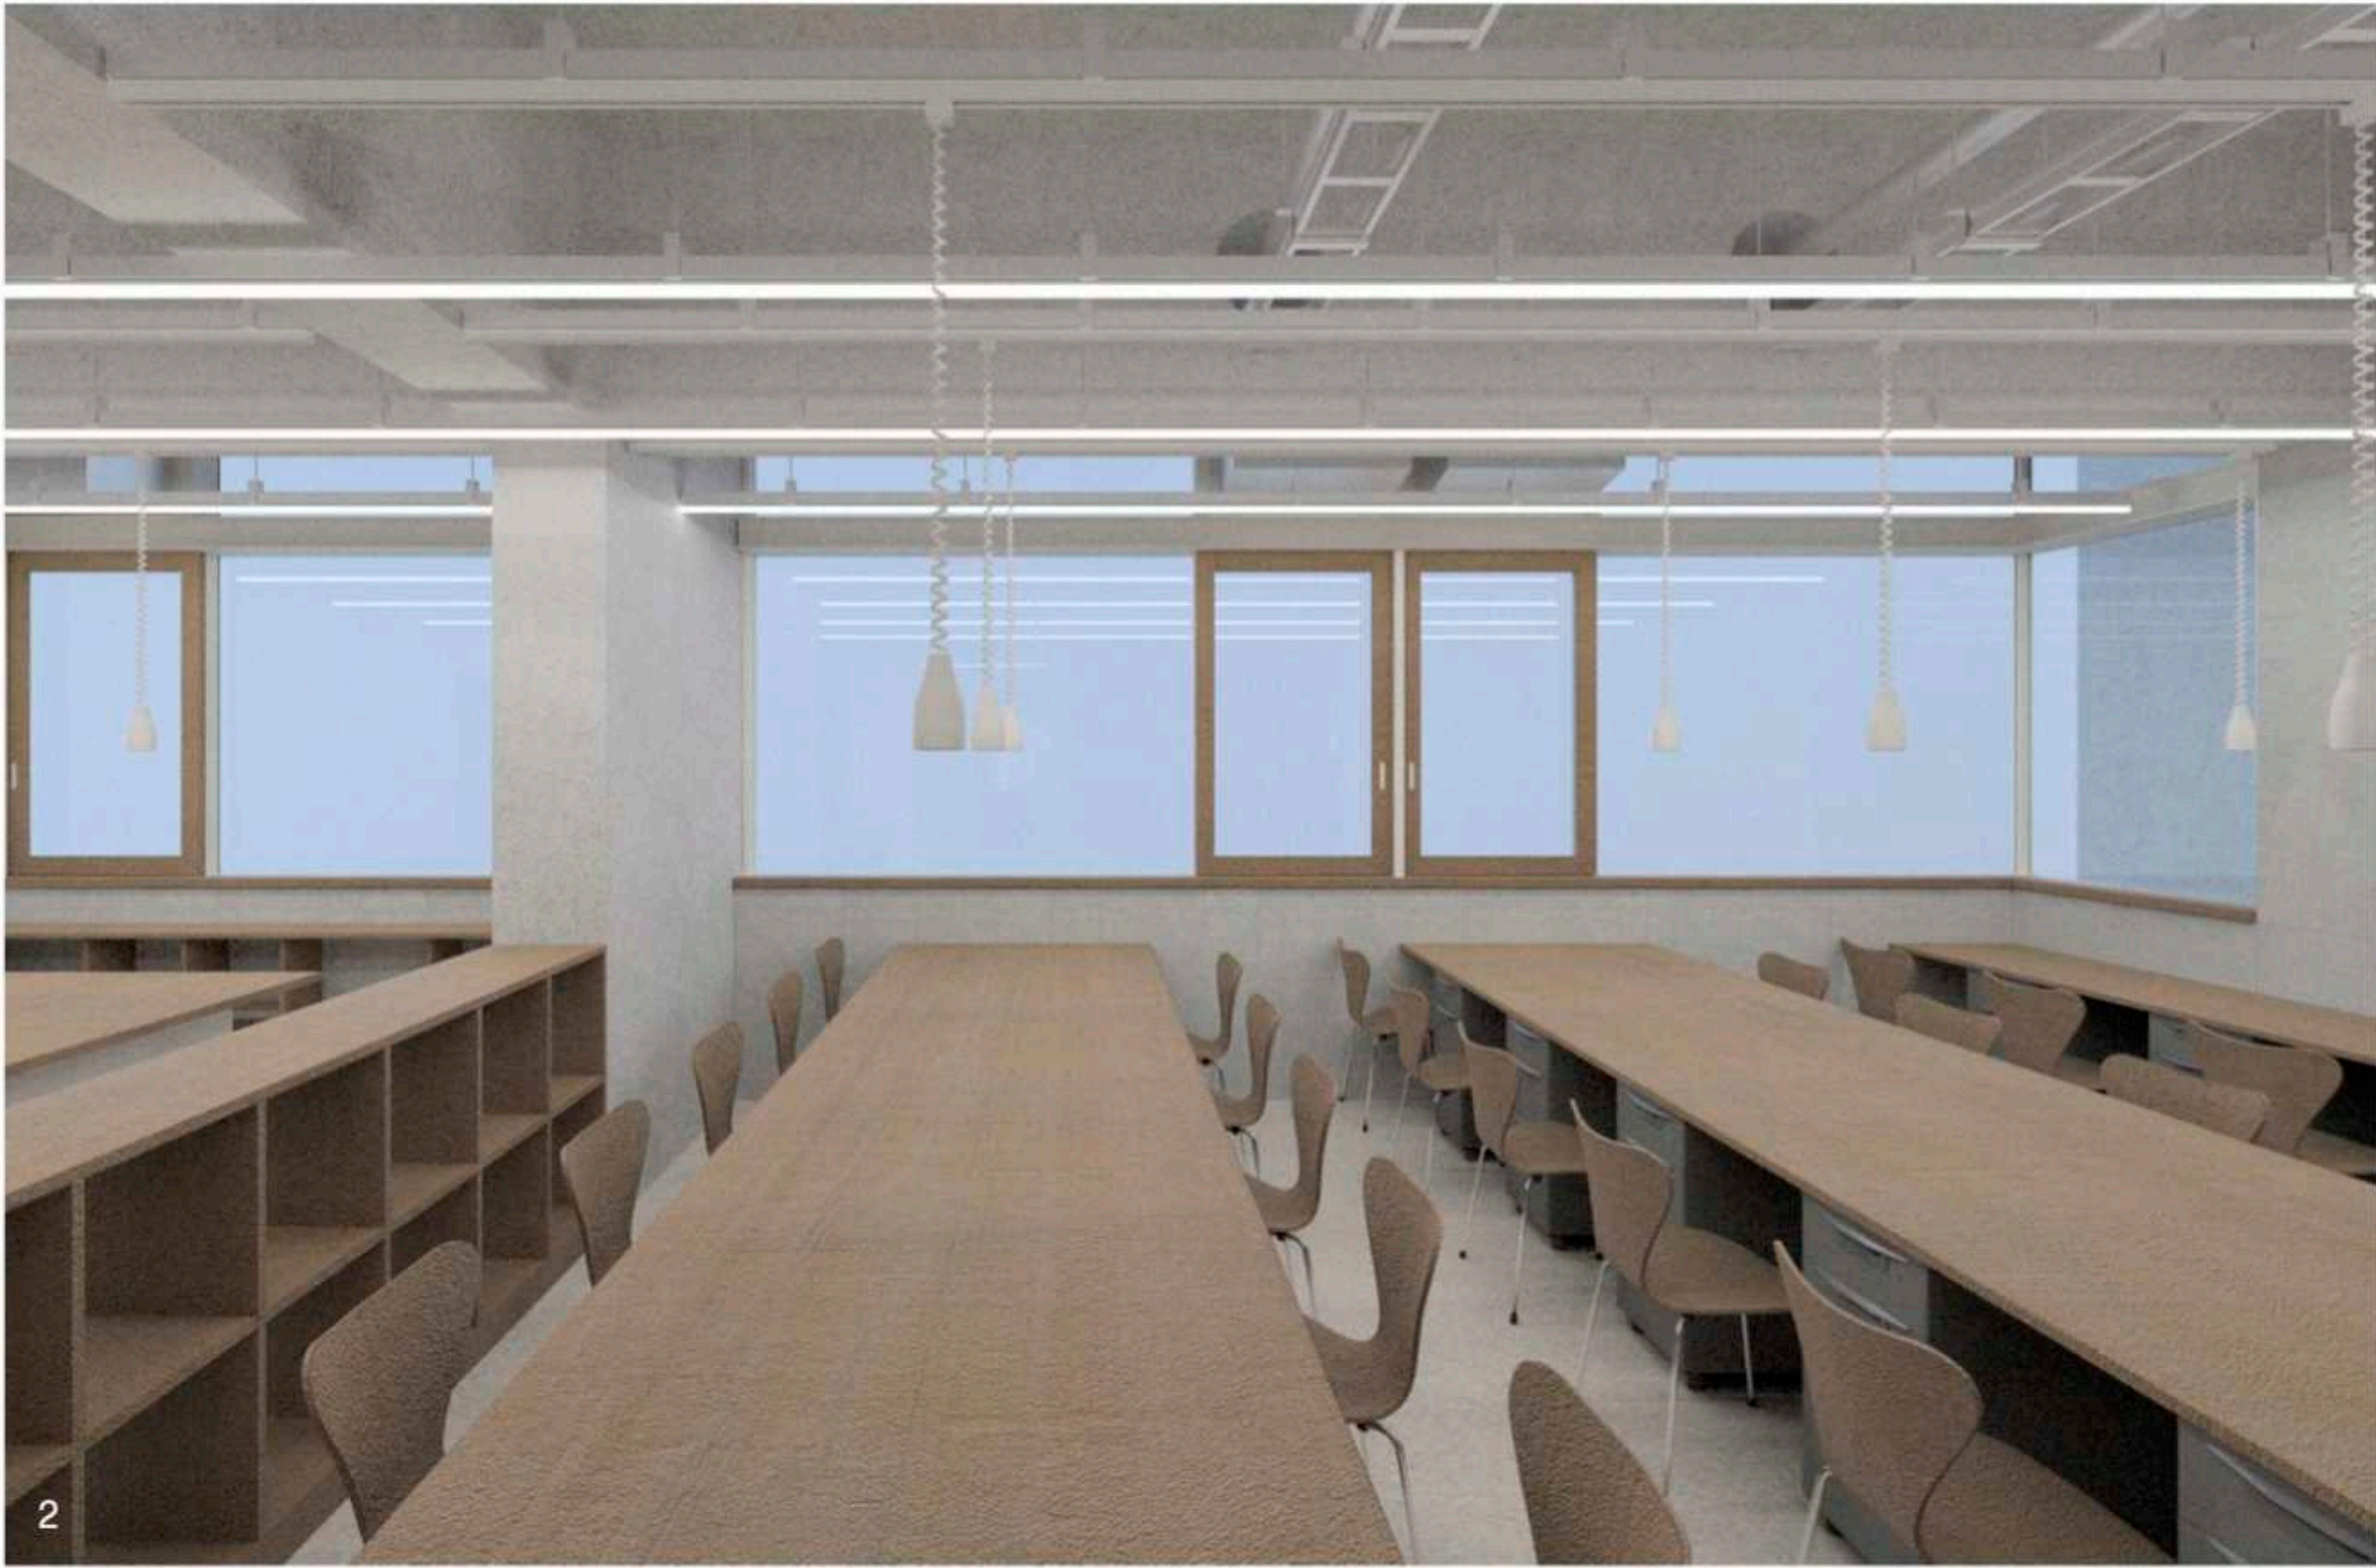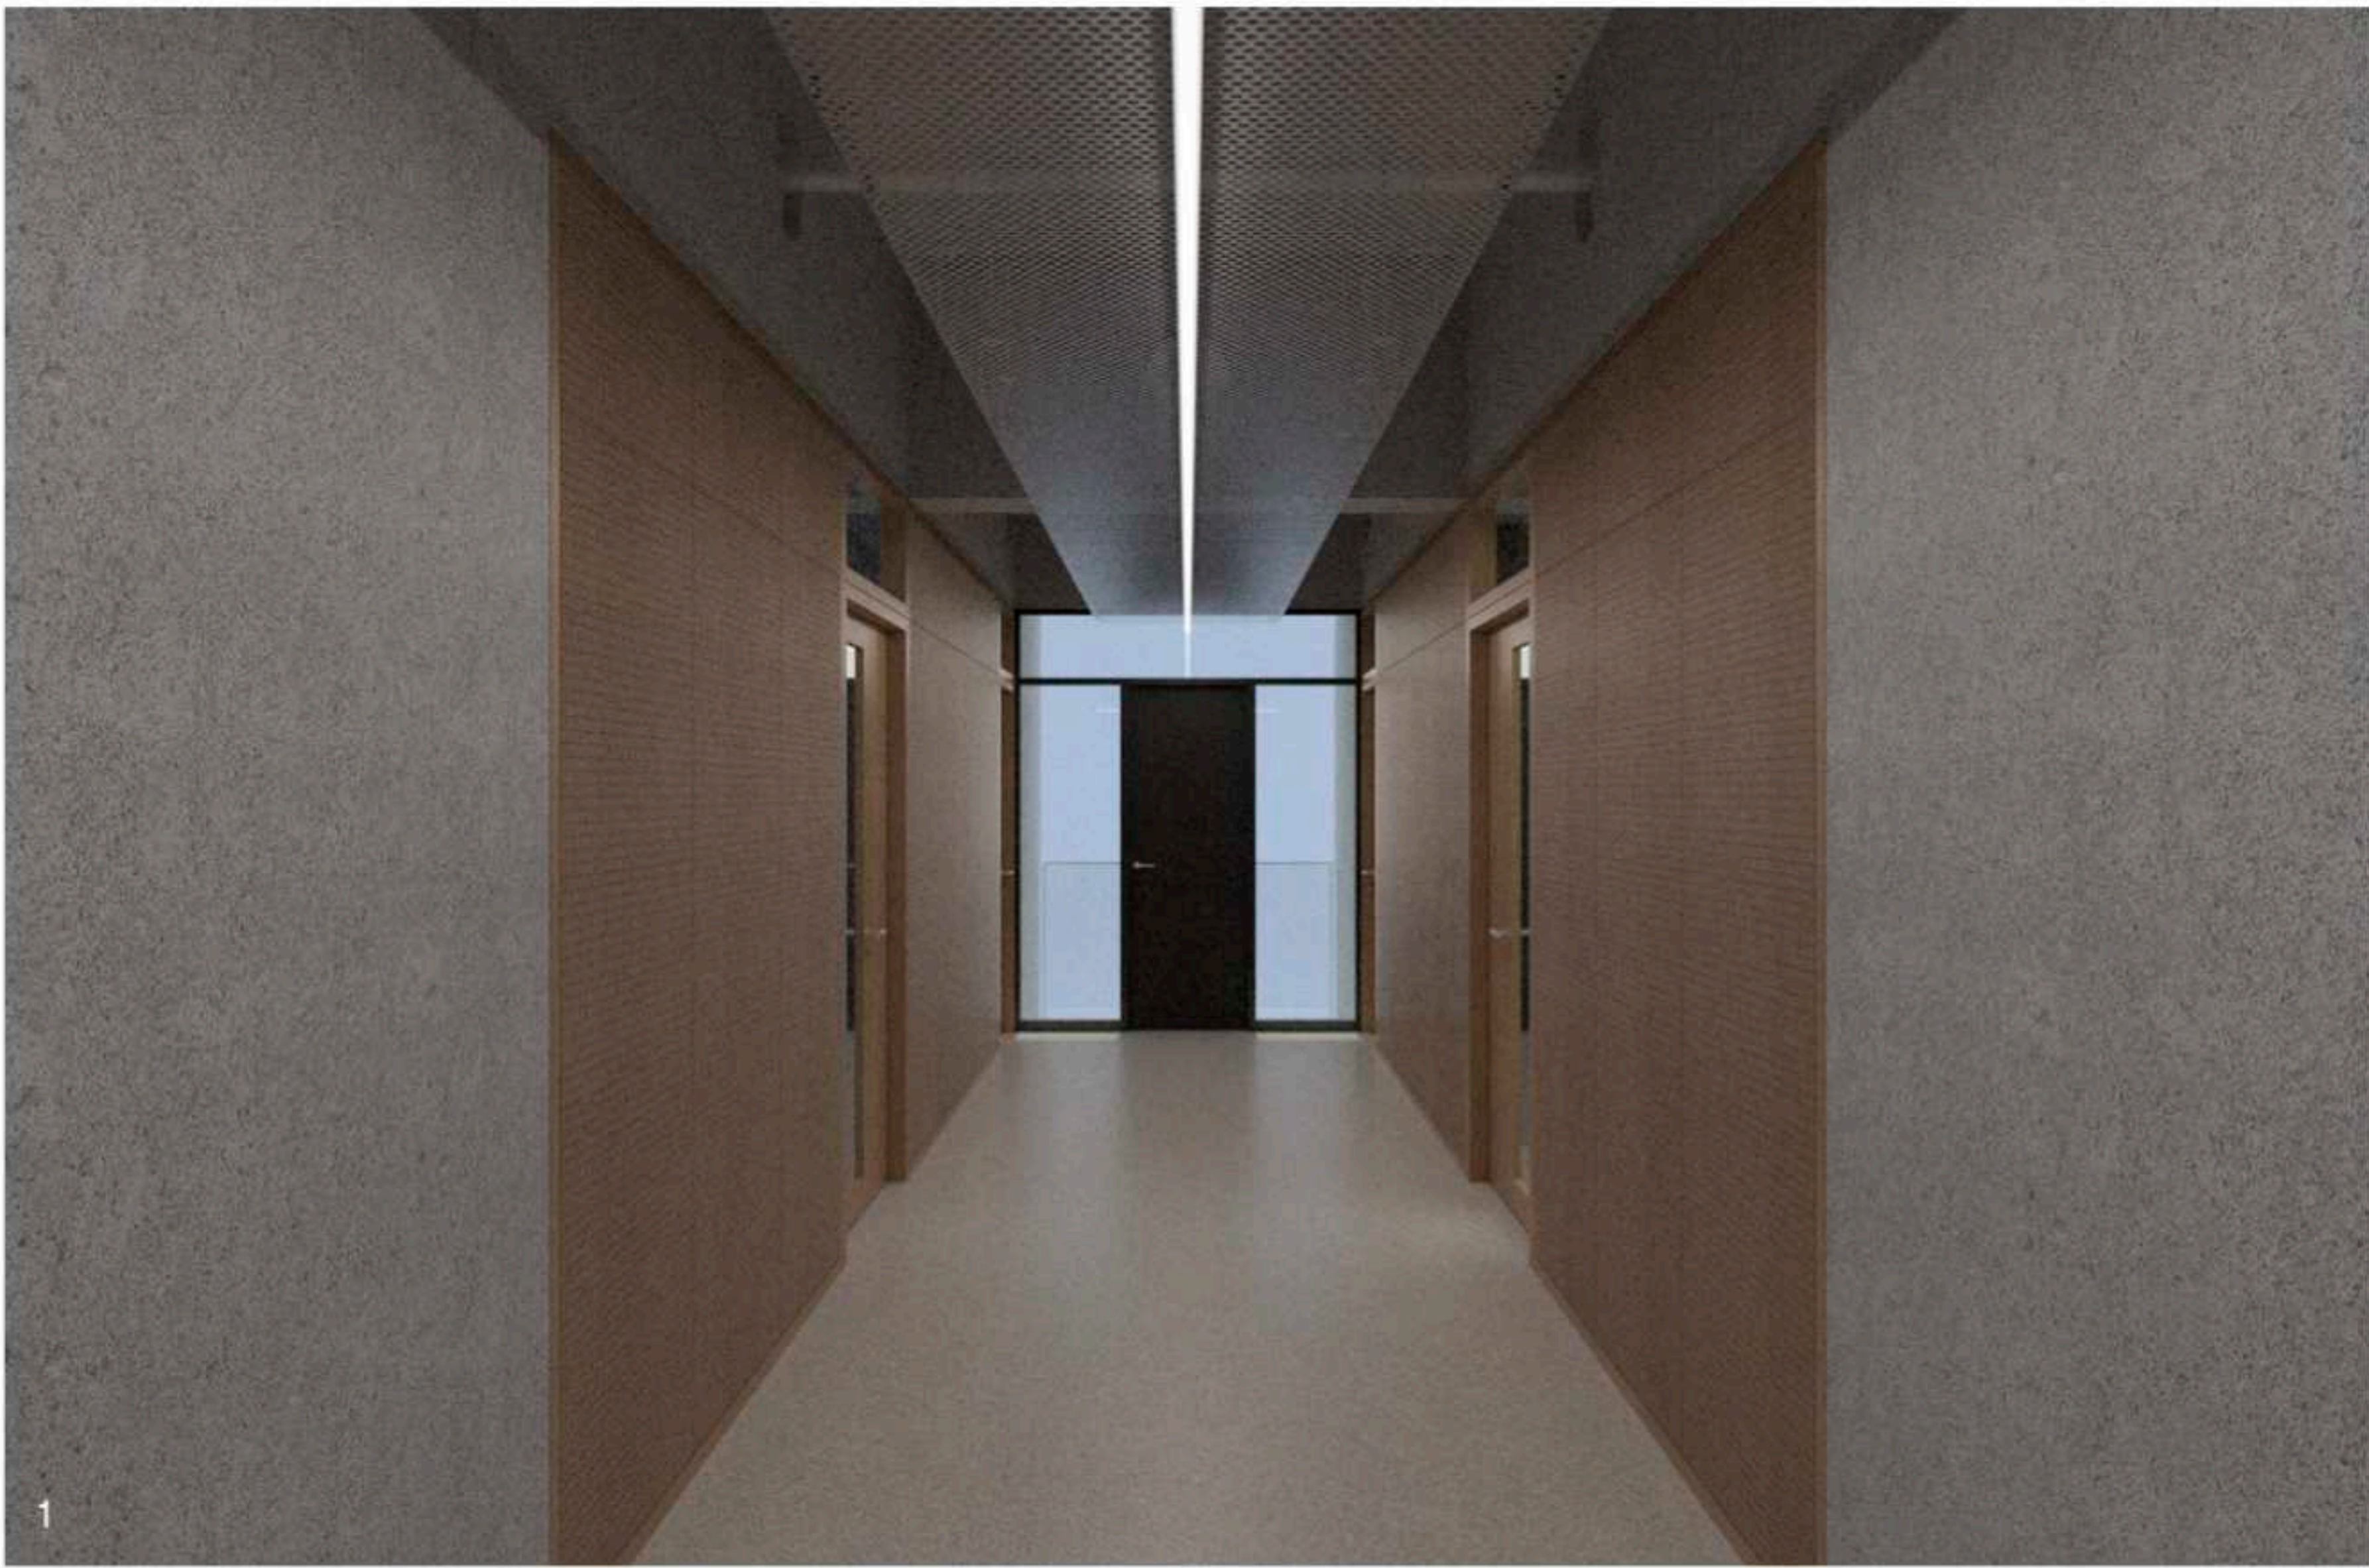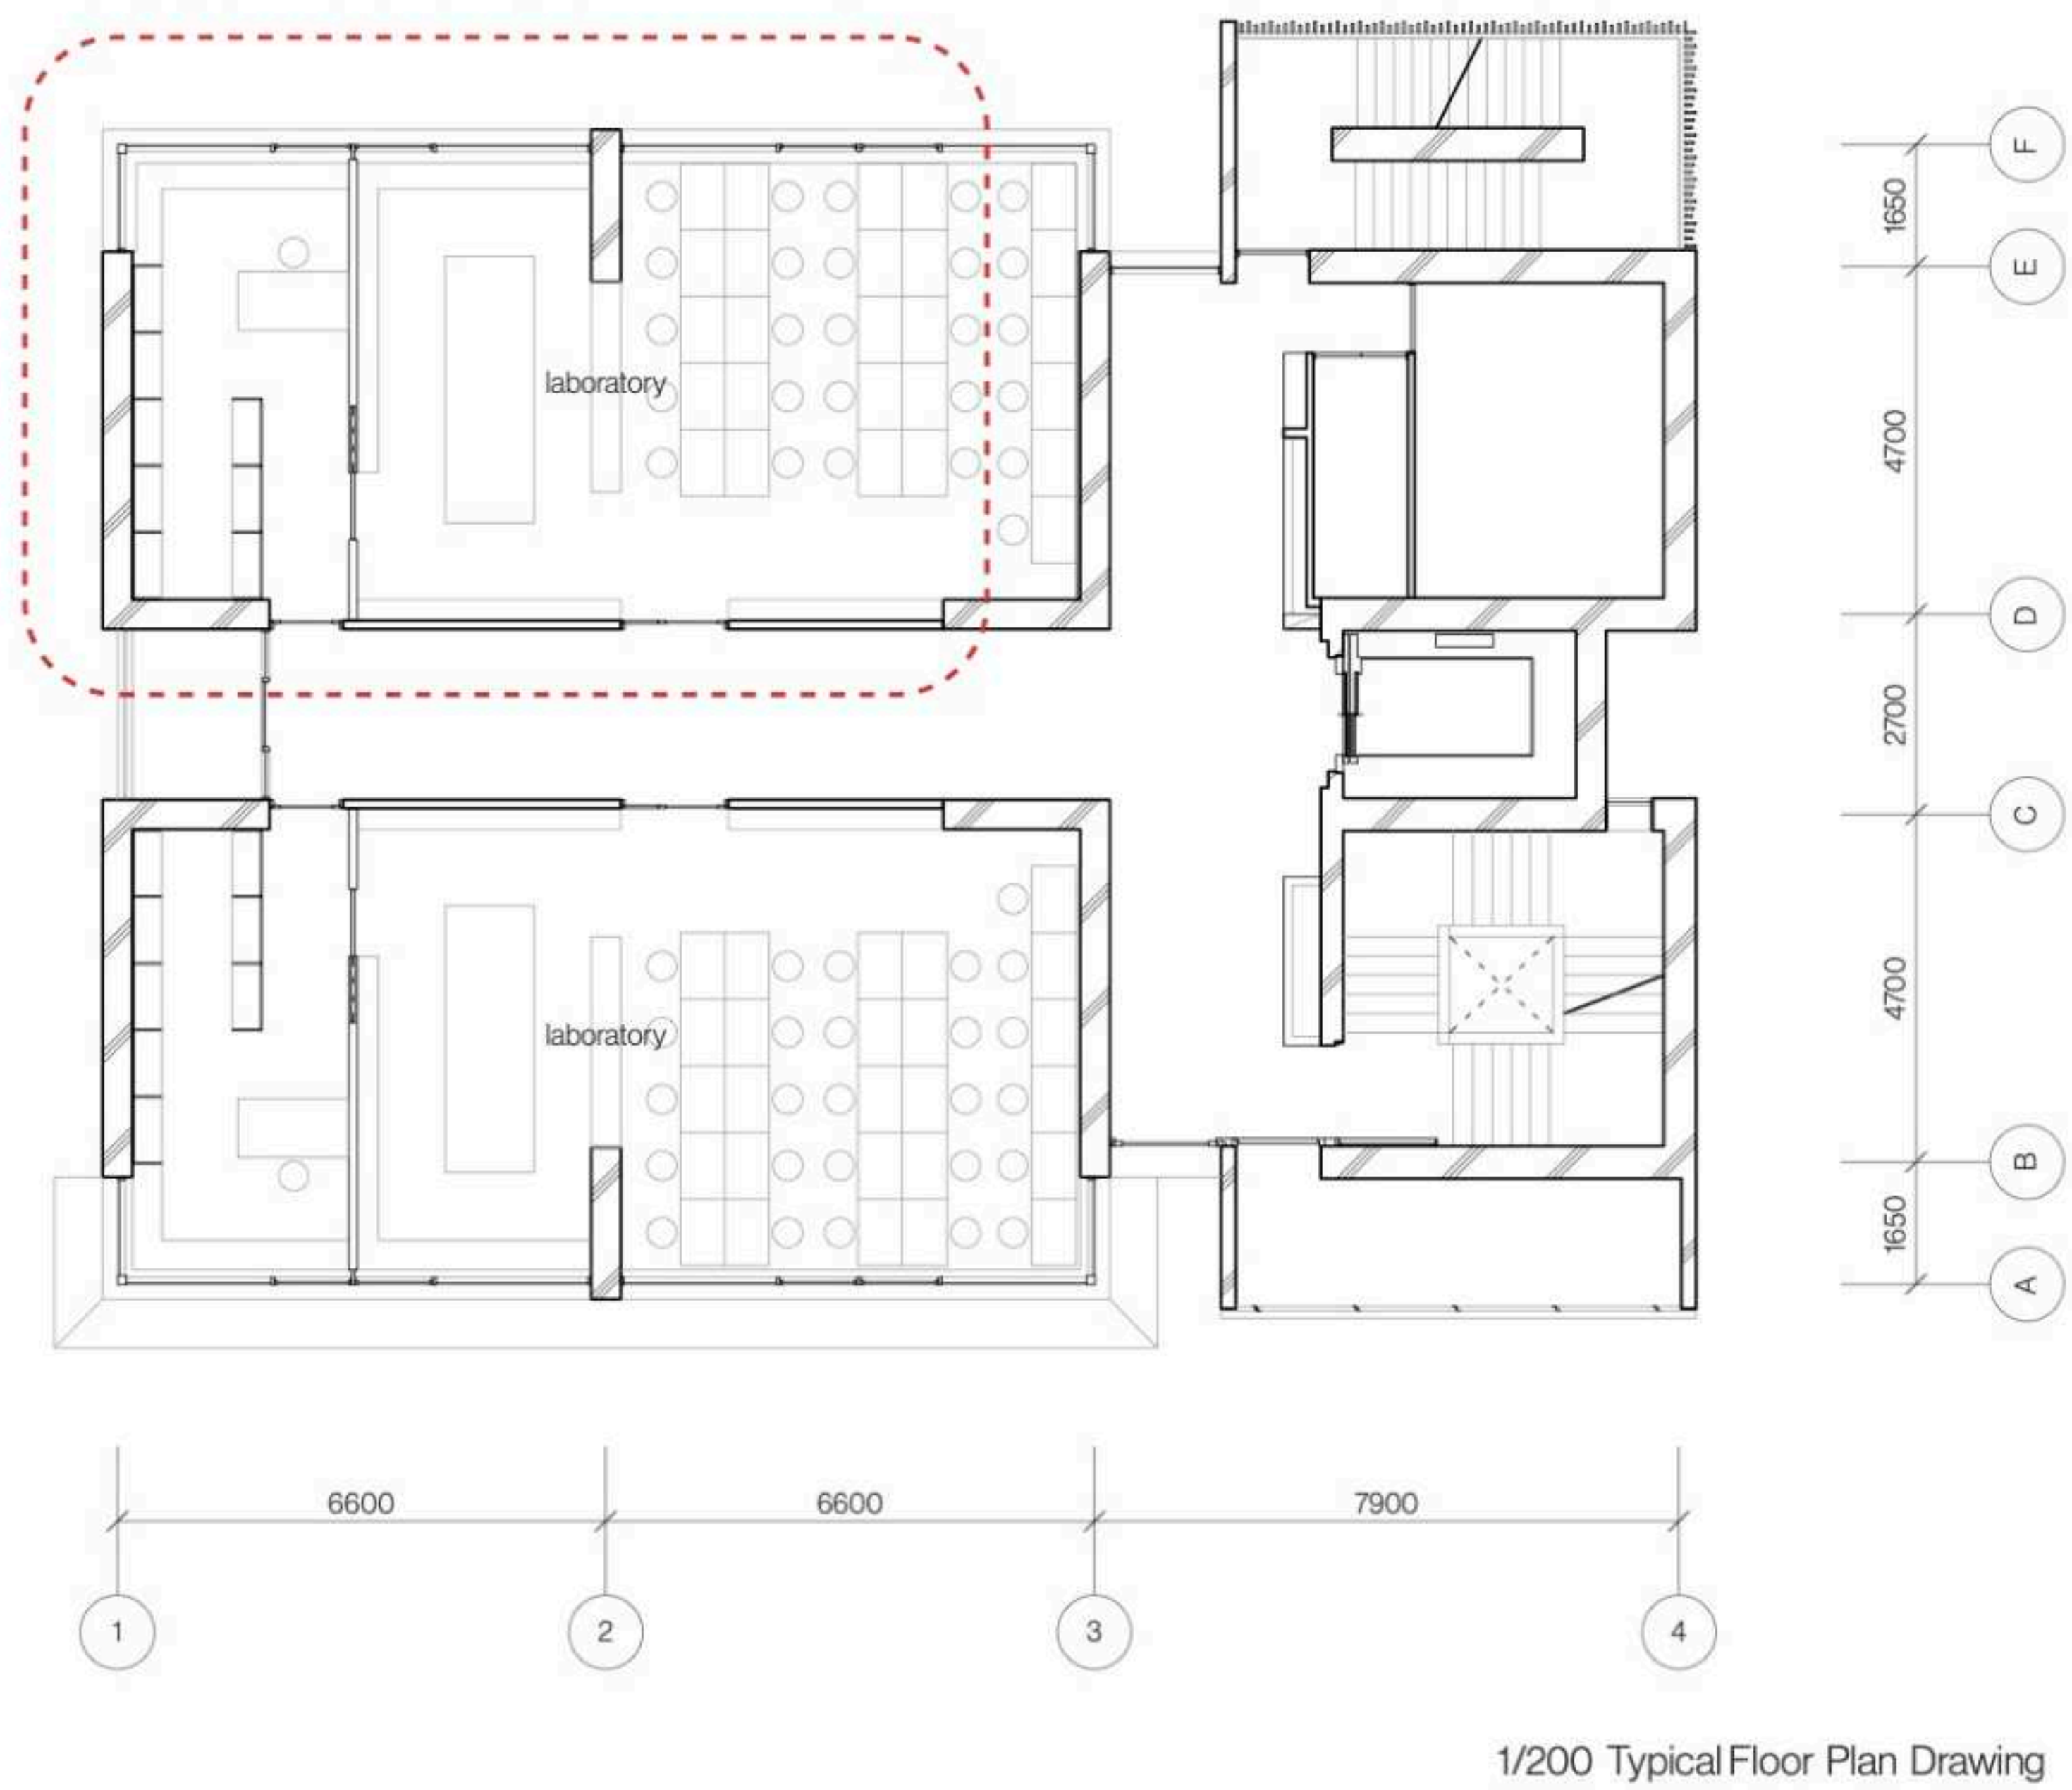

1. Corridor in front of the laboratory
2. Inside the laboratory

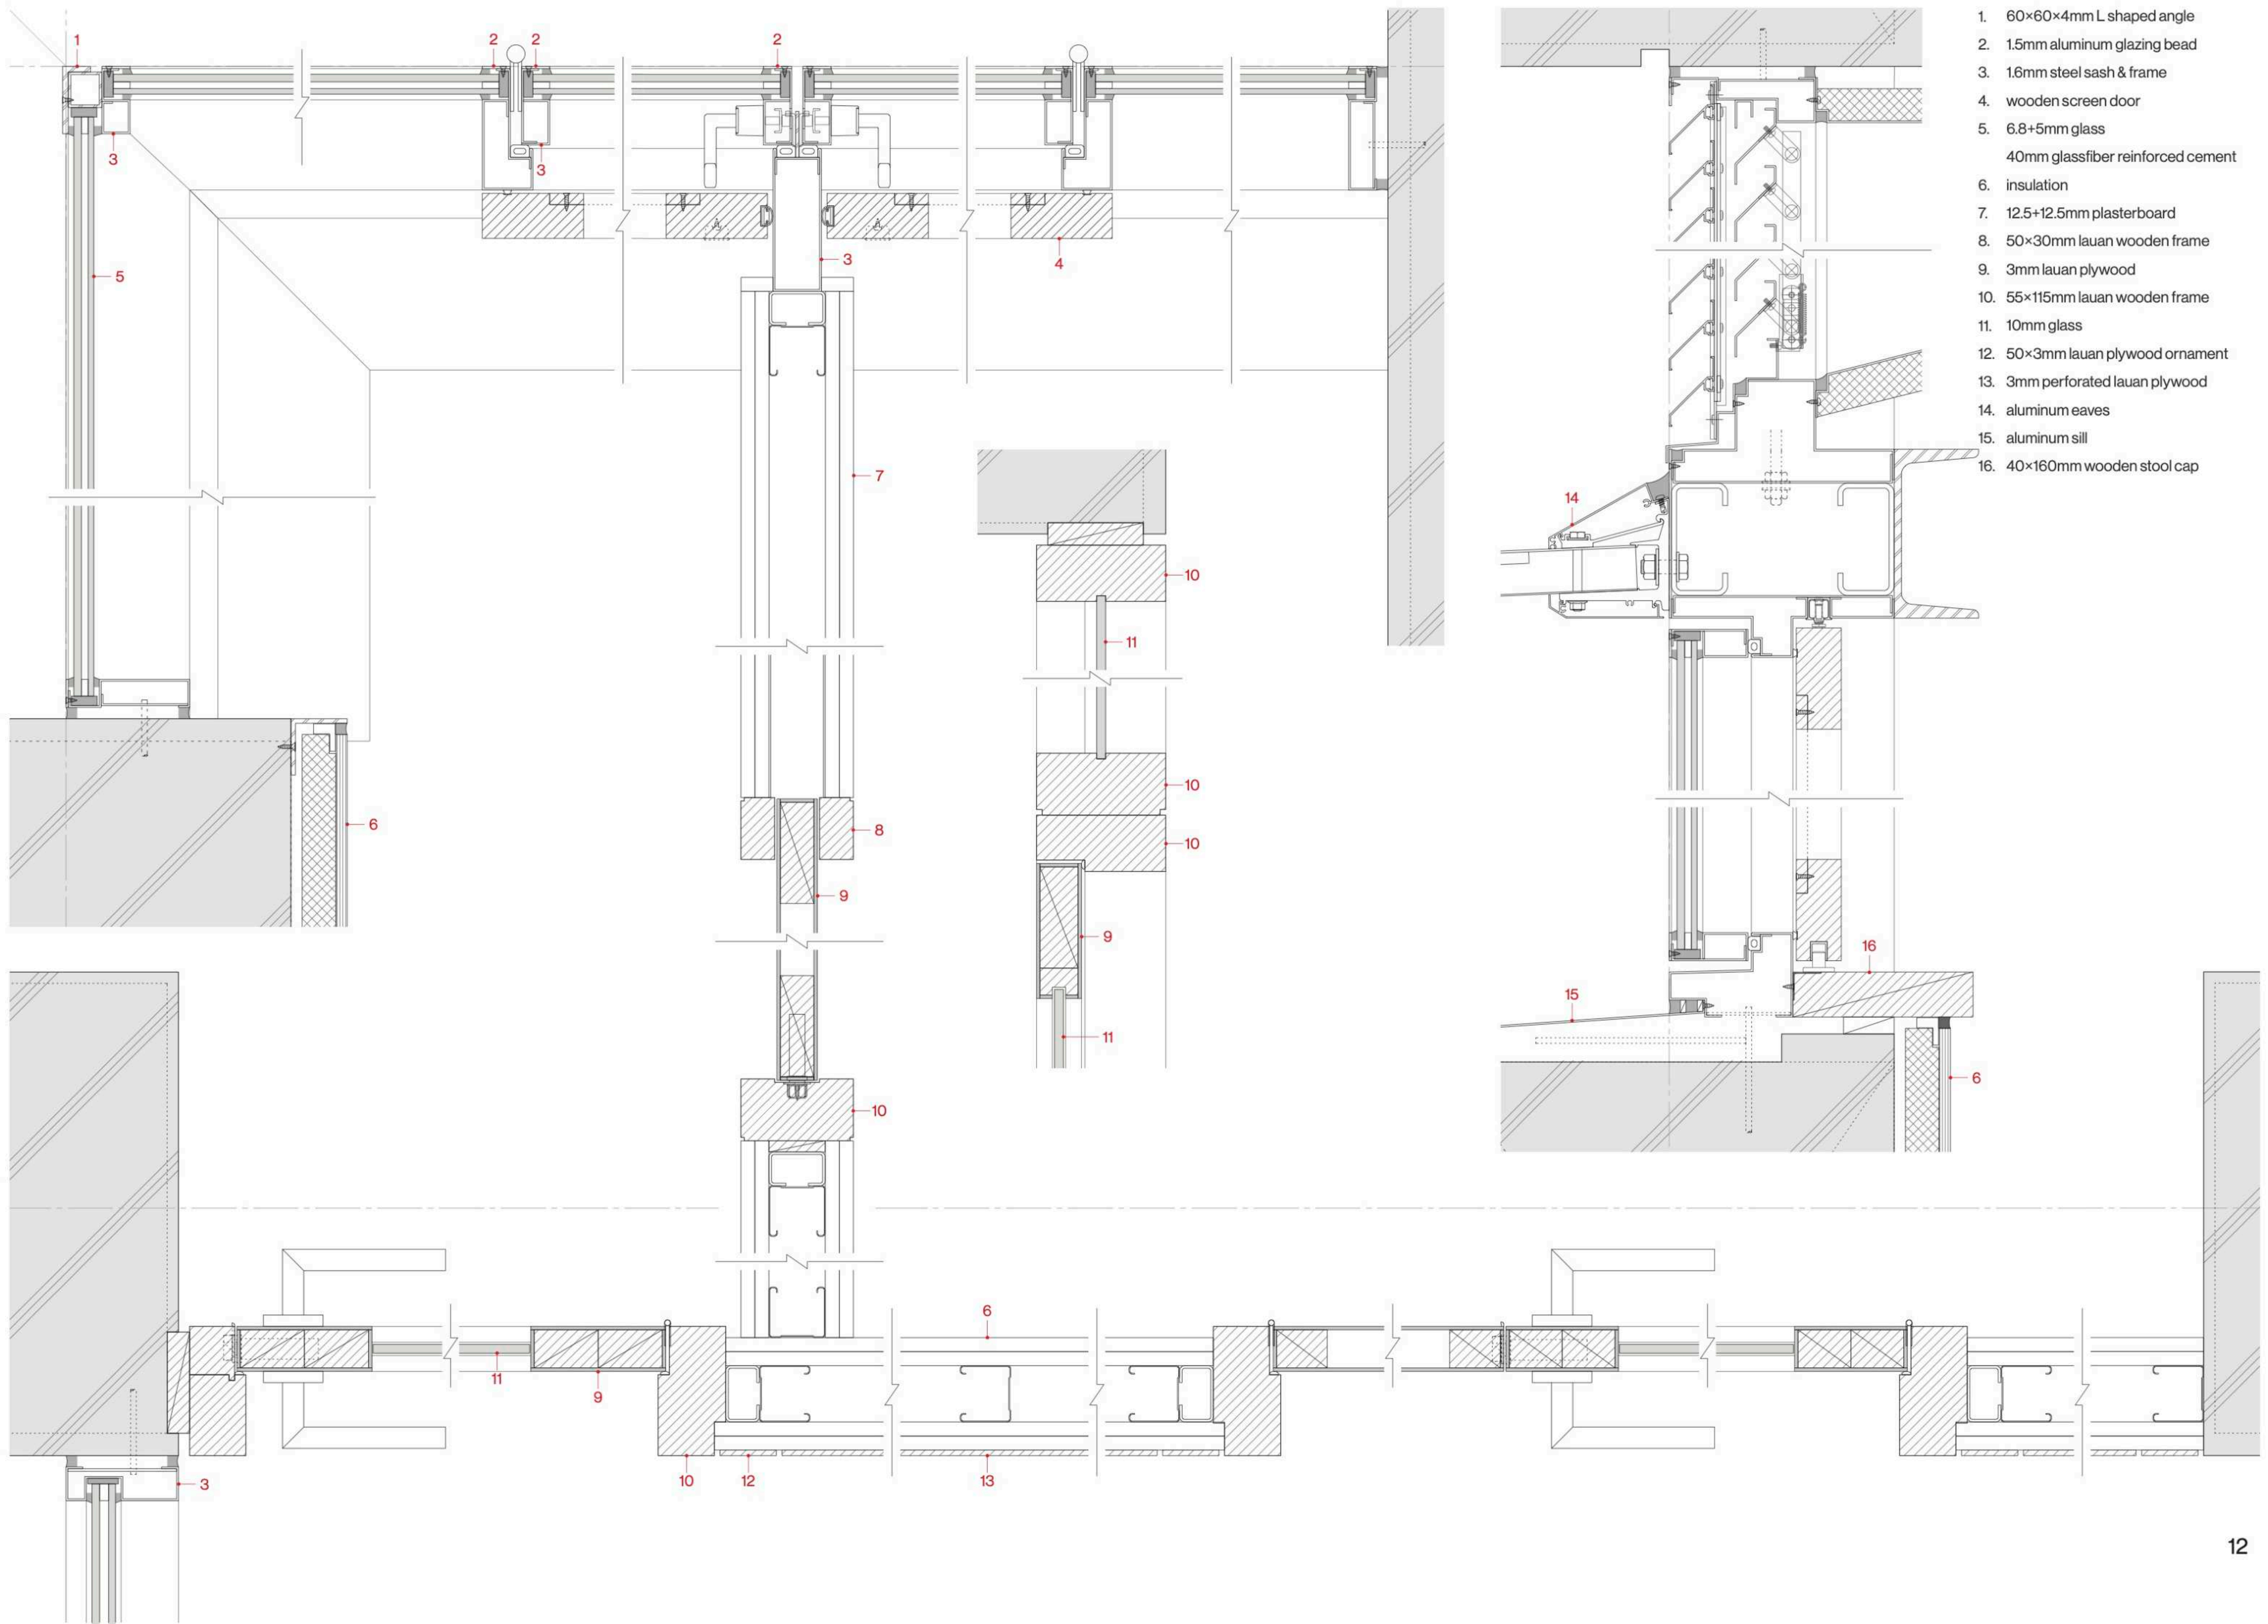



設計条件

明治大学生田キャンパスに通う学生 36 人の留学生、国内学生が居住する国際混住寮の計画である。個室面積は 7 ～ 14 m²/ 室の範囲内で設定し、トイレなどの水回りは 4 ～ 8 室で共用する。その共用部分にはキッチンやダイニング、洗濯、ラウンジなどスペースを確保する。

また、食事は共用部分で居住者が調理して食べる方針とする。寮生の学習環境を整えるため、ラーニングスペースも設けることとする。他にも、エレベーターを 1 機以上、駐輪場と、車 1 台分の駐車場を確保する。敷地内の造成にあたっては、土砂を敷地外に持ち出さないこととする。

Design Conditions

This is a plan for an international mixed-residence dormitory for 36 international and domestic students attending Meiji University's Ikuta Campus. Individual room sizes will range from 7 to 14 m² per room, with bathrooms and other water facilities shared among 4 to 8 rooms.


These shared areas will include a kitchen, dining area, laundry facilities, and a lounge. Meals will be prepared and eaten by residents in the shared areas. A learning space will also be provided to enhance the students' study environment. Additionally, at least one elevator, a bicycle parking area, and a parking space for one car will be included. During site preparation, no soil or sand will be removed from the premises.



設計の手がかり

様々な背景を持ち、全く異なる価値観や思考を備えている多国籍な学生同士が生活をともにしながら異文化理解を深めることのできる住まいについて考える。この時、密集するよりは、適度に距離を保ち、個人のプライベートな環境が点在している状態が理想的だと考えた。

そこで、高度な交流ではなく、より原始的で本能的な交流のあり方を規定するような建築を目指すことにした。つまり、文化という後天的に備えた性質ではなく、人類が共通して備えているであろうなわばり意識のようなものを設計の手がかりとした。

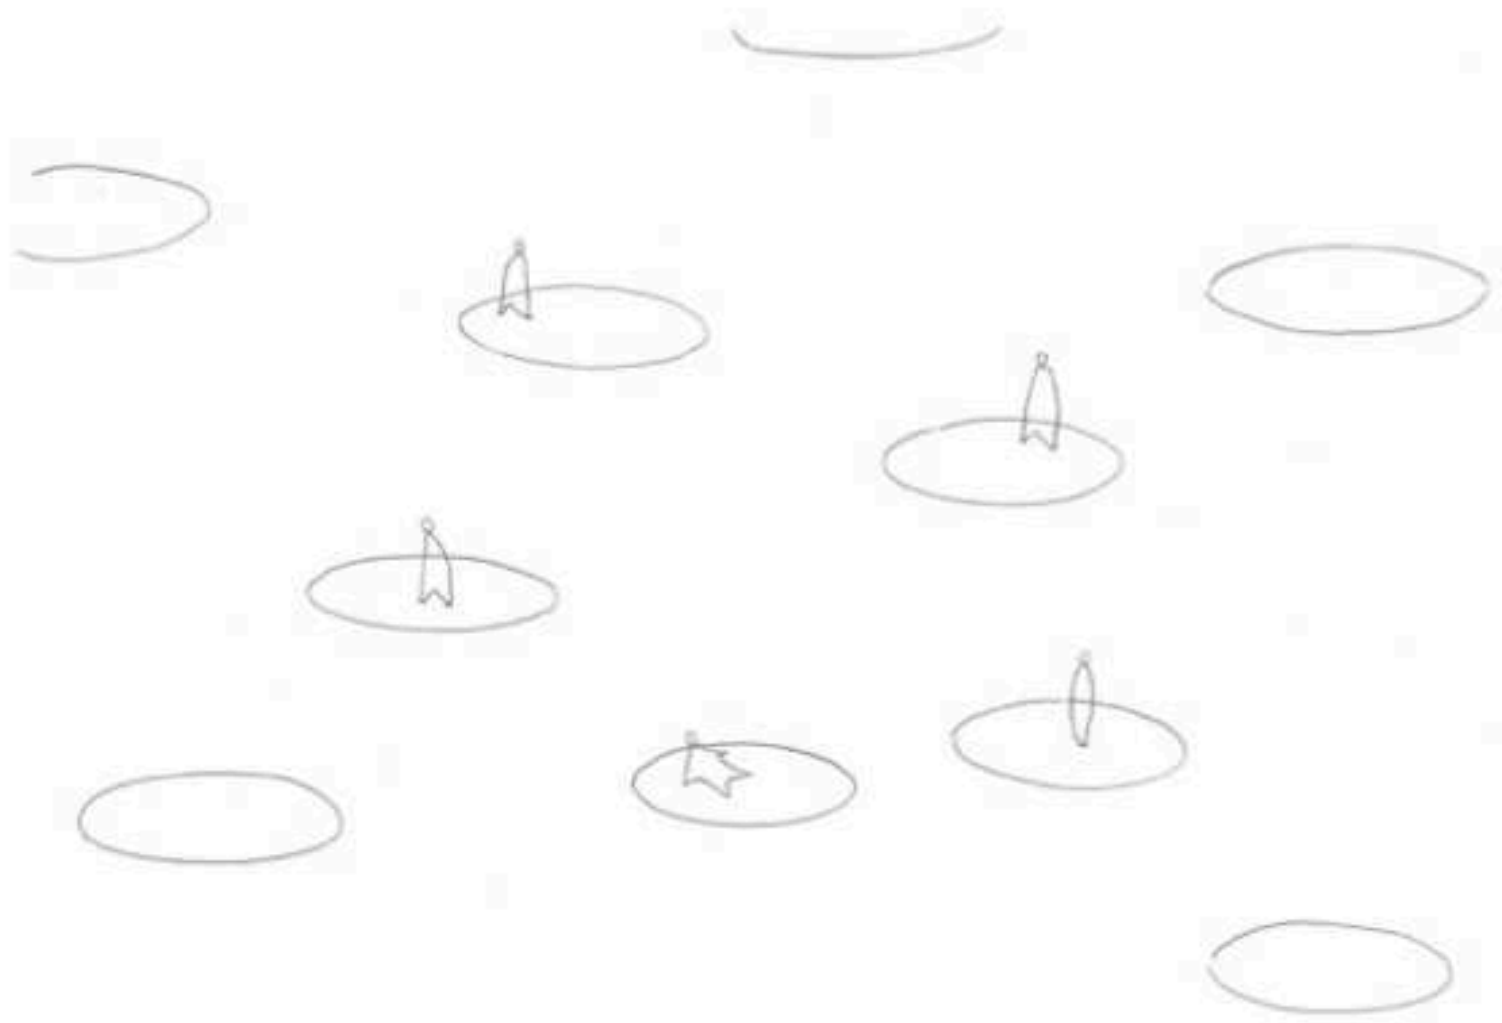

Design Clues

This project explores a form of dwelling where multinational students — each bringing distinct backgrounds, values, and ways of thinking — can live together and deepen their intercultural understanding. Rather than clustering residents in close proximity, the ideal condition was conceived as one in which a moderate distance is maintained between individuals, with each person's private environment dispersed across the whole.

With this in mind, the design sought not to facilitate sophisticated cultural exchange, but instead to give architectural form to a more primitive and instinctive mode of human interaction. In other words, the guiding principle was not culture — an acquired characteristic — but rather something akin to the territorial instinct that appears to be universally shared across humanity.



構造コンセプト
部分から全体へ / 全体から部分へ

柱および梁の断面寸法とグリッドの寸法の検討を繰り返した結果、プライベート空間となる各住民の住戸ブロックを 2 マスに分割したグリッドの平面寸法を 2600mm × 2600mm の RC ラーメン造が最適であると判断した。

これを基準とした同一の正方形のみを複製して構成された建築を提案する。これにより、後述する全てのエリアは、等価なグリッド同士の関係性へと帰着する。

Structural Concept
From Part to Whole / From Whole to Part

Through repeated study of column and beam cross-sections alongside grid dimensions, a reinforced concrete rigid frame structure with a plan grid of 2,600 mm × 2,600 mm — derived by subdividing each resident's private residential unit into two bays — was determined to be the optimal solution.

The proposal replicates this single square unit consistently throughout, without variation. As a result, all areas mentioned later private, intermediate, and common resolve into a relationship of equivalent, homogeneous grid units.

プログラム
機能のグラデーション

同一フロアの寮生が共有して利用するコモンスペース、数名の住戸の前に位置する中間領域、各寮生のプライベート空間である住戸ユニットは、住民にとってのプライベートな領域とパブリックな領域を完全に分断するのではなく、建築内部の各グリッドを段階的に、ゆるやかに繋げている。


このグラデーションが学生同士の自然なコミュニケーションを誘発するだろう。

Programme
A Gradient of Function

The common space shared by residents on the same floor, the intermediate space situated in front of a small cluster of units, and the residential unit that forms each student's private domain are not organized as a strict binary division between private and public.

Instead, each grid within the building is connected gradually and loosely, forming a continuous spatial gradient.

It is this gradation that is expected to naturally encourage spontaneous communication among students.

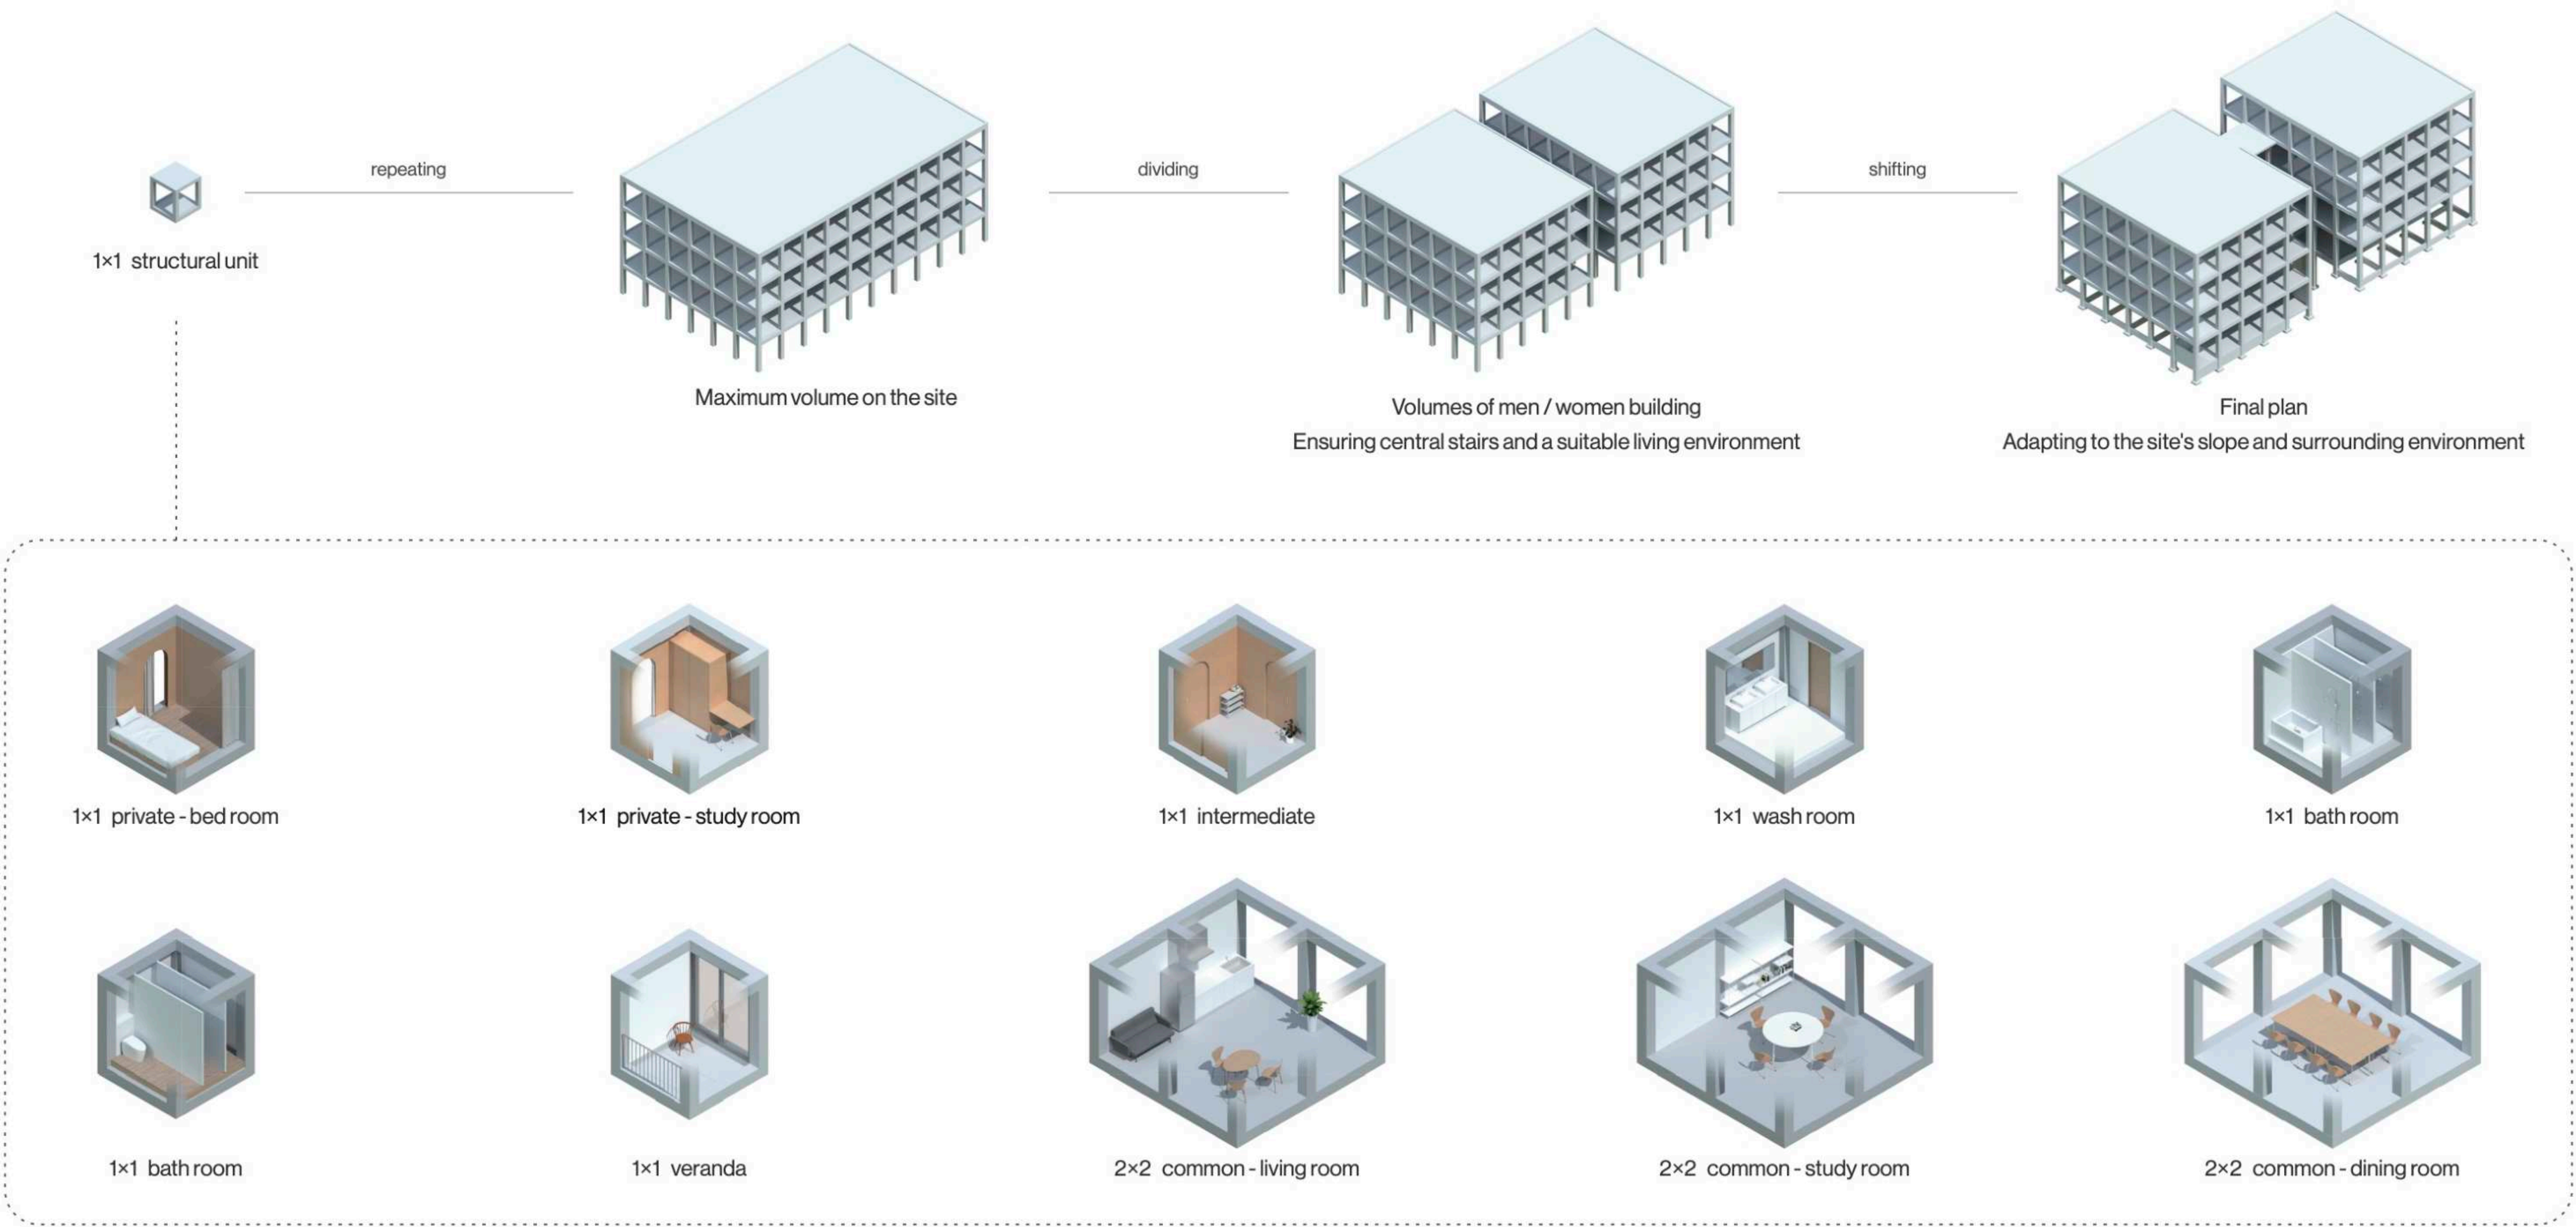

プライベート空間 — 住戸ユニット


2つのマスで構成される住戸ユニットは、それぞれ寝室とワークスペースの用途からなっている。最もプライベート性の高い寝床としての寝室は、ワークスペースを介してコモンから距離を取るよう配置され、空間のグラデーションを高める。
これらのユニットを仕切る2つのアーチはプライベート空間の象徴であり、わずかに空間の軸性をも生む。

学生は一人の時間を楽しむためにこの空間を閉ざして自習すること
もできるし、隣人と親しくなれば、コミュニケーションを取るため
に扉を開放してコモンとの接続を図ることもできる。



Private Space — Residential Unit


Each residential unit, composed of two bays, comprises a bedroom and a workspace. The bedroom — the most private zone, serving as a place of rest — is positioned at a distance from the common space, with the workspace acting as an intermediary, thereby enhancing the spatial gradient.
The two arches that divide these units are symbolic of private space, while also subtly generating a sense of spatial axiality.

A student may close off this space for solitary study and private time, or, as familiarity with neighbours grows, may open the doors to connect with the common area and invite interaction.

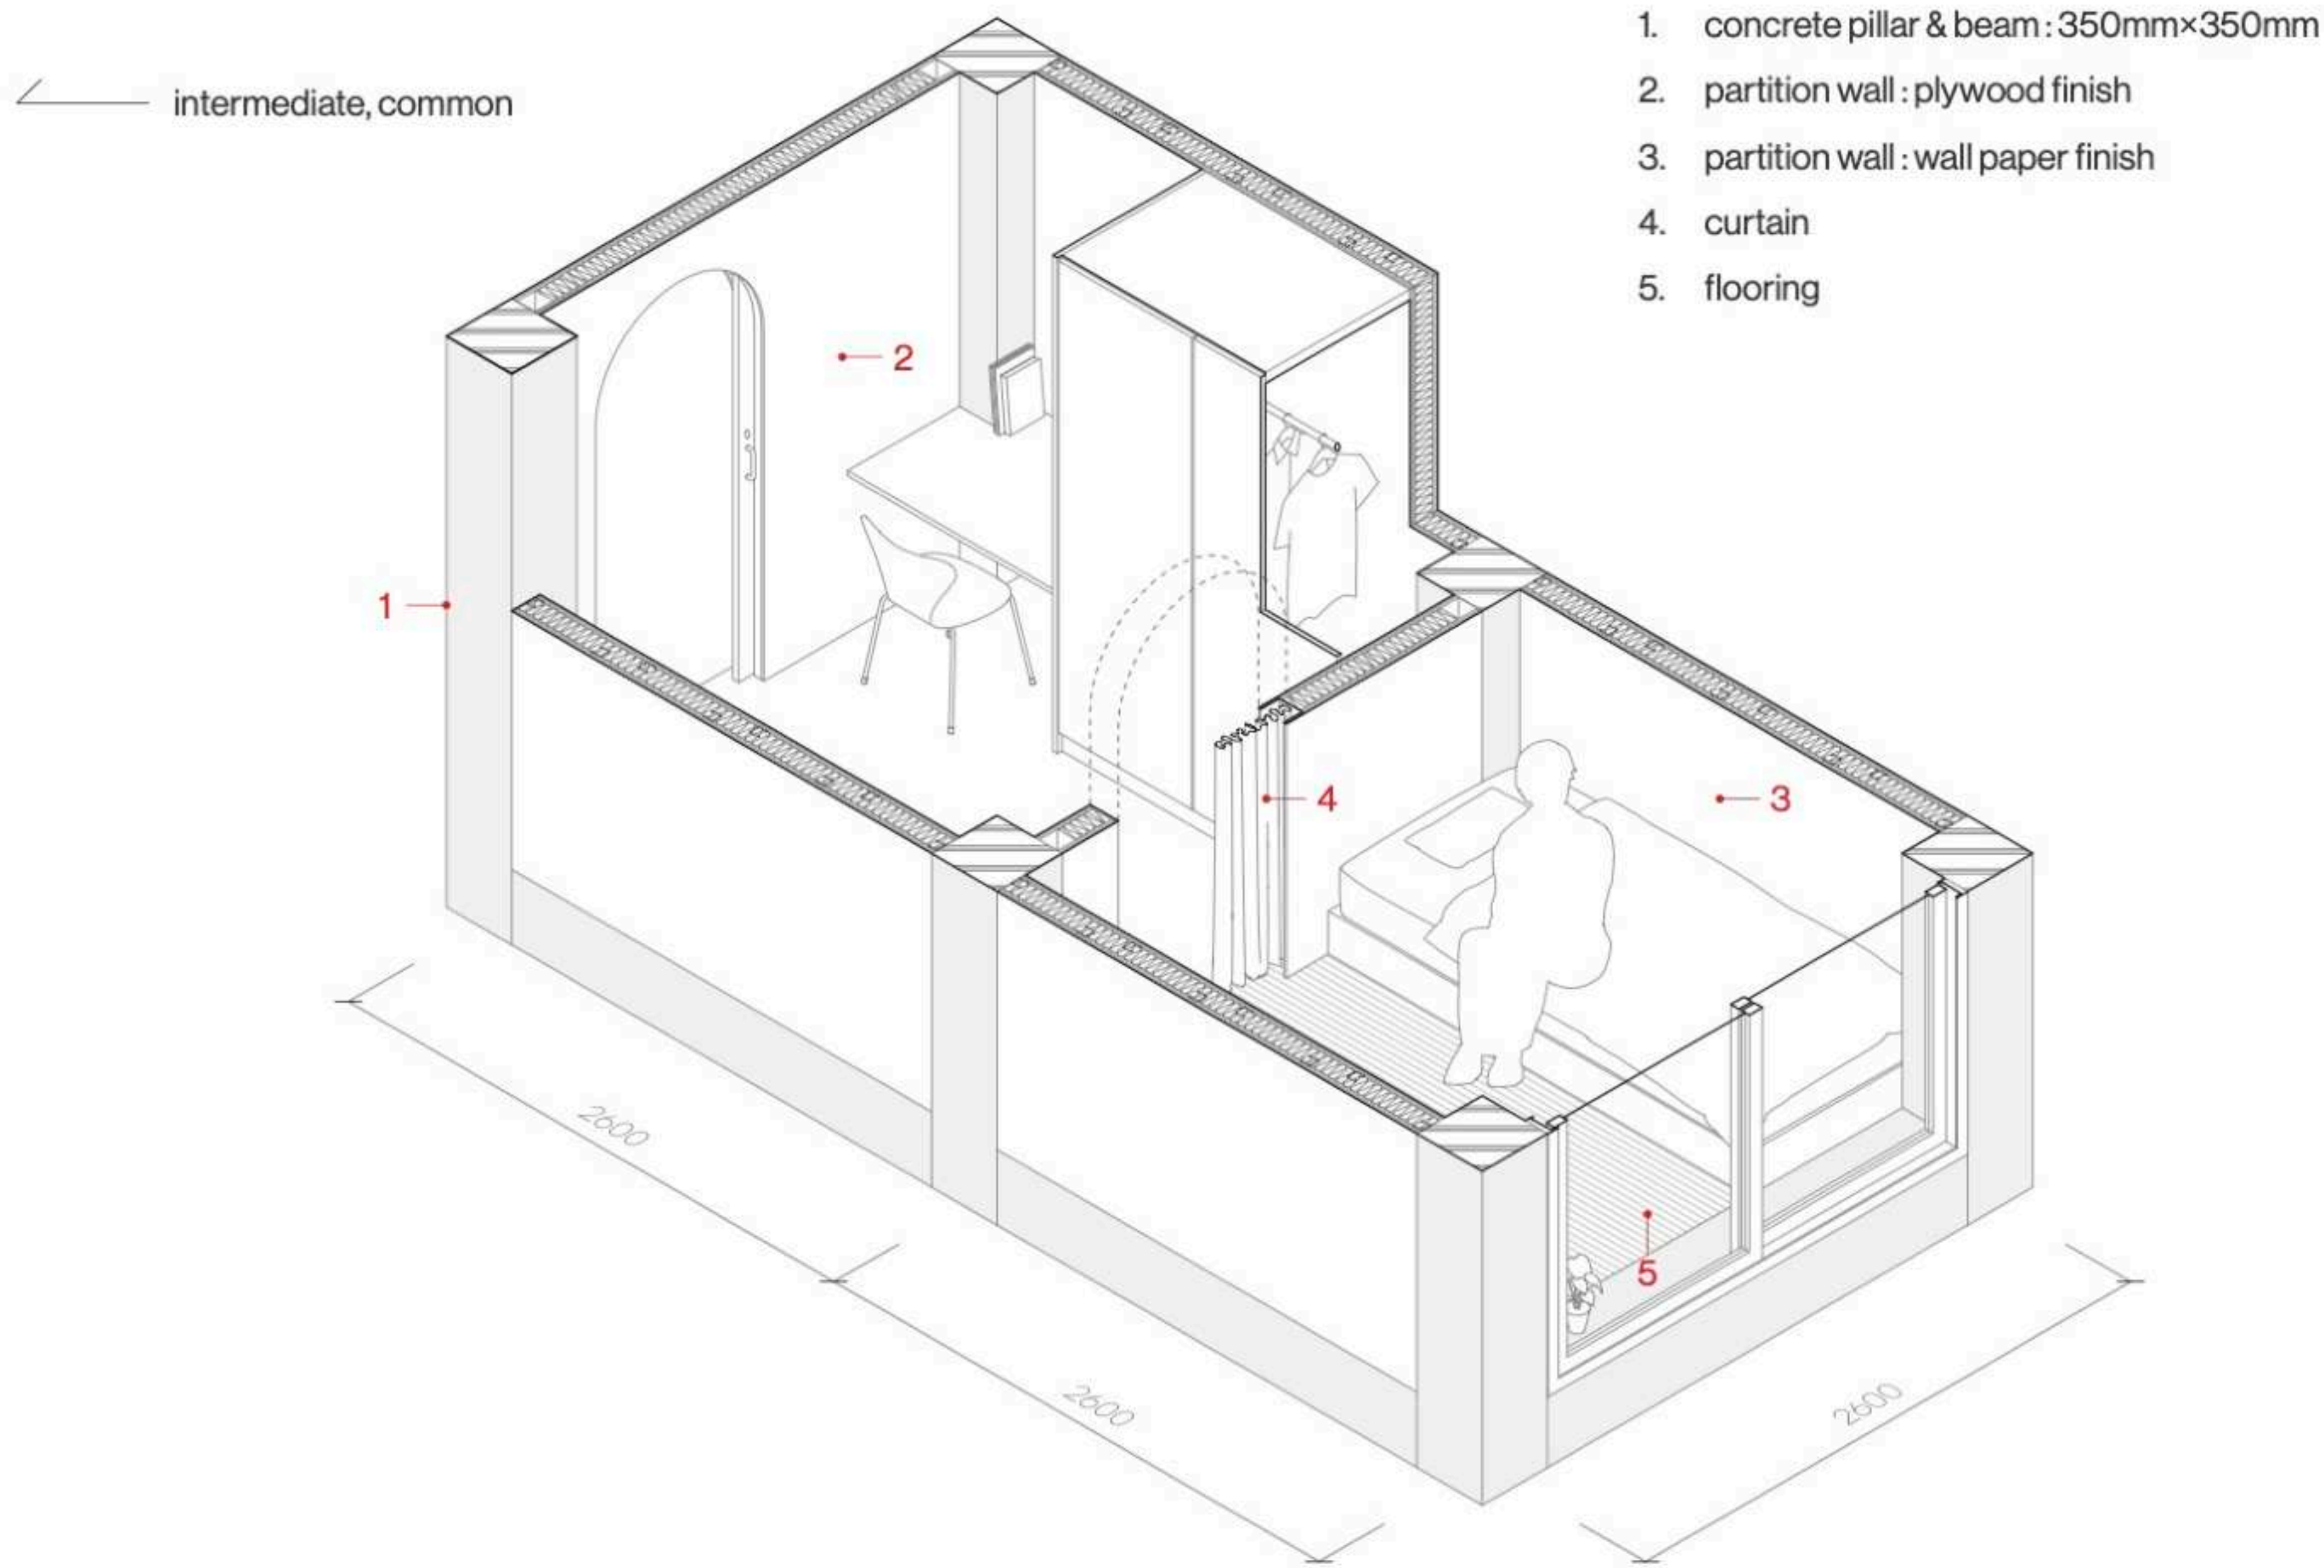


Residential Unit Axonometric Drawing

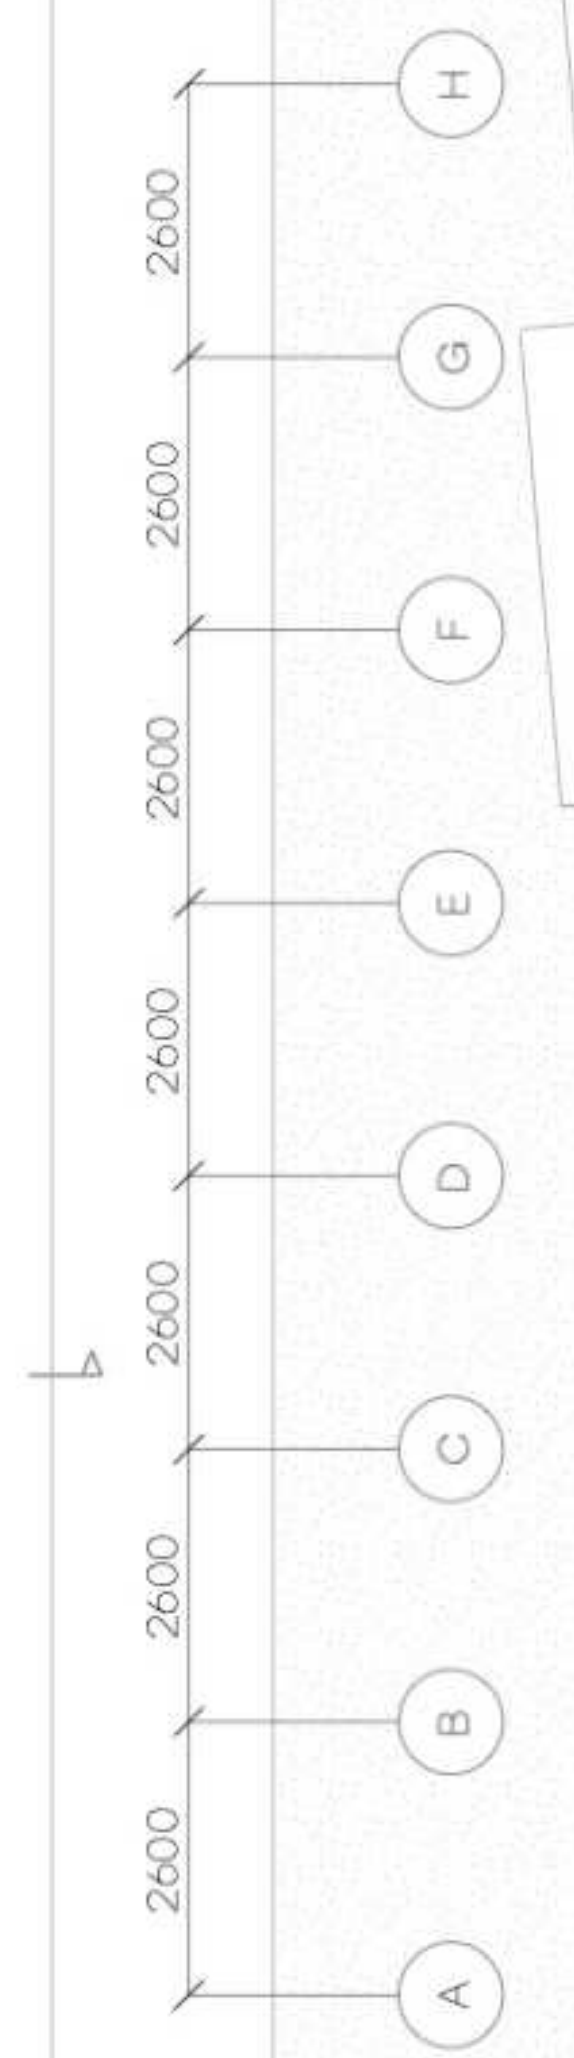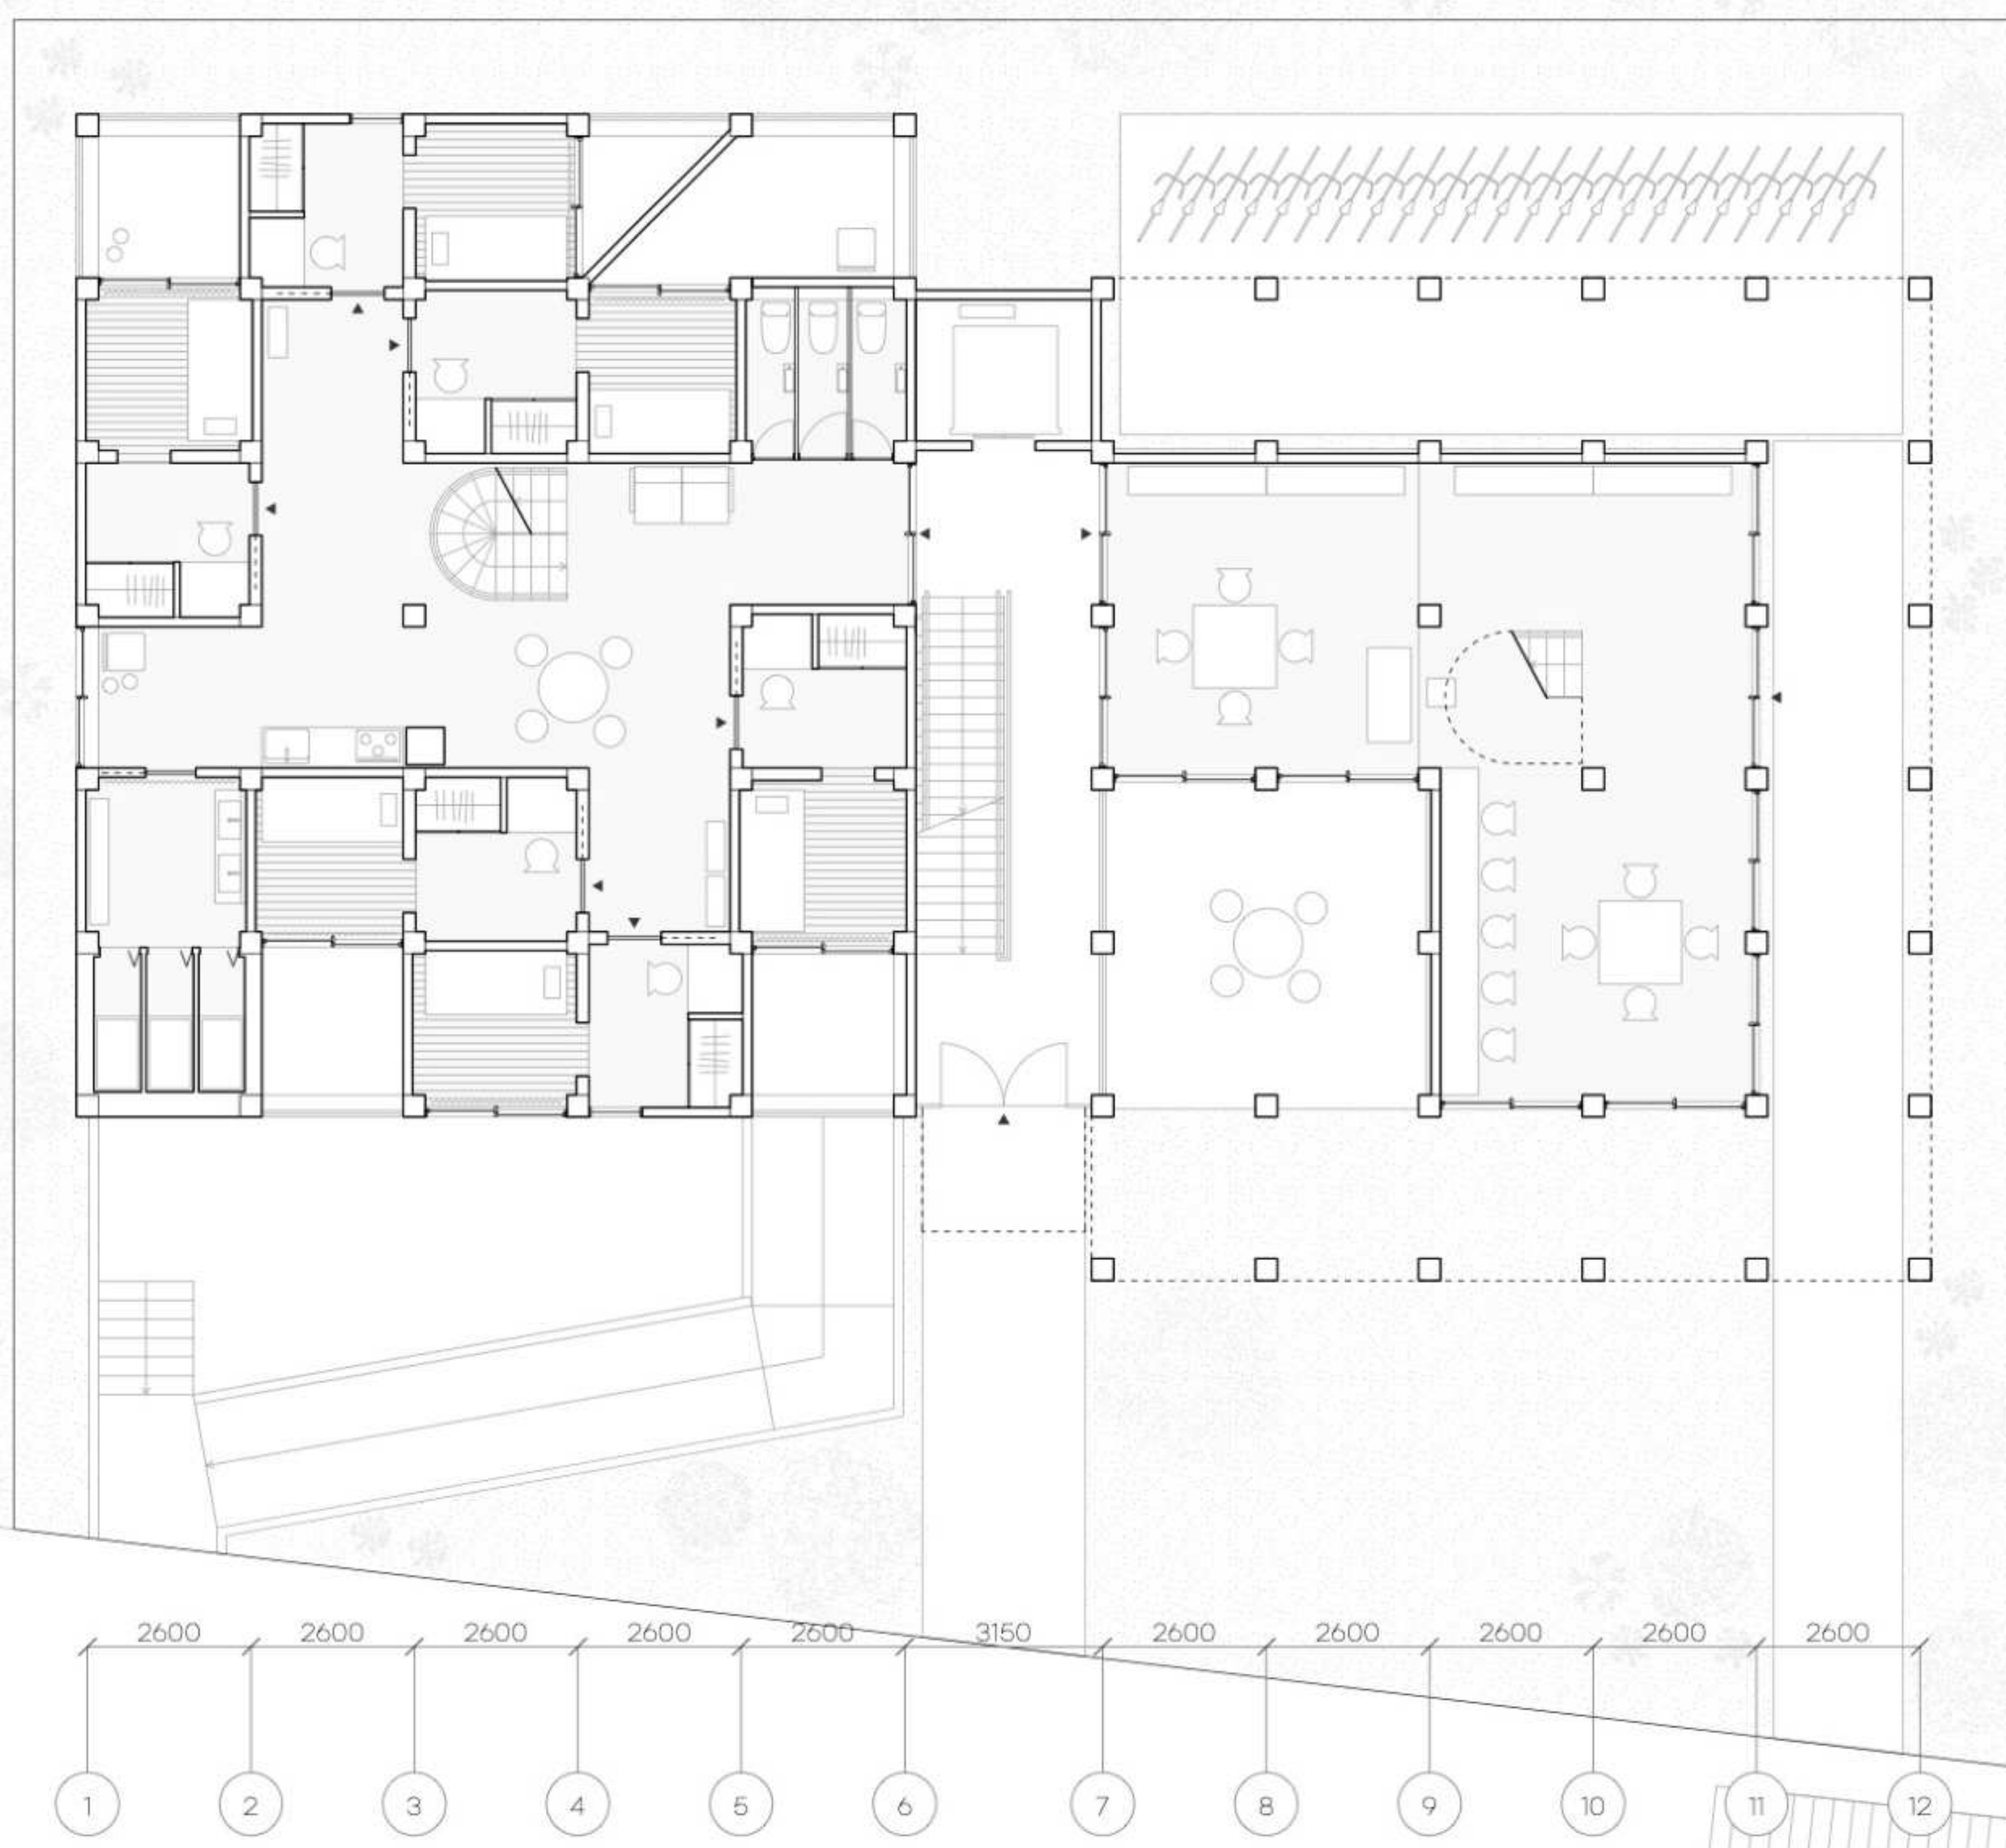


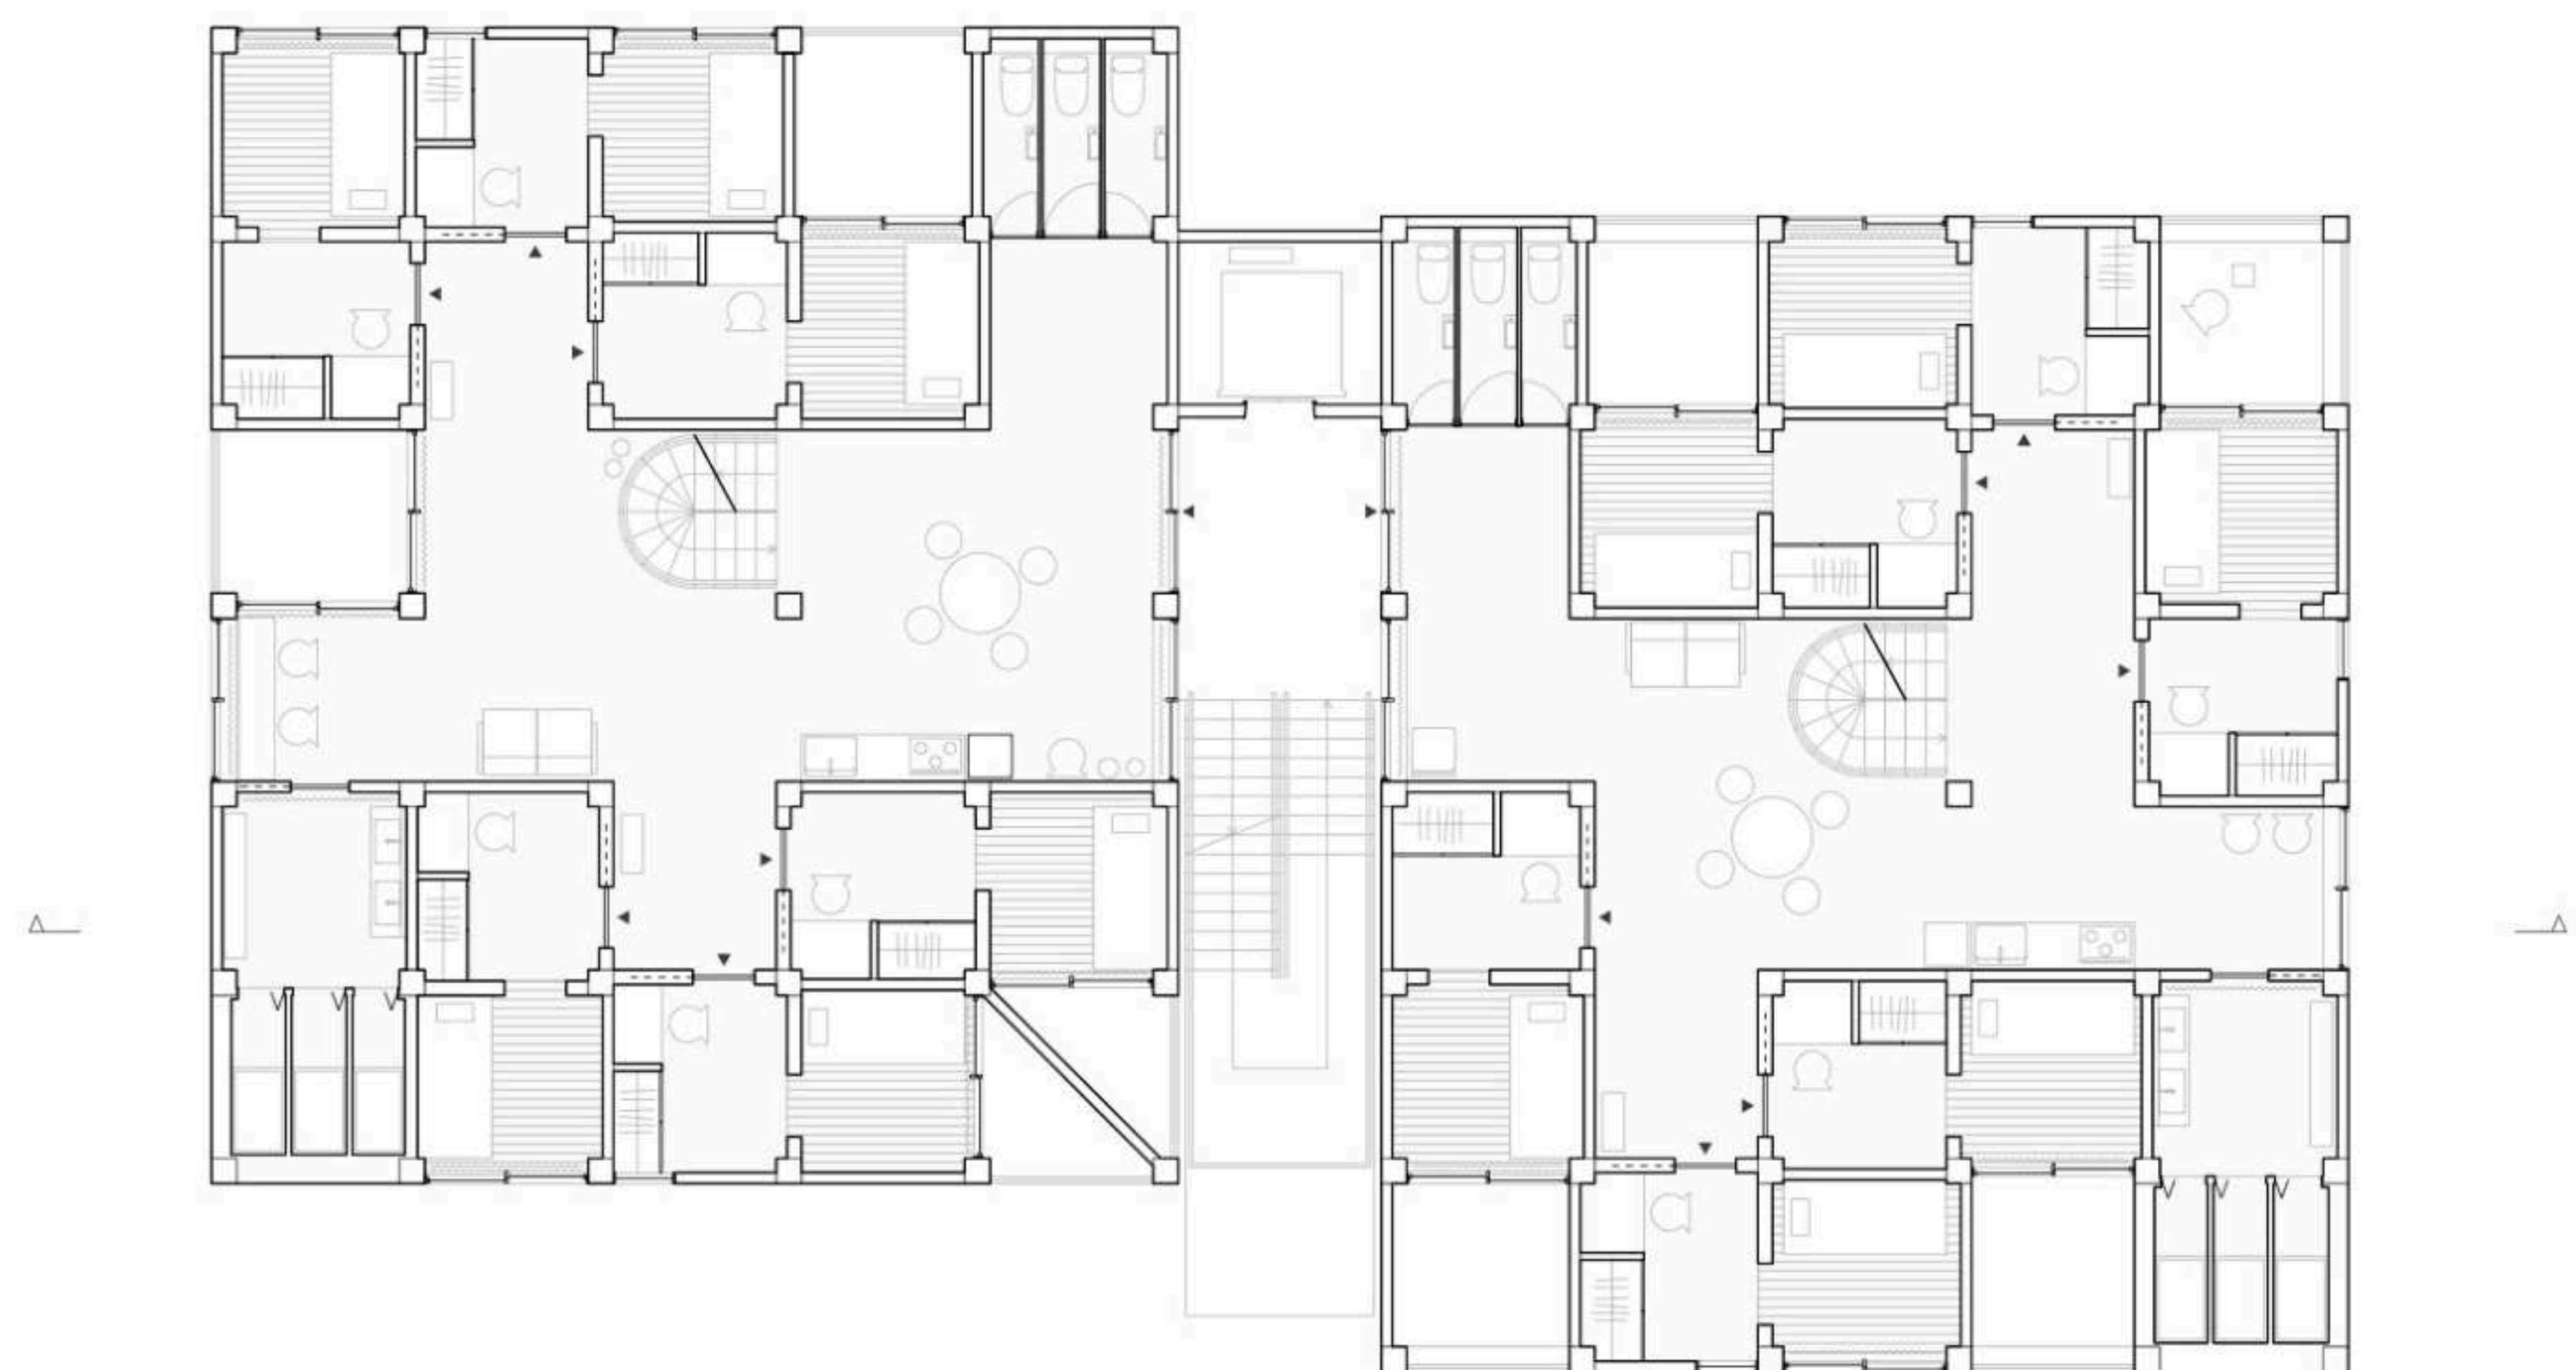


1/200 2F Plan Drawing

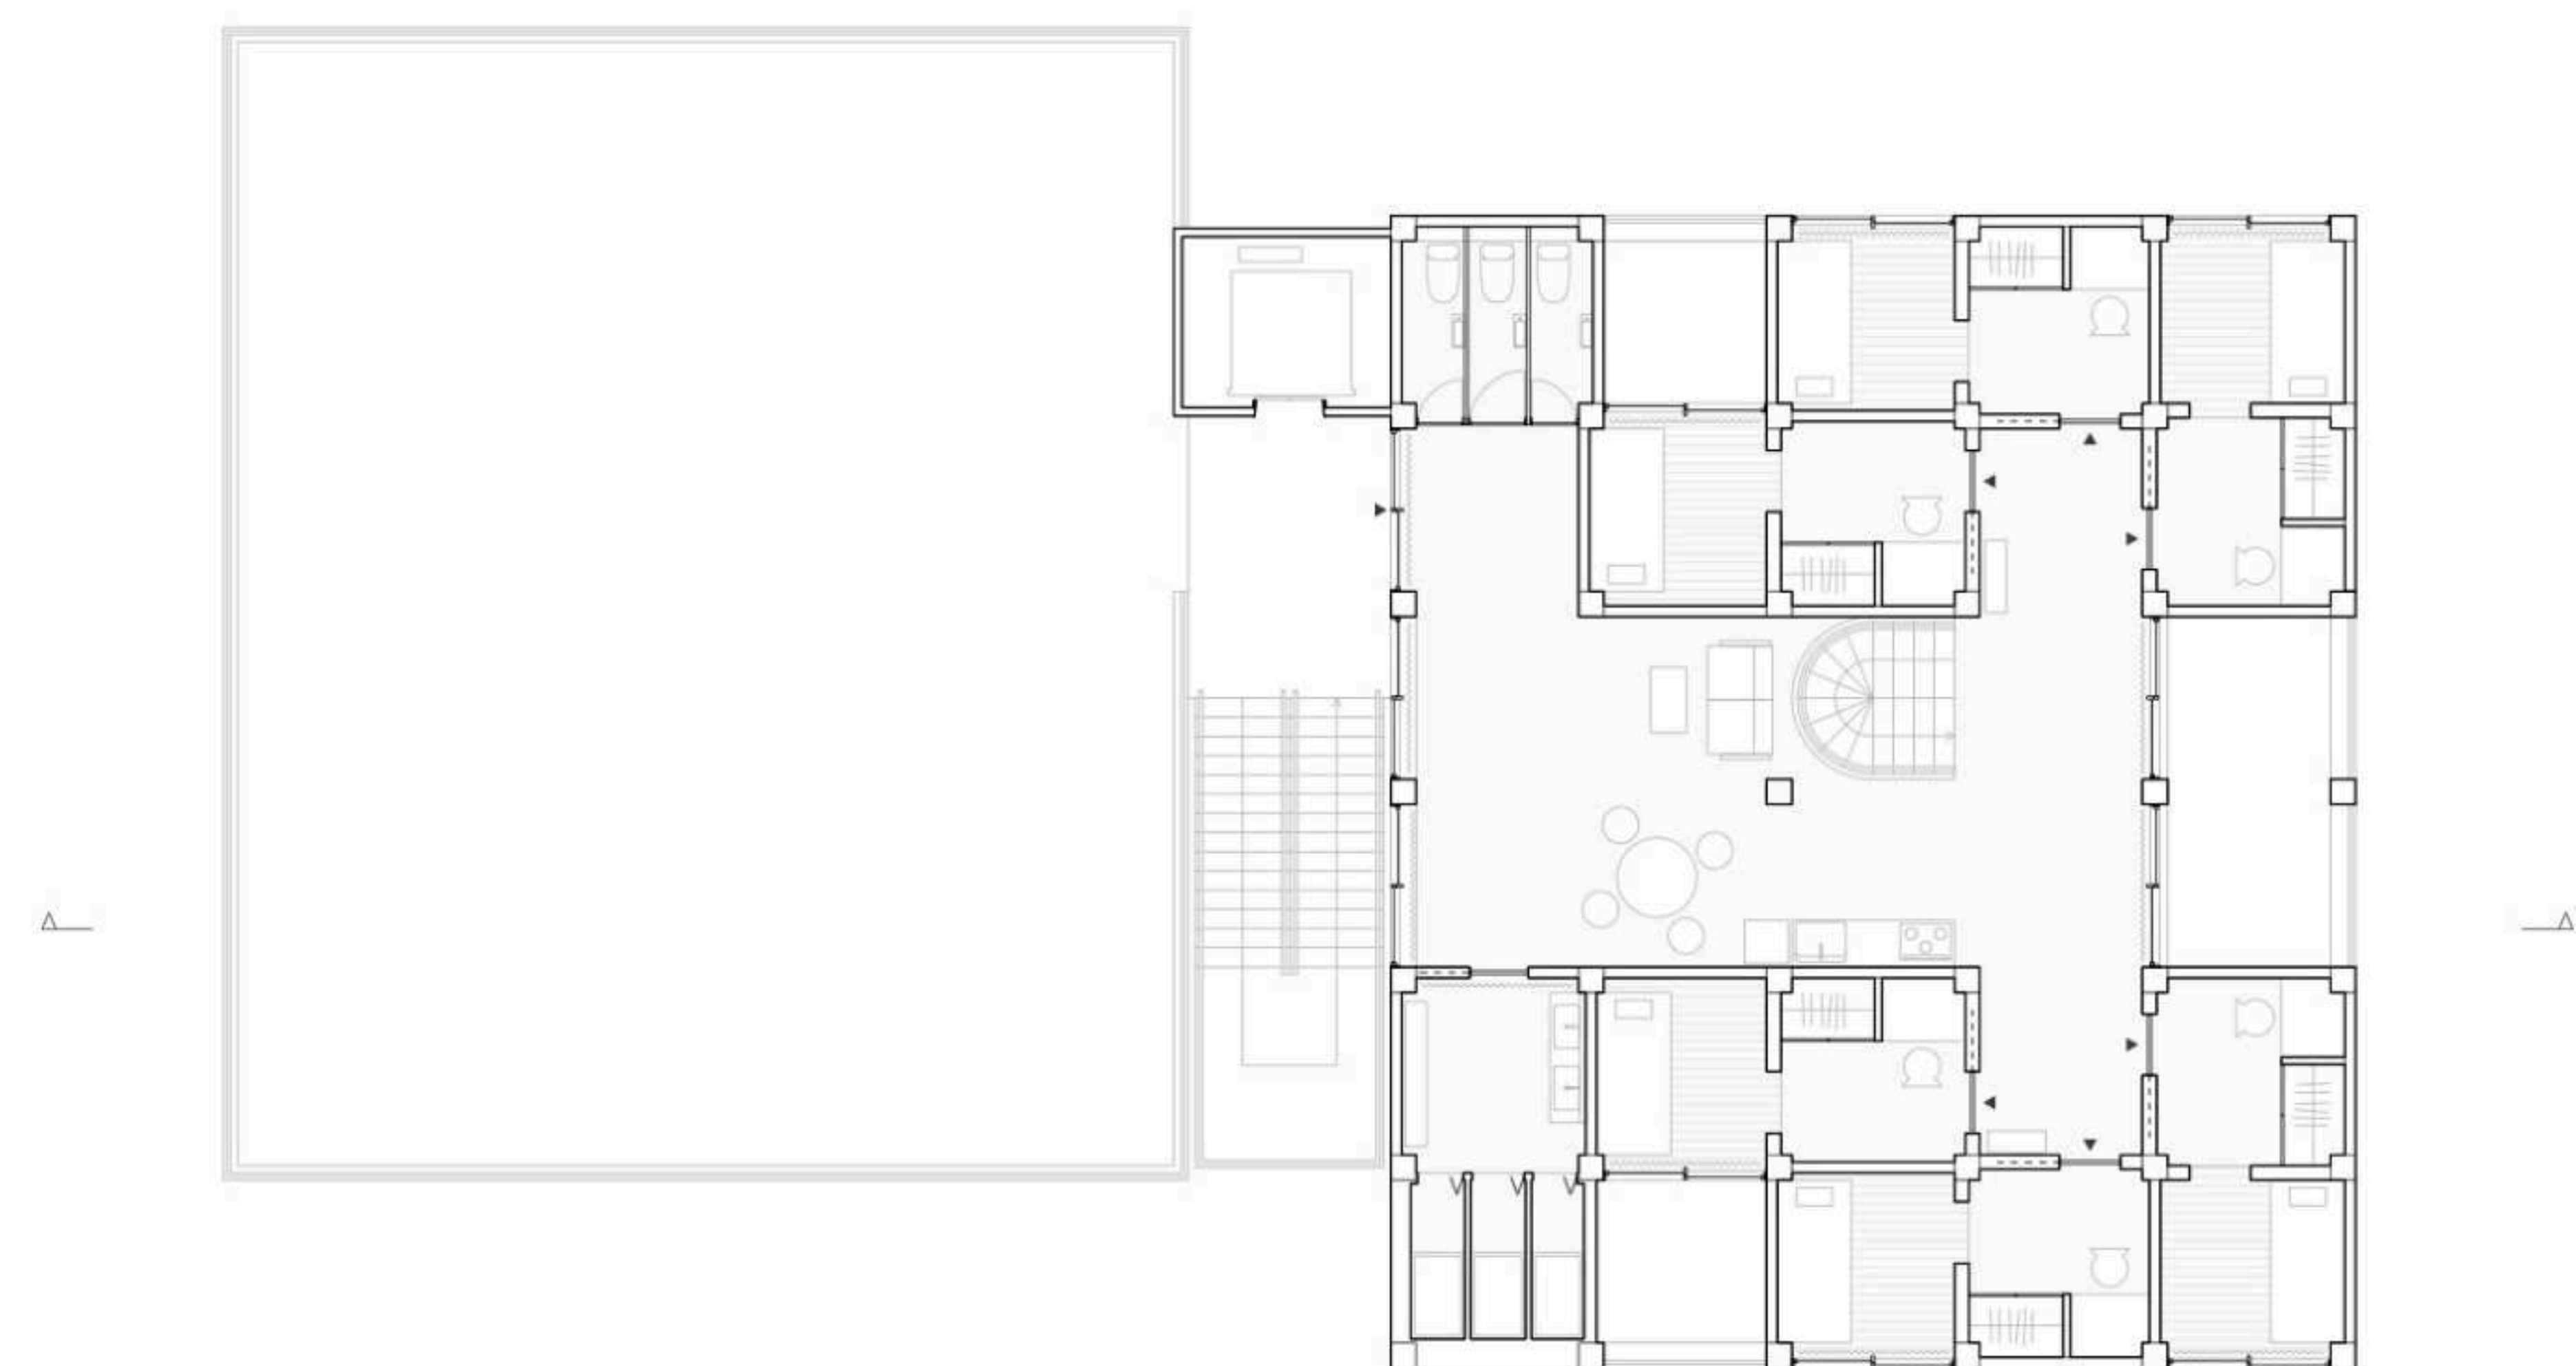

1/200 4F Plan Drawing

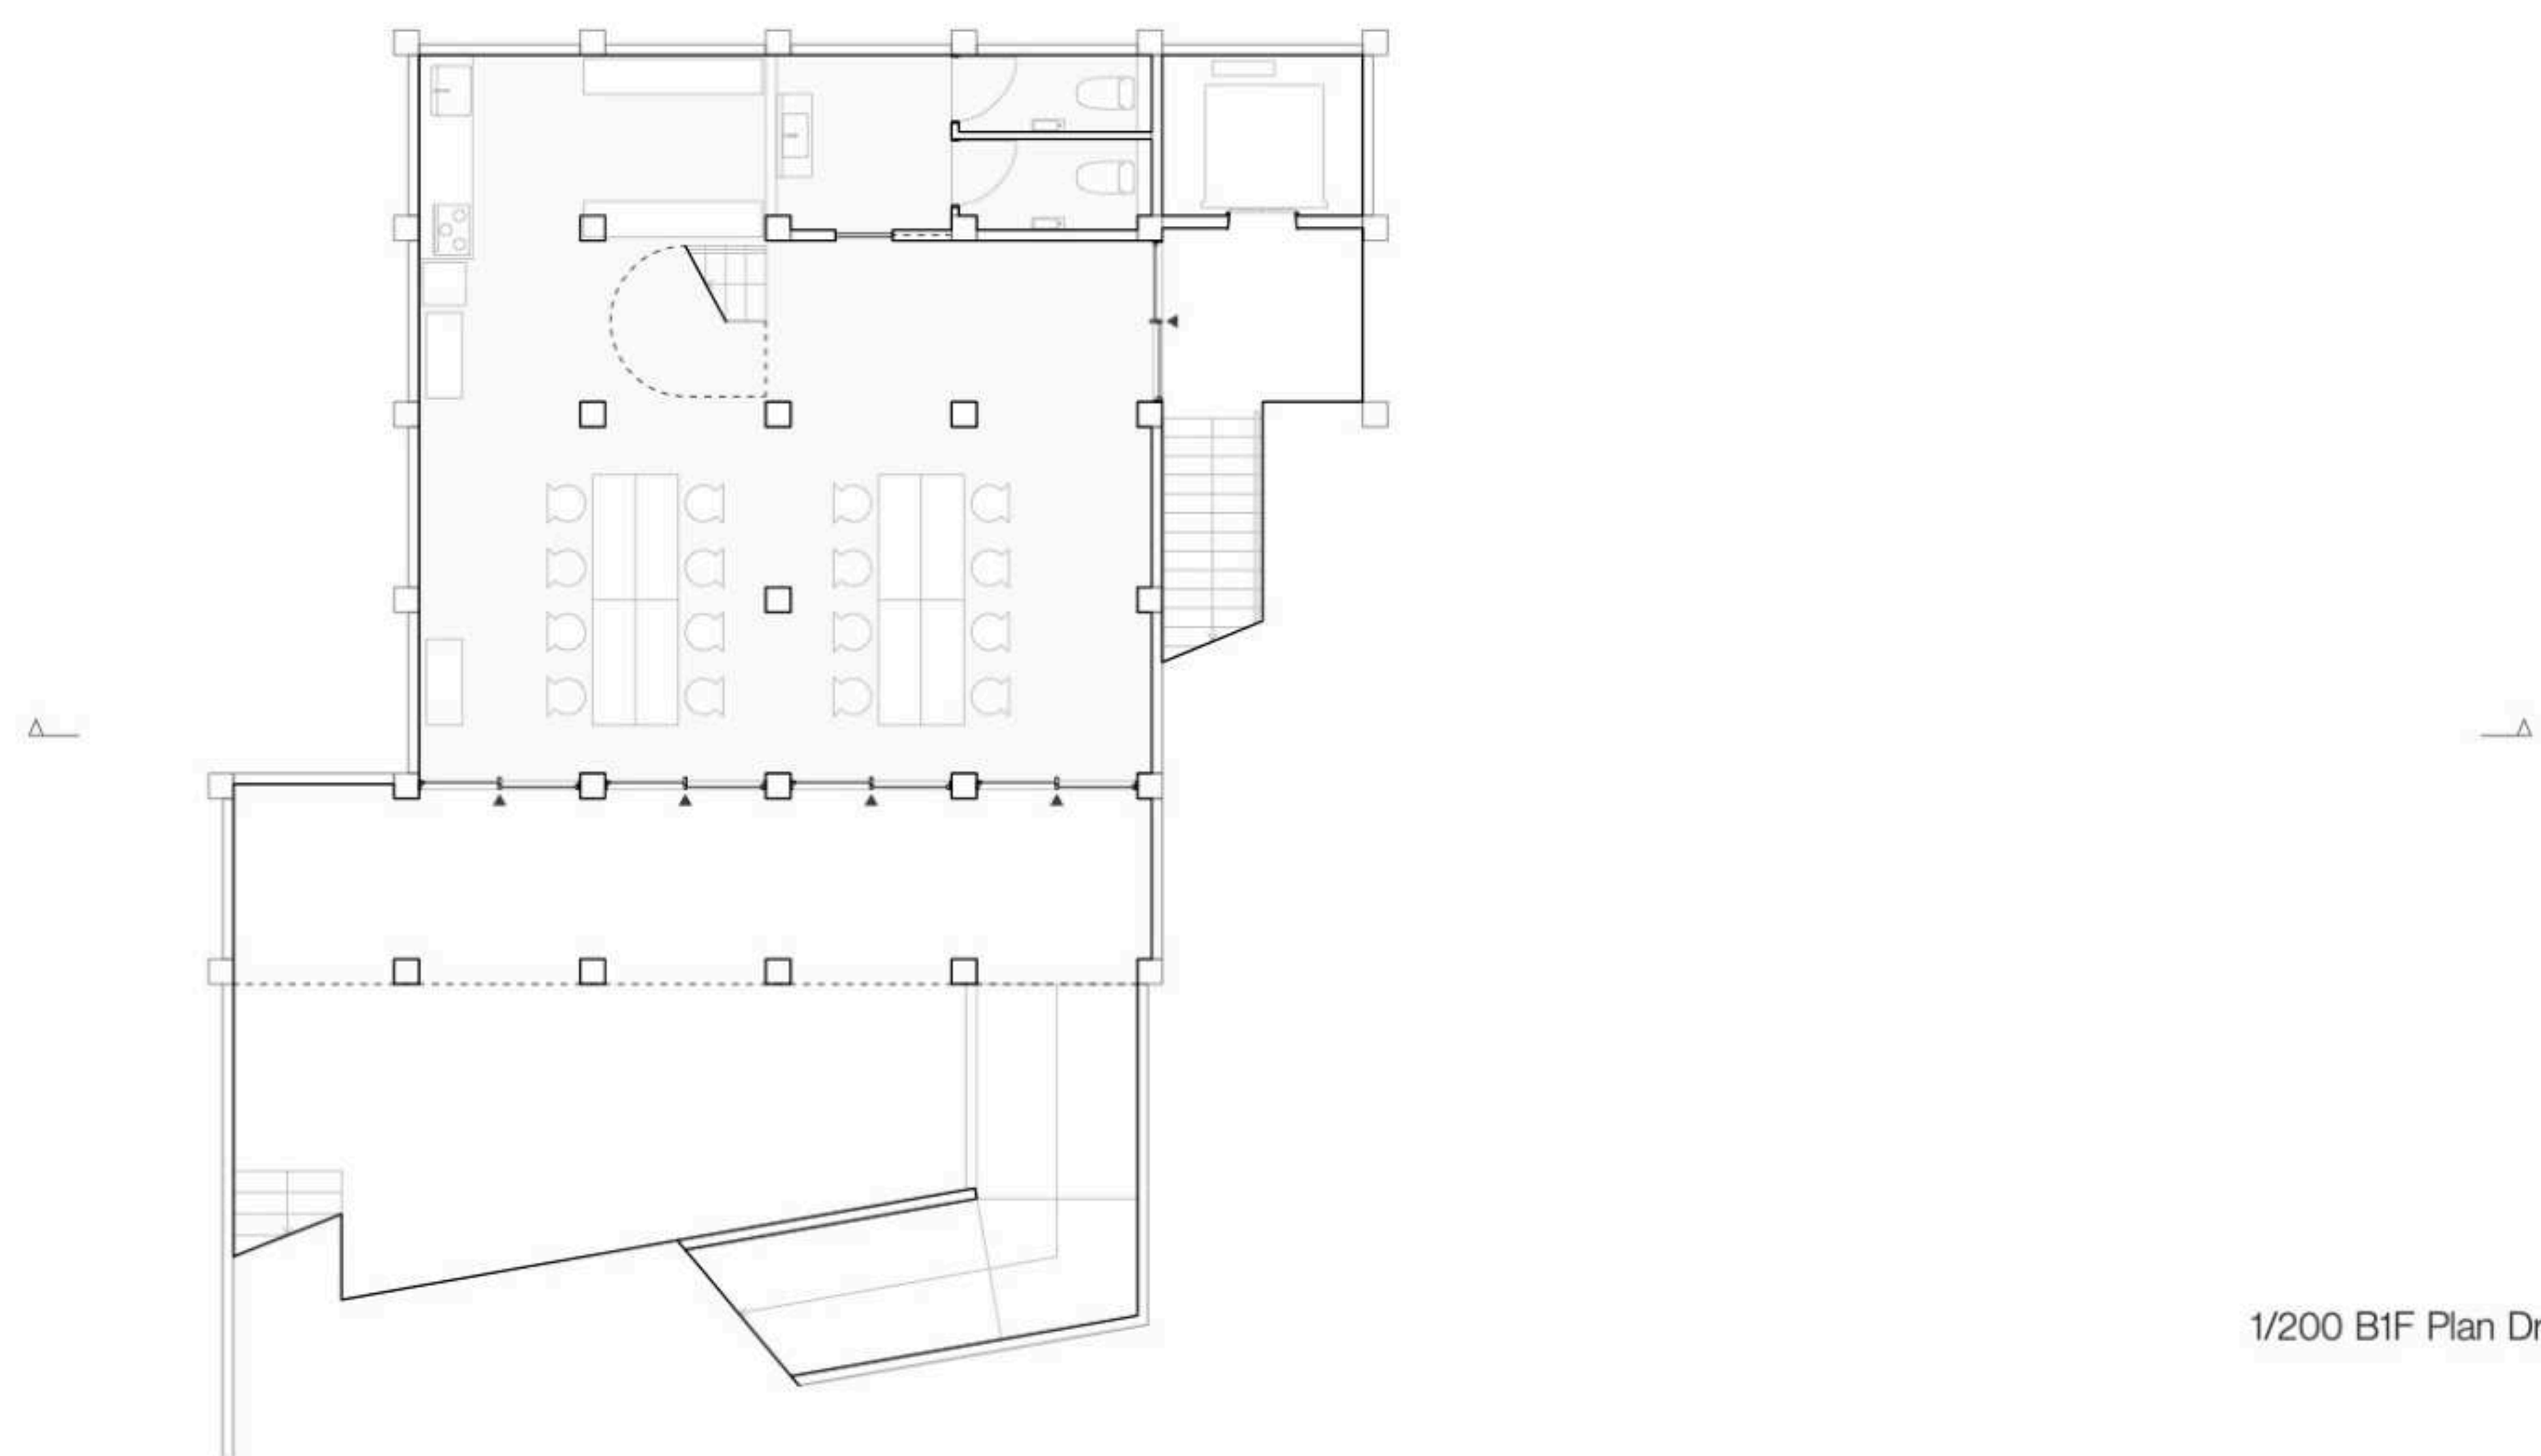

1/200 B1F Plan Drawing

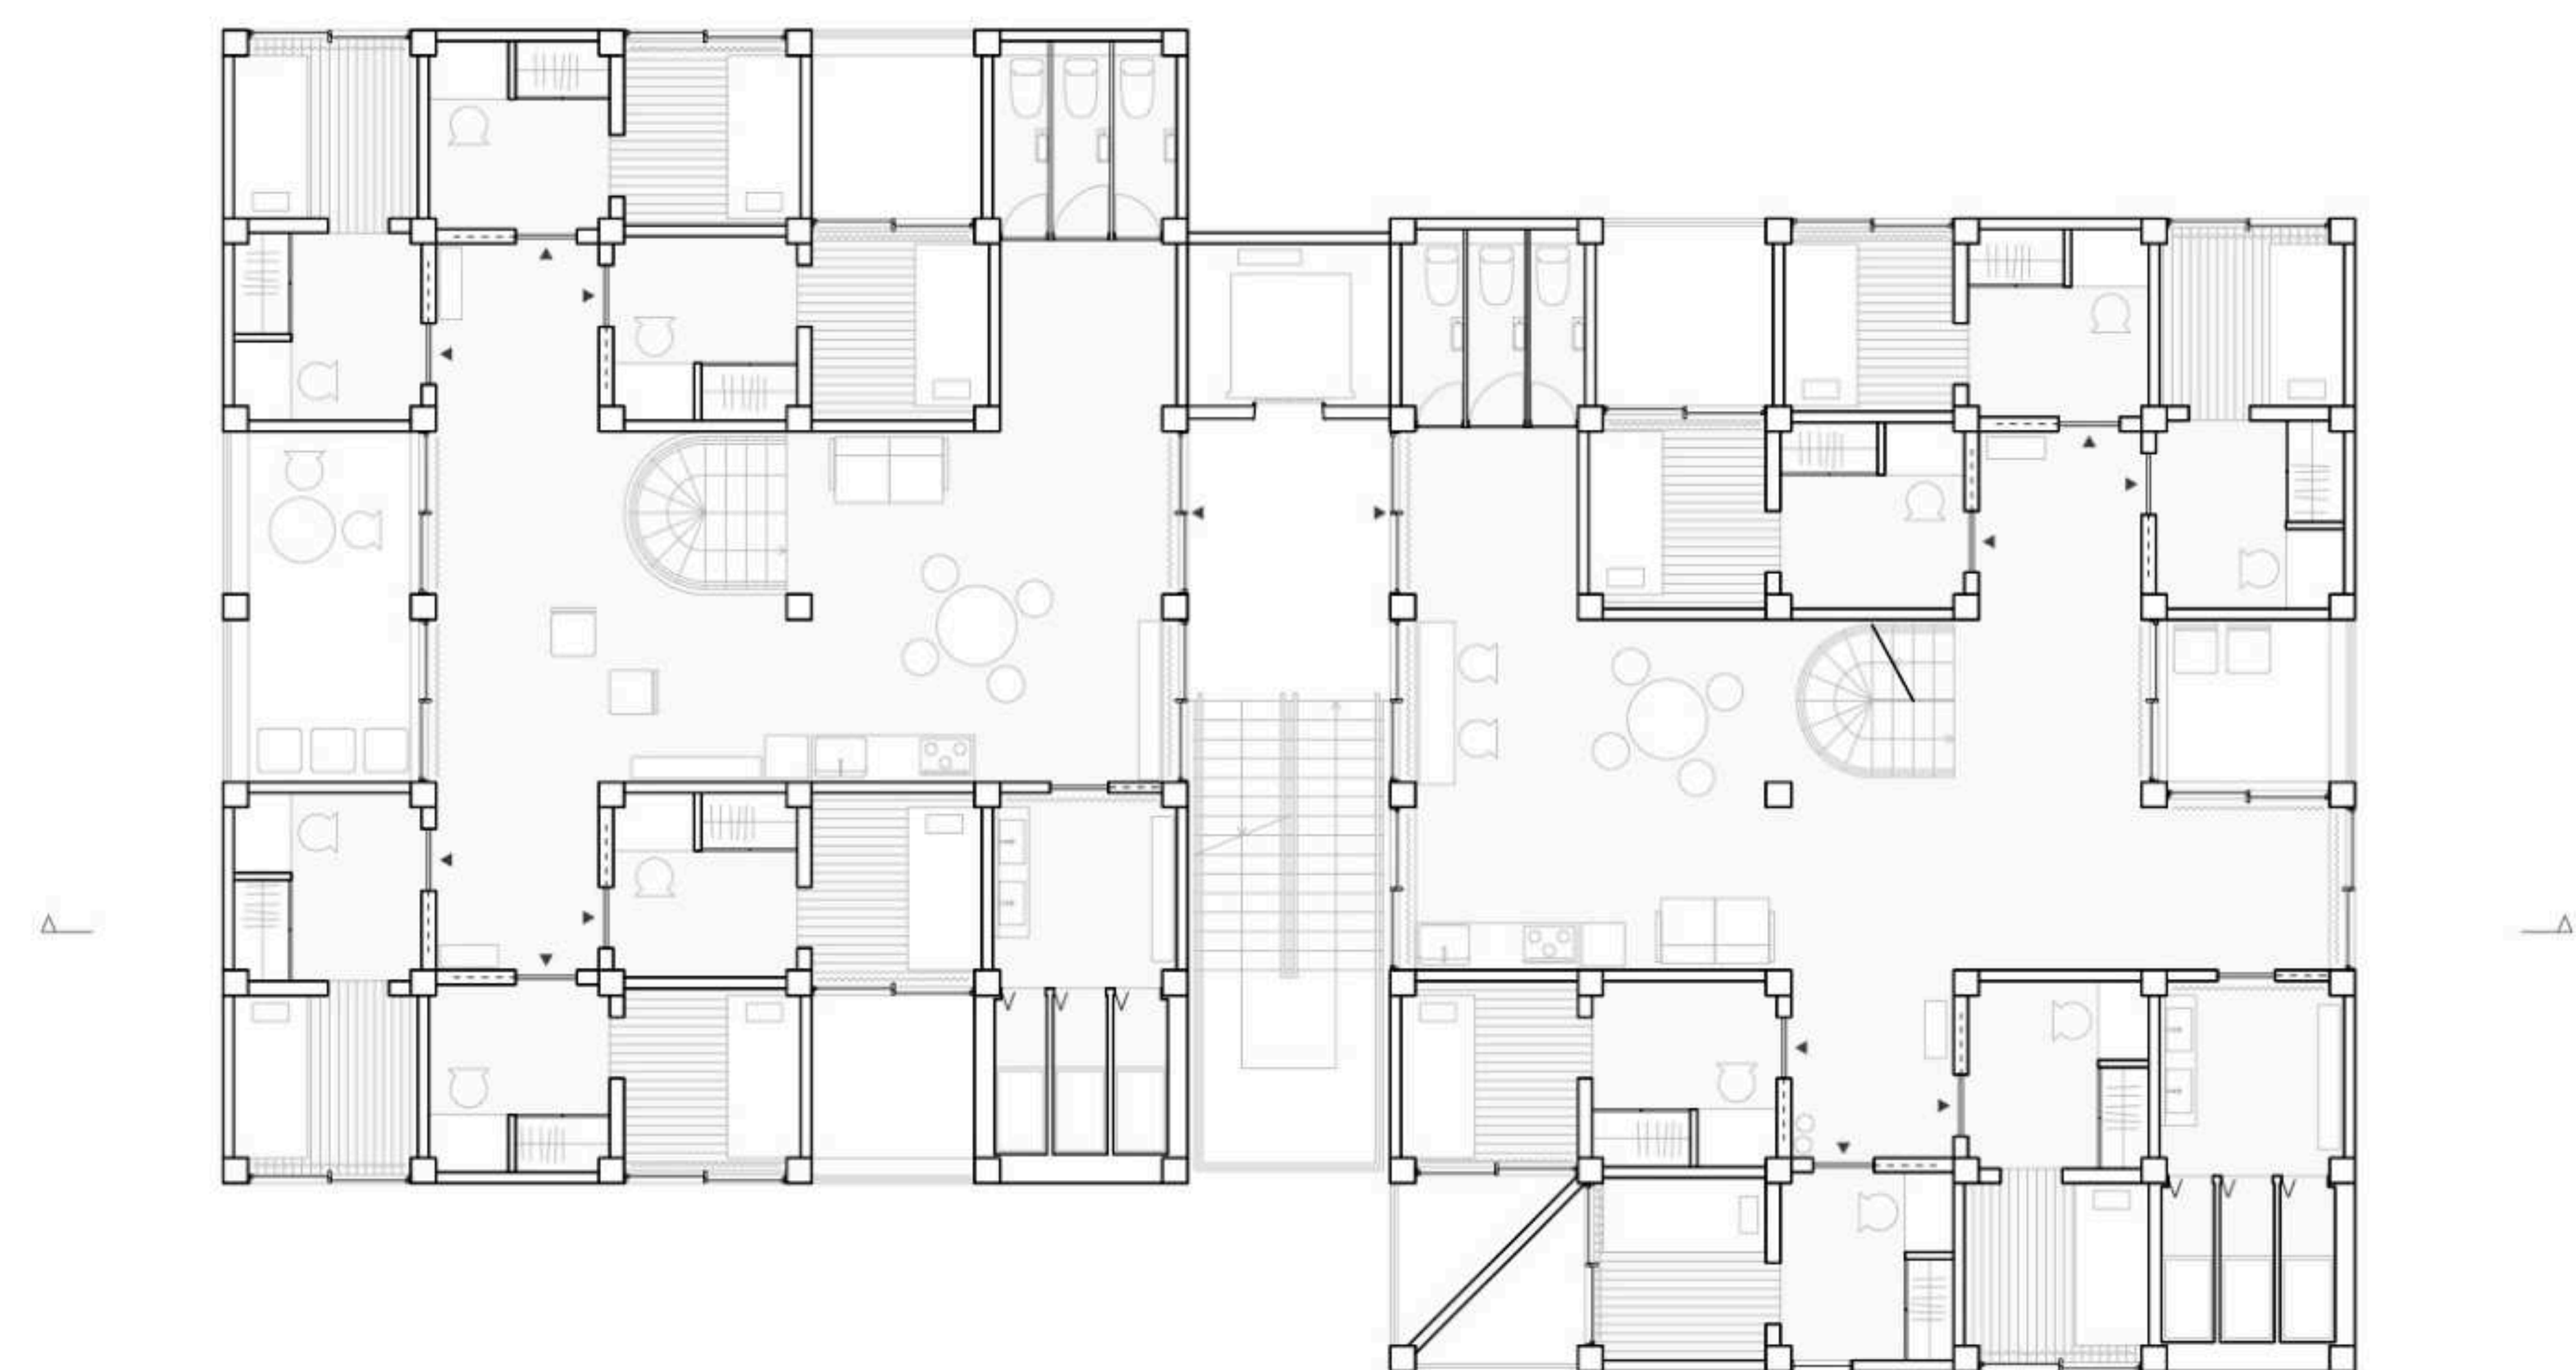

1/200 3F Plan Drawing

コンクリートの列柱と斜面

実際の敷地は、東西に 2m 近くの高低差があり、ゆるやかな傾斜をもつ残留土の空き地である。


一方で、敷地の東側には既存の擁壁がそびえている。この自然のような大地の露出と、土木構造物との対比関係と共存関係が、この敷地の持っている最大の特長であり個性であると考えた。


これをもとに、明確なグリッドを持つ建物の地階部分は、土木構造物のような言語と、地面から直接立ち上がったような列柱をベースにした遺跡のような空間で構成されており、上記の関係を建築的な体験へと昇華させている。

Concrete Colonnade and Topography

The actual site is a vacant lot of residual earth with a gentle slope, featuring a difference in elevation of nearly two metres from east to west. On the eastern edge of the site, an existing retaining wall rises prominently. The contrast and coexistence between this exposed terrain — raw and almost natural in character — and the civil engineering structure was understood as the most distinctive and defining quality the site has to offer.

Drawing from this reading, the basement level of the building — which otherwise follows a clear grid — is composed as a ruin-like space grounded in a vocabulary akin to civil infrastructure, with colonnades that appear to rise directly from the earth. In doing so, it elevates the relationship described above into an architectural experience.

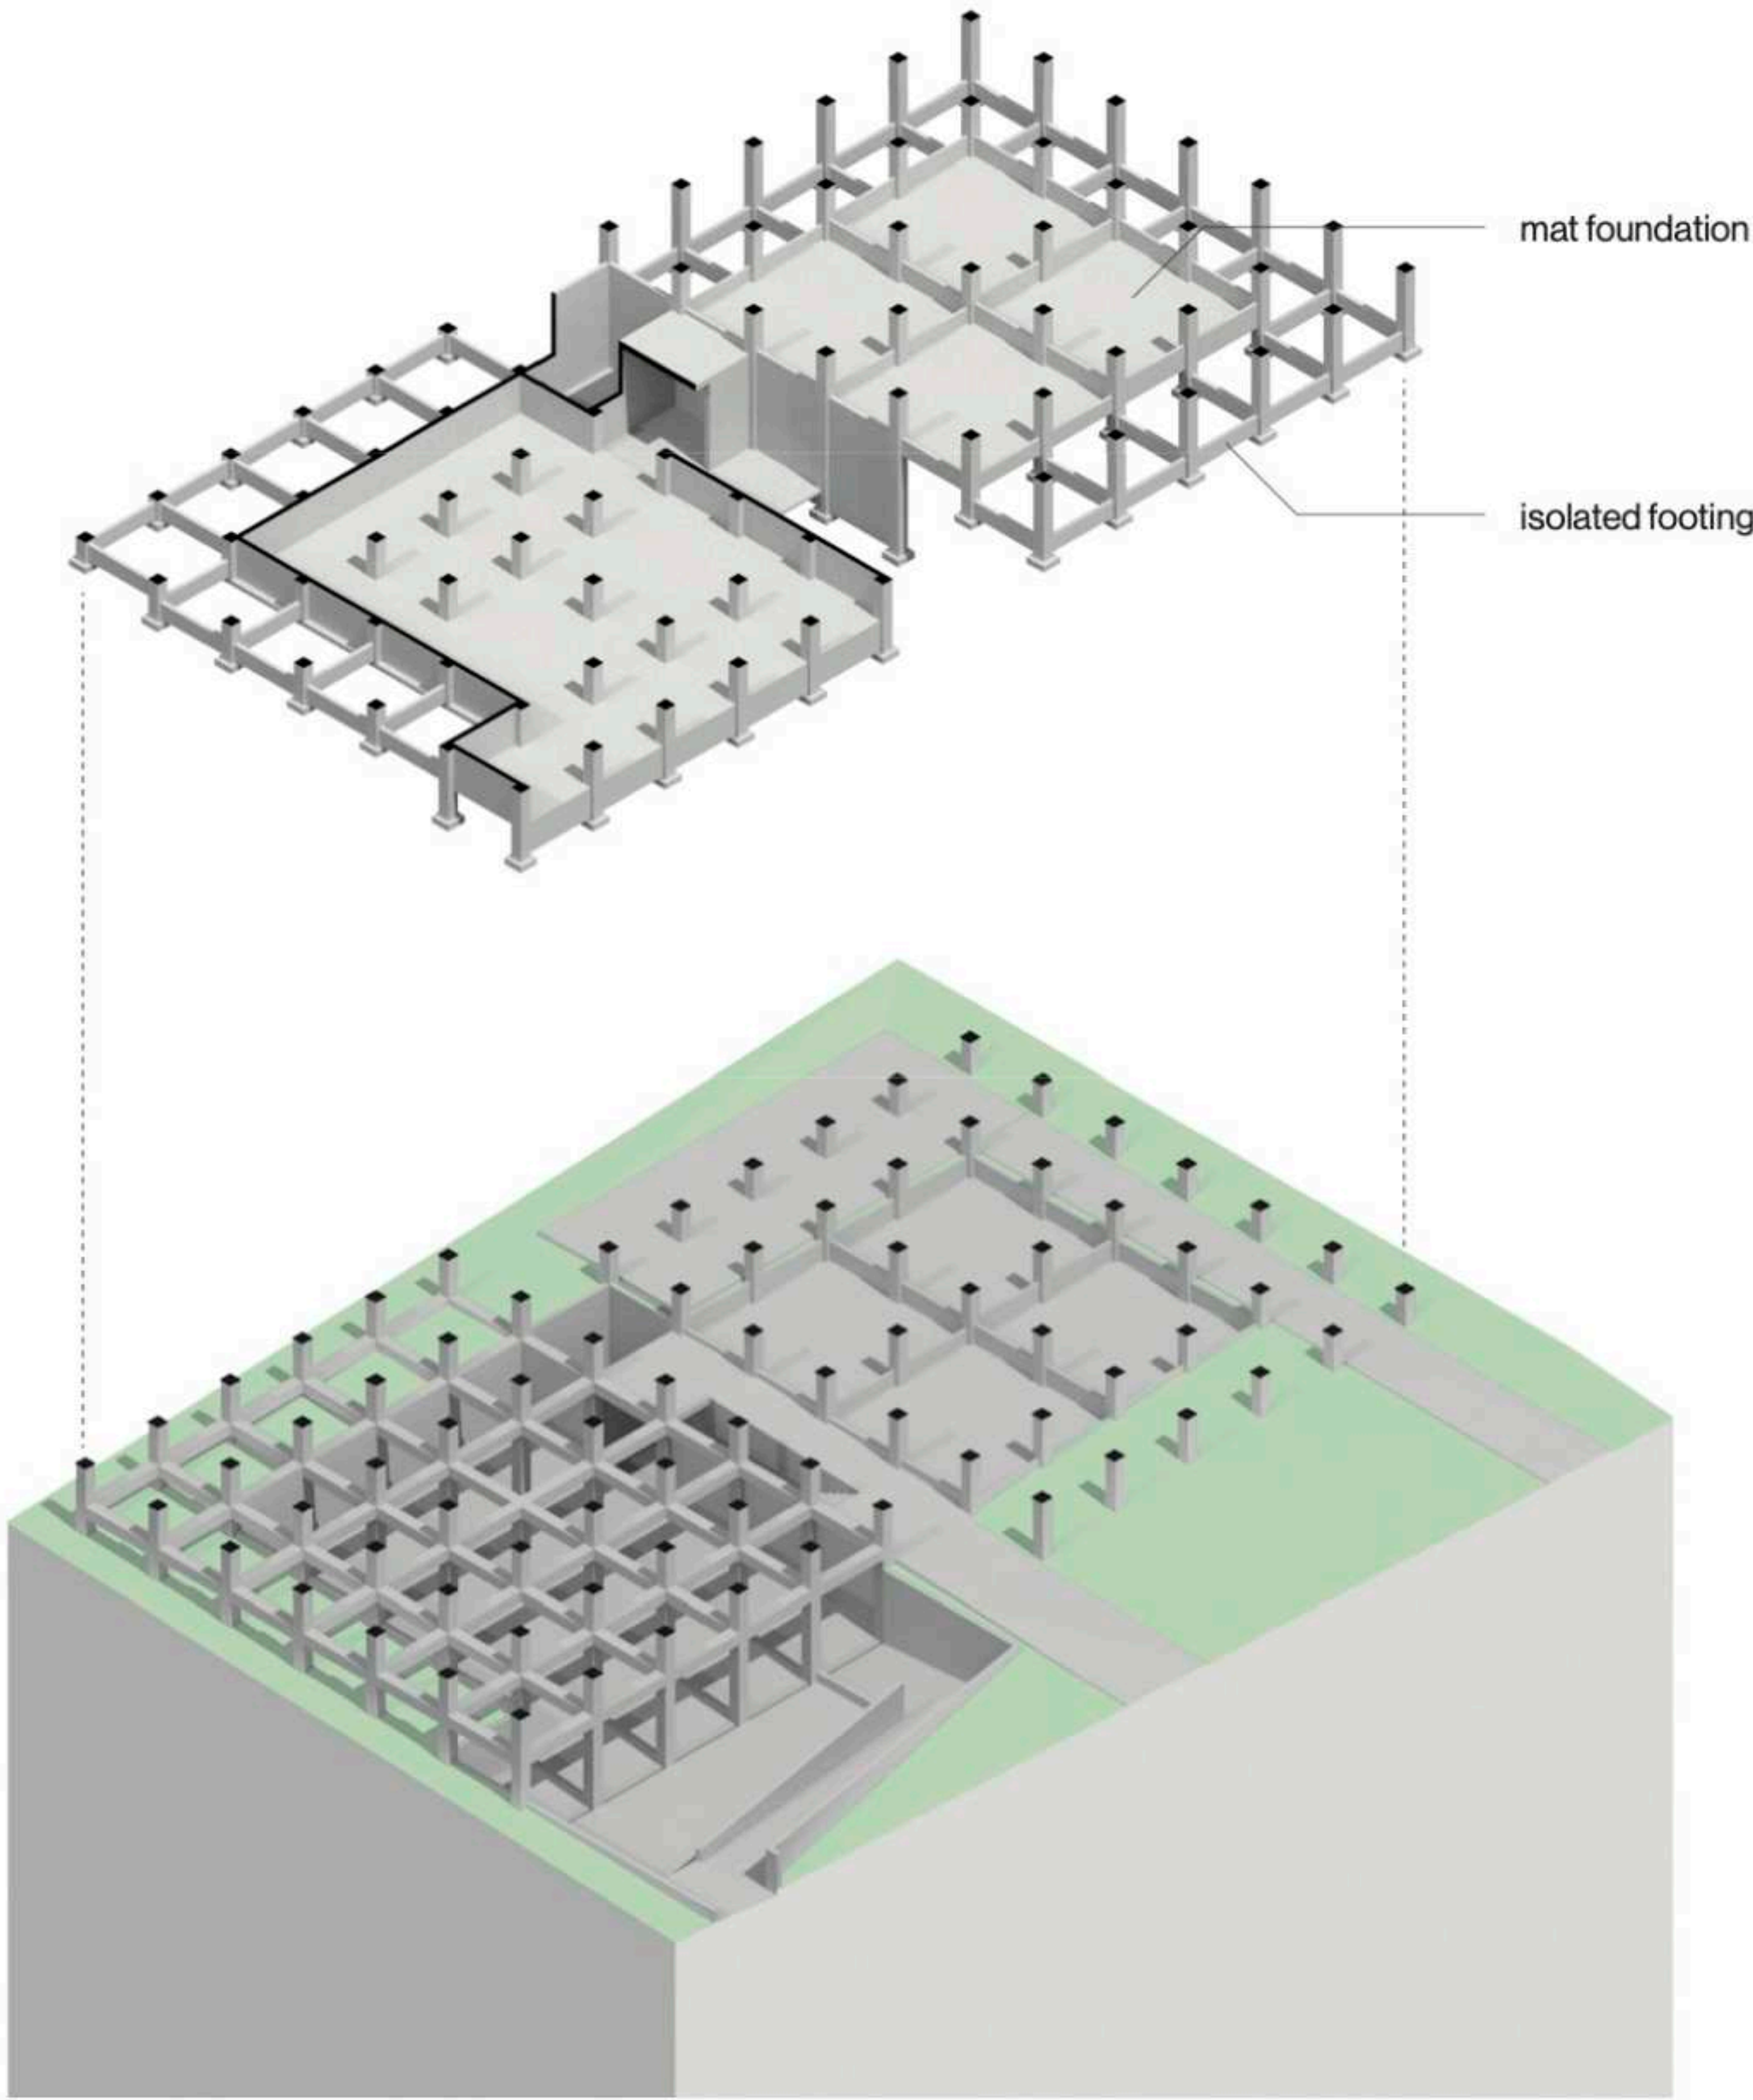

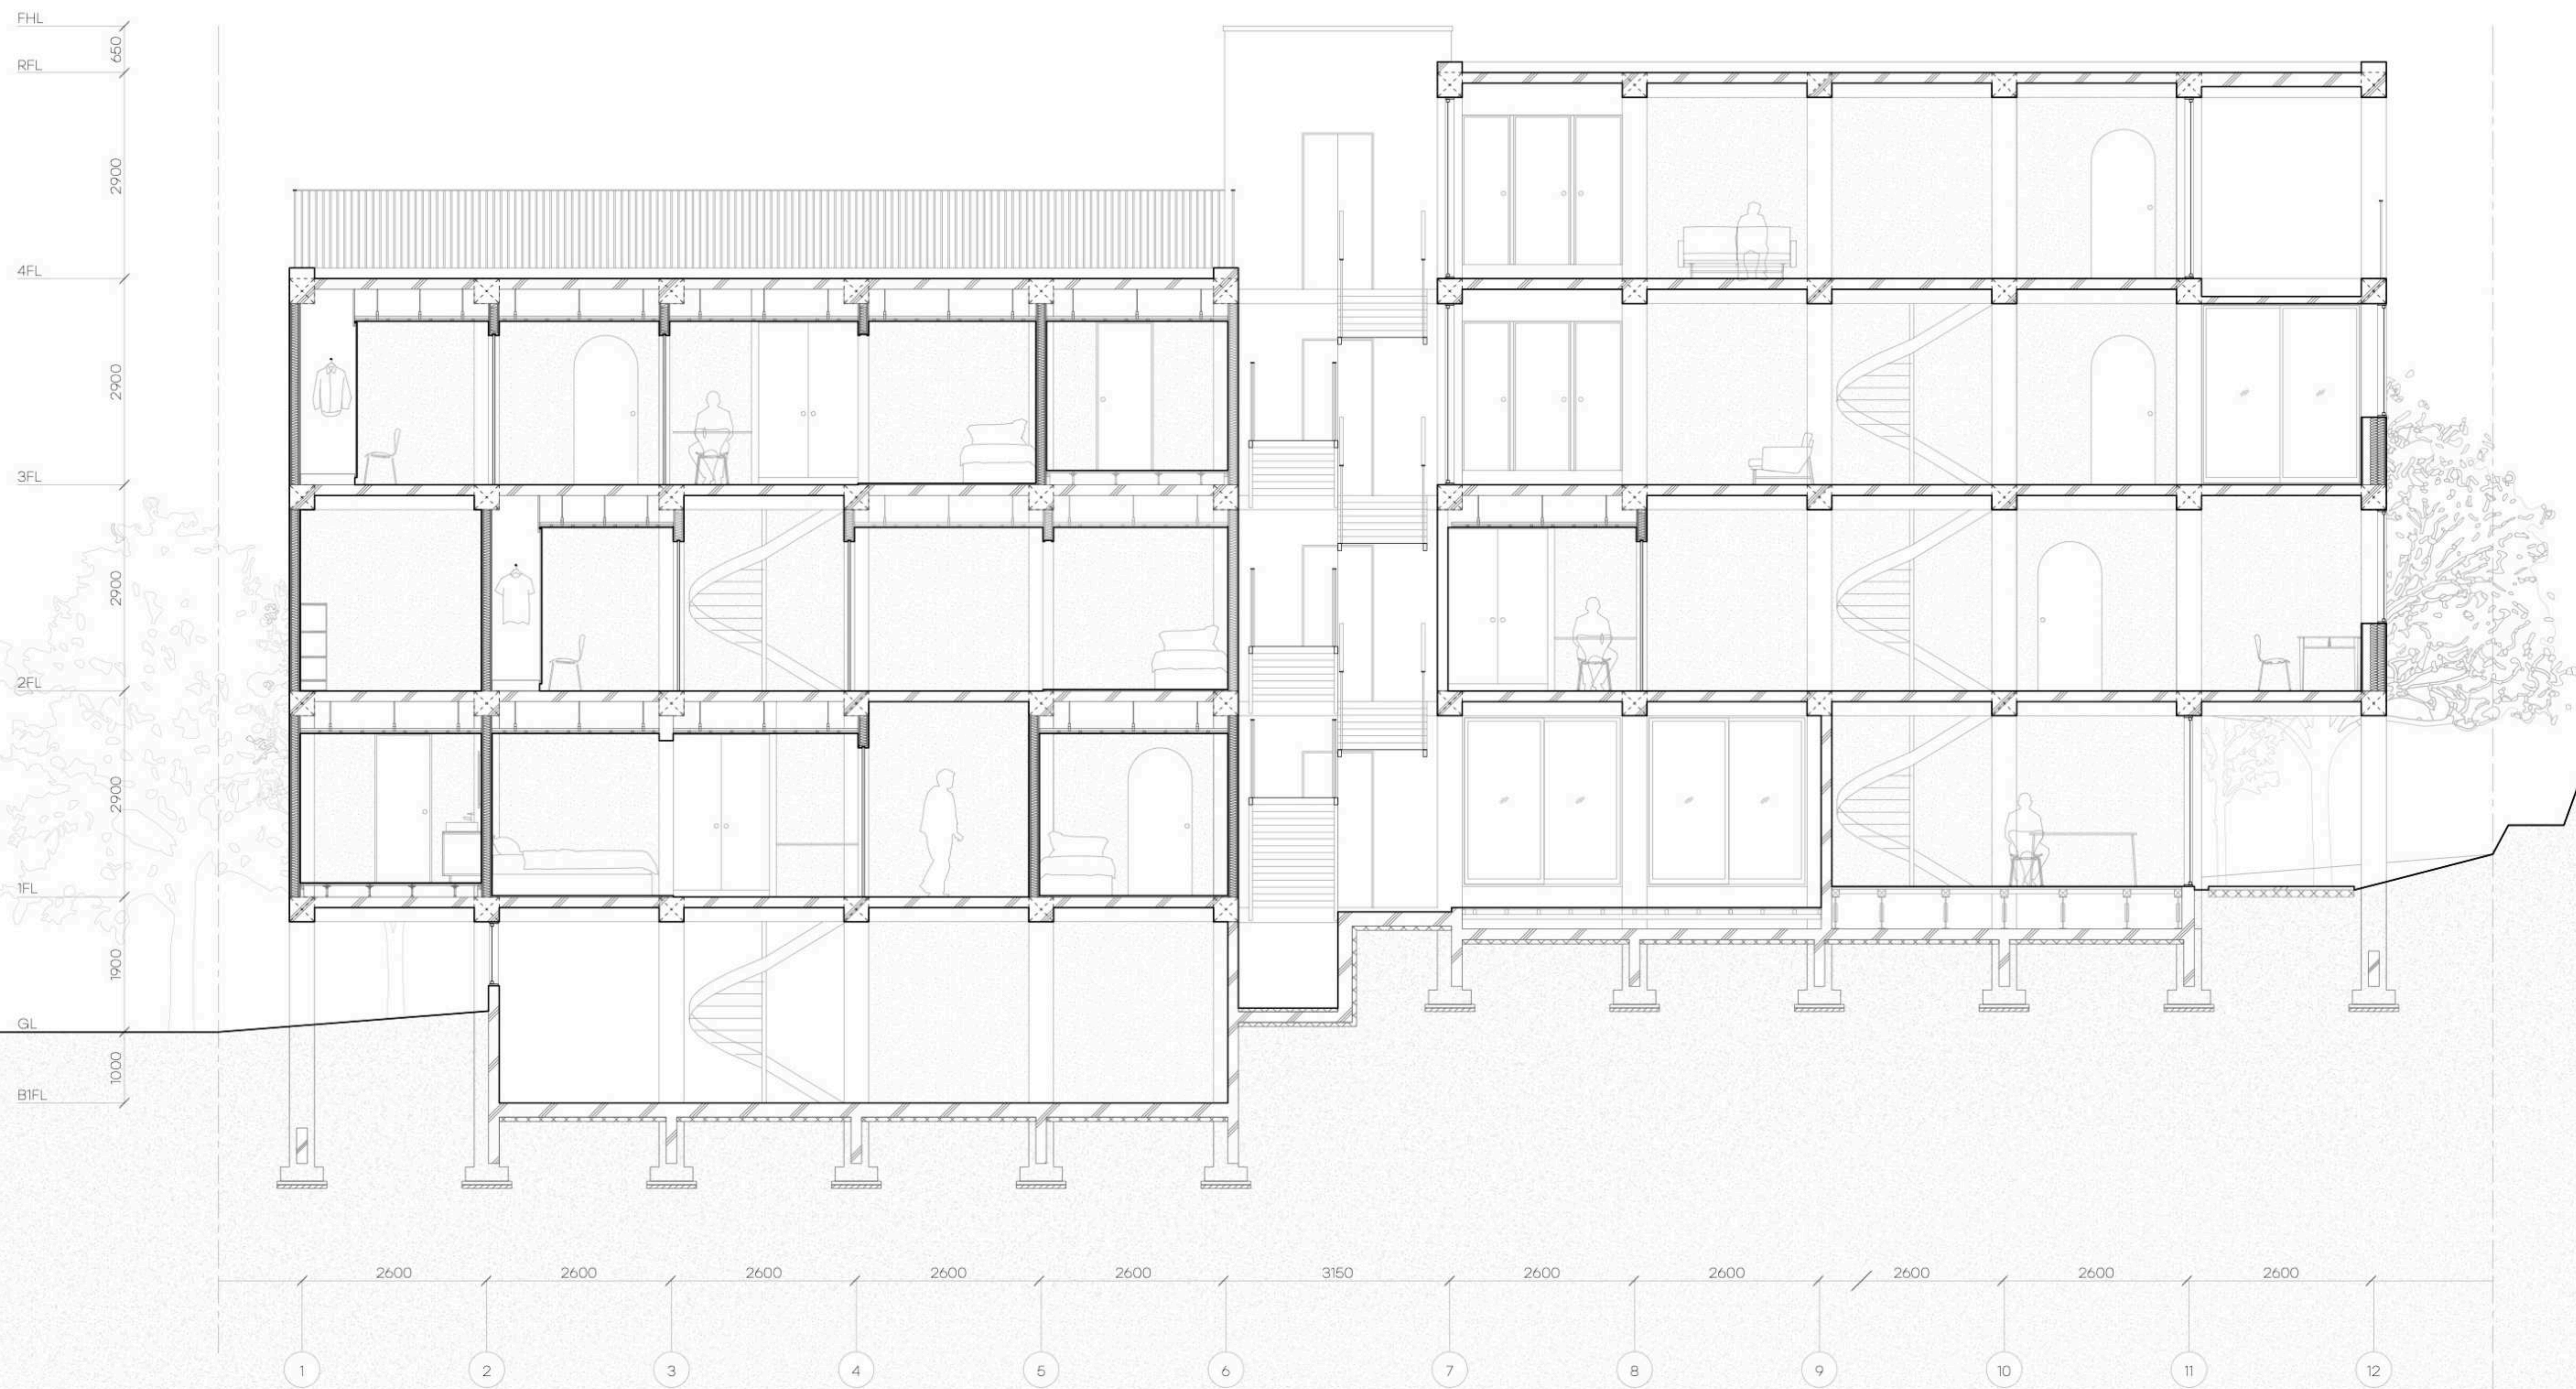



設計条件

東京都神田神保町の中心部に位置するブックカフェ併設のオフィスの計画である。この町は古くから古書店が立ち並ぶ世界一の本の街であると同時に、出版やメディア関連の業種が中心となるオフィス街でもある。

全体としては、古書店街の個性ある街の魅力を高めるため、他の店舗との連続性店先や道路のパブリックな空間との関係性を大切にすることが求められている。

オフィスフロアは出版・メディア関係の貸しテナントとし、低層部は書店とカフェを組み合わせたブックカフェを設け、動線や機能はオフィスからは独立させる。また、敷地内西側には既存の地下鉄駅の出入口があり、同位置に出入口の機能を維持する計画とする。

Design Conditions

This project is a proposal for an office building with an integrated book café, located in the heart of Jinbōchō, Chiyoda-ku, Tokyo. The district has long been renowned as the world's greatest concentration of secondhand bookshops, while also functioning as an office quarter dominated by publishing and media-related industries.

In response to the character of the area, the design is required to enhance the distinctive urban appeal of the antiquarian booksellers' street by giving careful consideration to continuity with neighbouring storefronts and the relationship between the building and the public realm of the street.

The upper office floors are designated as leasable tenant space for publishing and media companies, while the lower levels house a book café combining a bookshop and café, with circulation and functions kept independent from those of the office.

In addition, the entrance to an existing subway station is located on the western edge of the site, and the plan provides for the preservation of this access point in its current position.

設計の手がかり

現代の日本の都市空間は、私有されて立ち入れない空間と、消費行動のための空間で満ちている。公共的な歩道を歩いても、その空間を輪郭づけているビル群のファサードは市民からは閉ざされている。

そこでこの計画では、都市の公共空間と内部の私有空間の境界である建築のファサードに領有の中間領域を設けることで、新たな都市景観と、新たな都市体験をもたらすことを目指した。

空間の図式 建築の構成

敷地北側の大通りは、書籍を店の入り口の前に並べて販売する露店のような形式をとっている古書店が多い。神保町は、地階のレベルでは街を歩きながら消費行動をする開かれた街の姿がある。

この街のそうした伝統的な活動を継承し、新たな体験として進化させるため、人々を内部に引き込み、そして上層階に引き上げる立体広場を北側のファサードに設けることを考える。これらは直通階段を有するオフィスにとってのテラスでもあり、屋外避難階段の動線にもなる。

Design Clues



Contemporary urban space in Japan is dominated by privately owned areas inaccessible to the public and spaces designed solely for consumption. Even when walking along a public pavement, the facades of the buildings that define and enclose that space remain closed off from the citizens who inhabit the city.


In response, this project seeks to introduce a new urban landscape and a new quality of urban experience by establishing an intermediate zone of appropriation within the building's facade — the threshold between the public space of the city and the private interior beyond.


Spatial Diagram — Architectural Organisation

Along the main boulevard to the north of the site, many secondhand bookshops adopt a stall-like format, displaying their books on stands set out in front of the entrance. At street level, this city presents itself as an open, walkable district where people browse and engage in spontaneous consumption as they move through the city.

In order to inherit this traditional mode of urban activity and evolve it into a new form of experience, the proposal introduces a vertical plaza on the northern facade — one that draws people inward into the building and lifts them upward through its levels. These spaces also serve as terraces for the offices, which are equipped with direct staircase access, and simultaneously function as outdoor emergency evacuation routes.

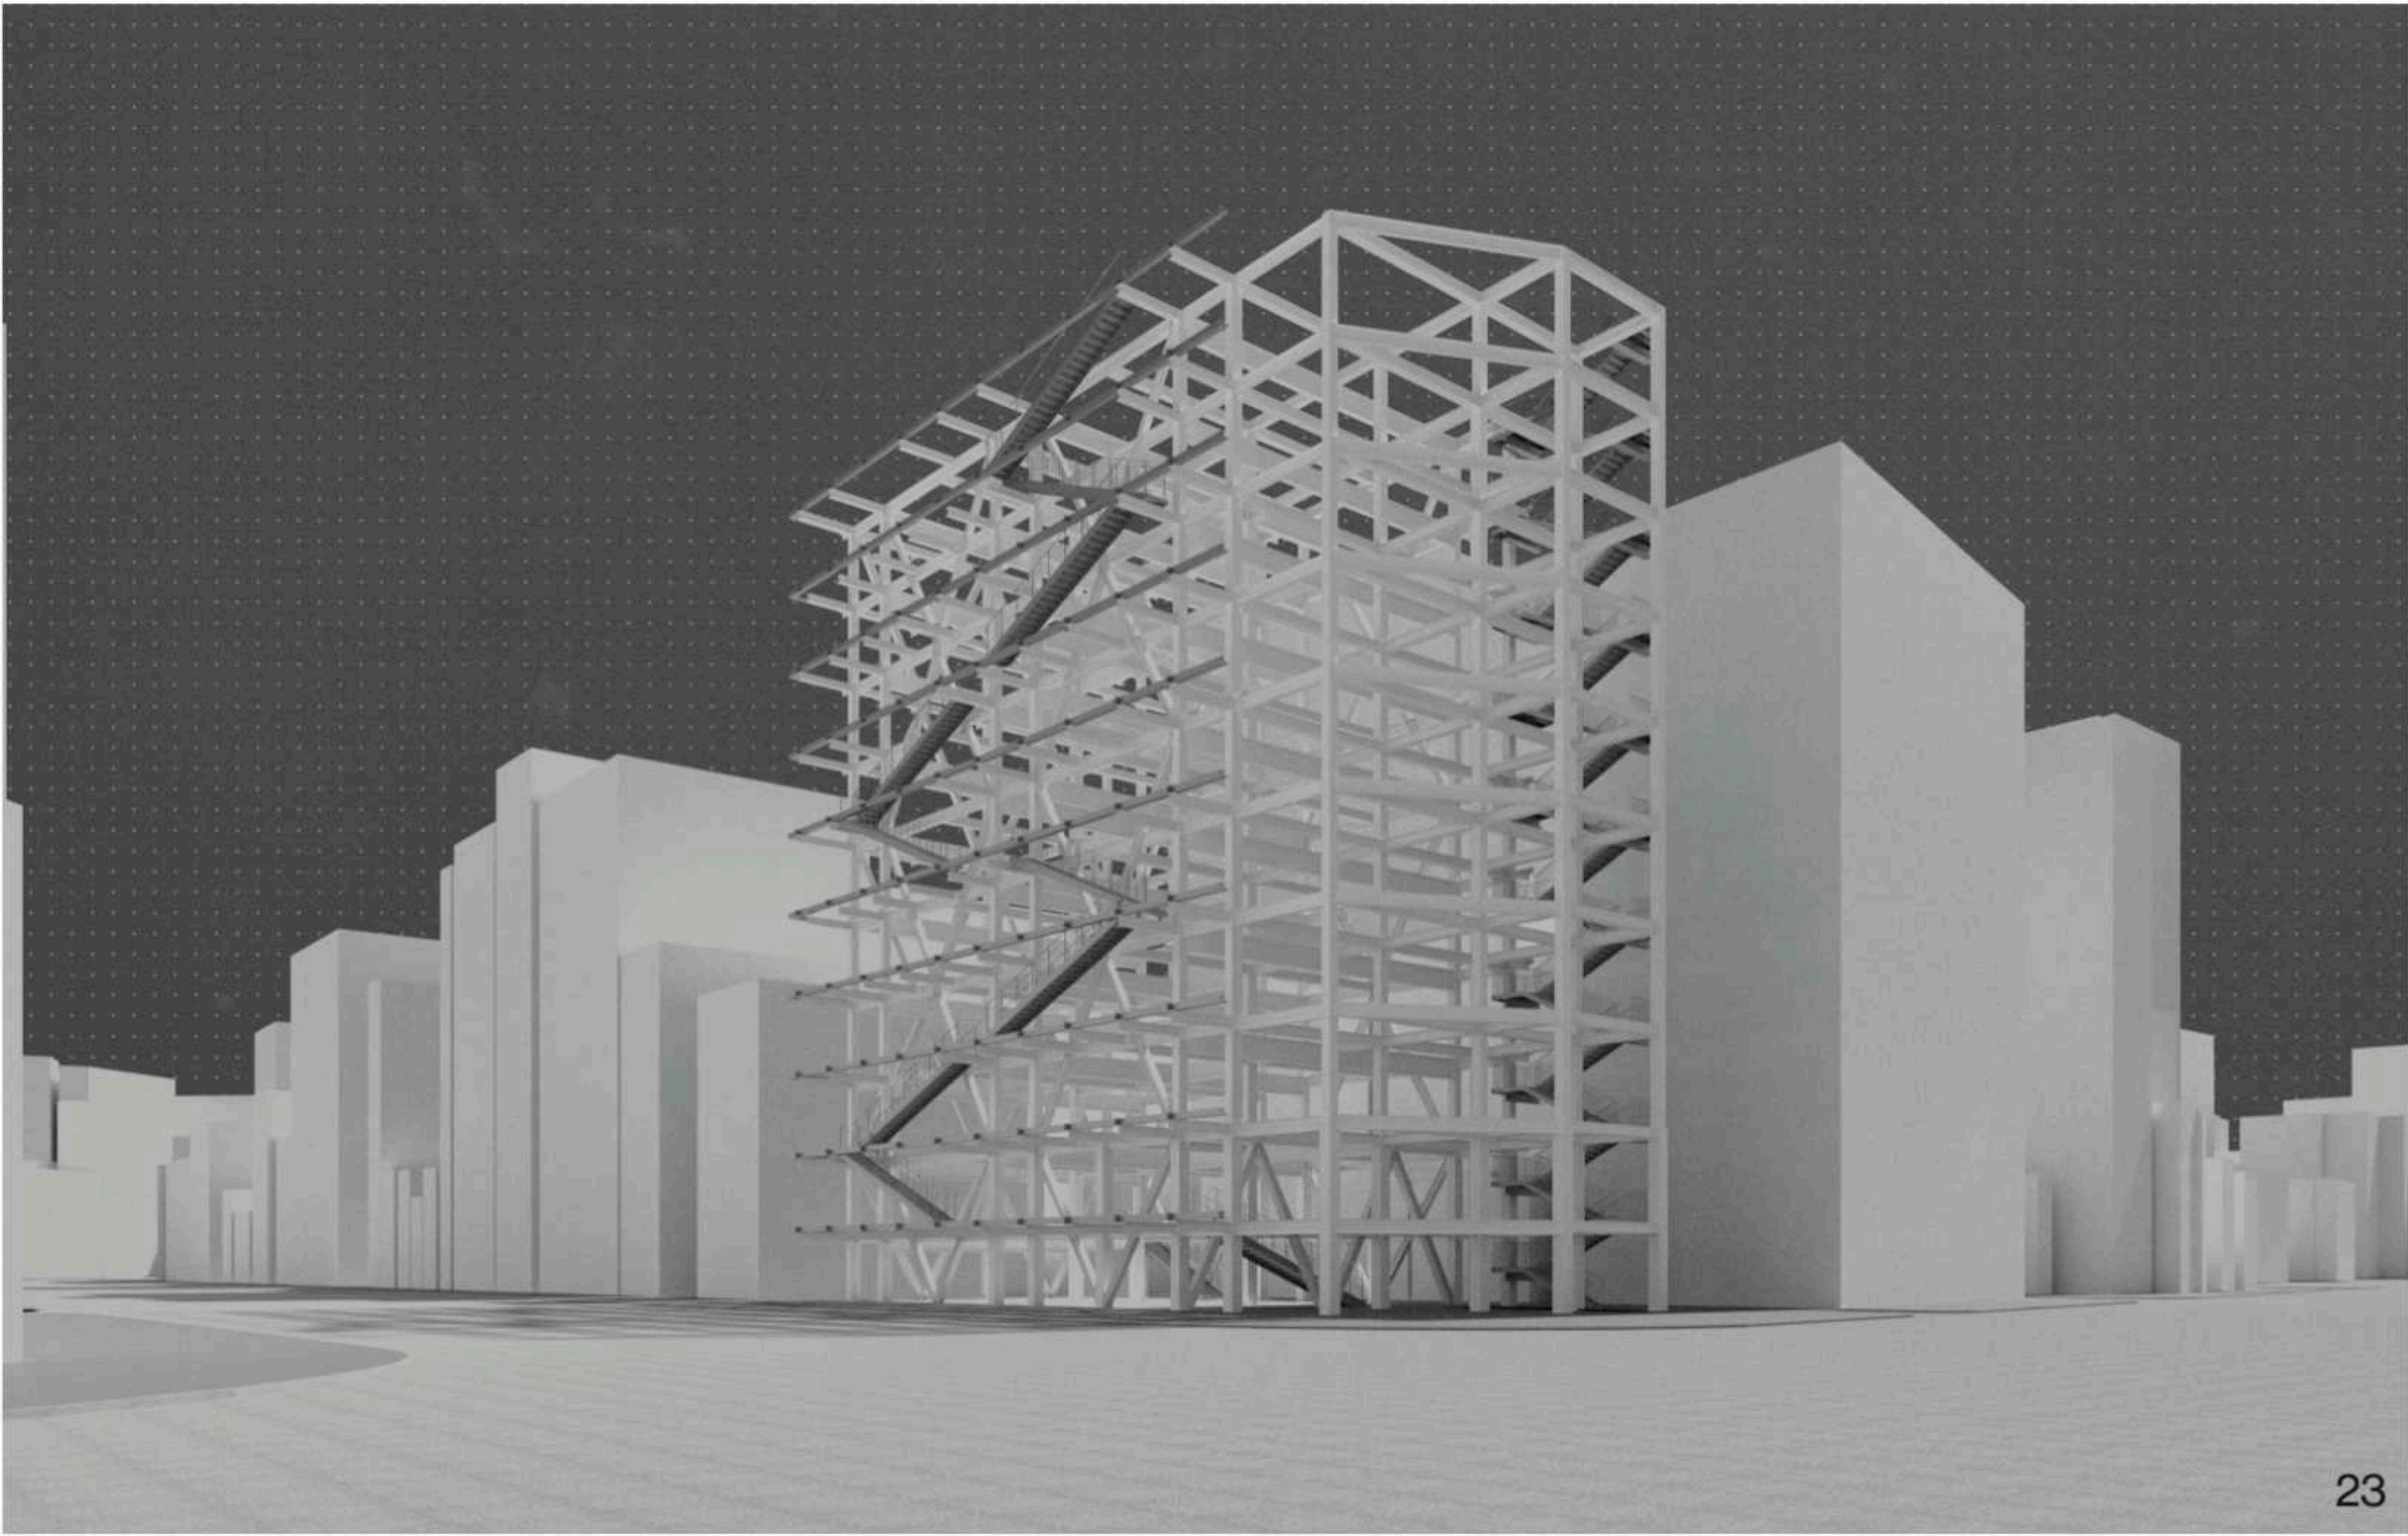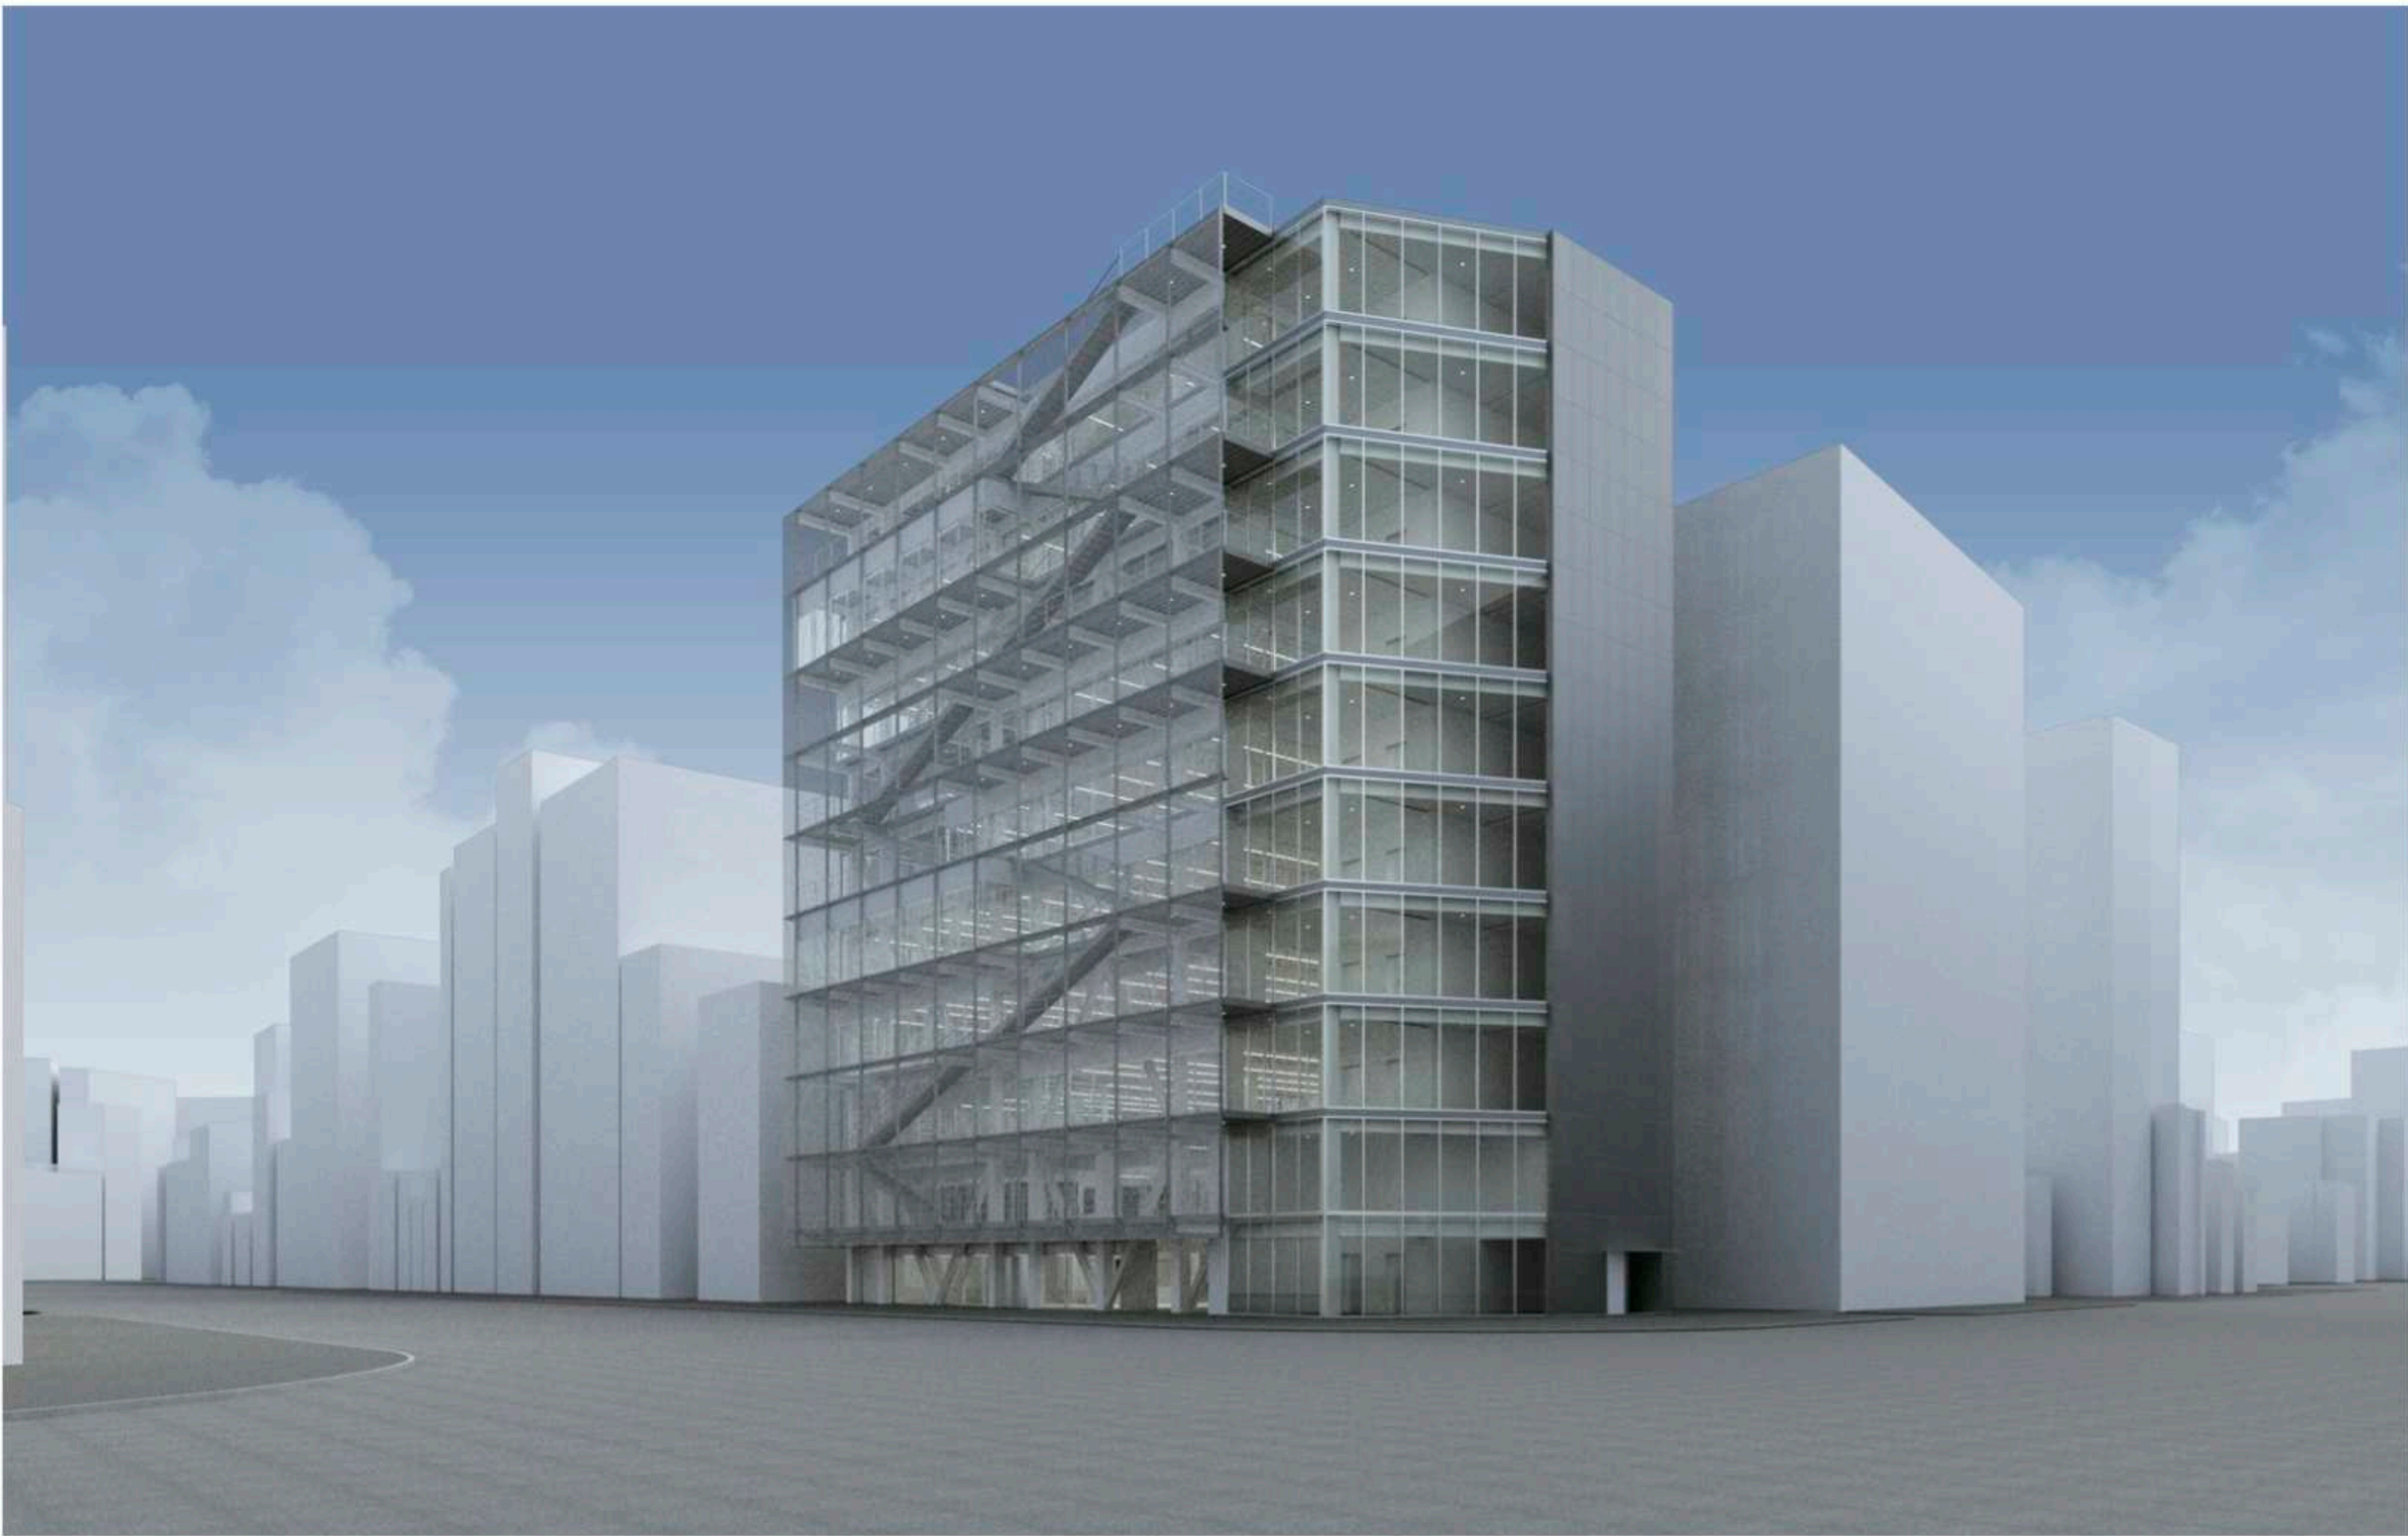

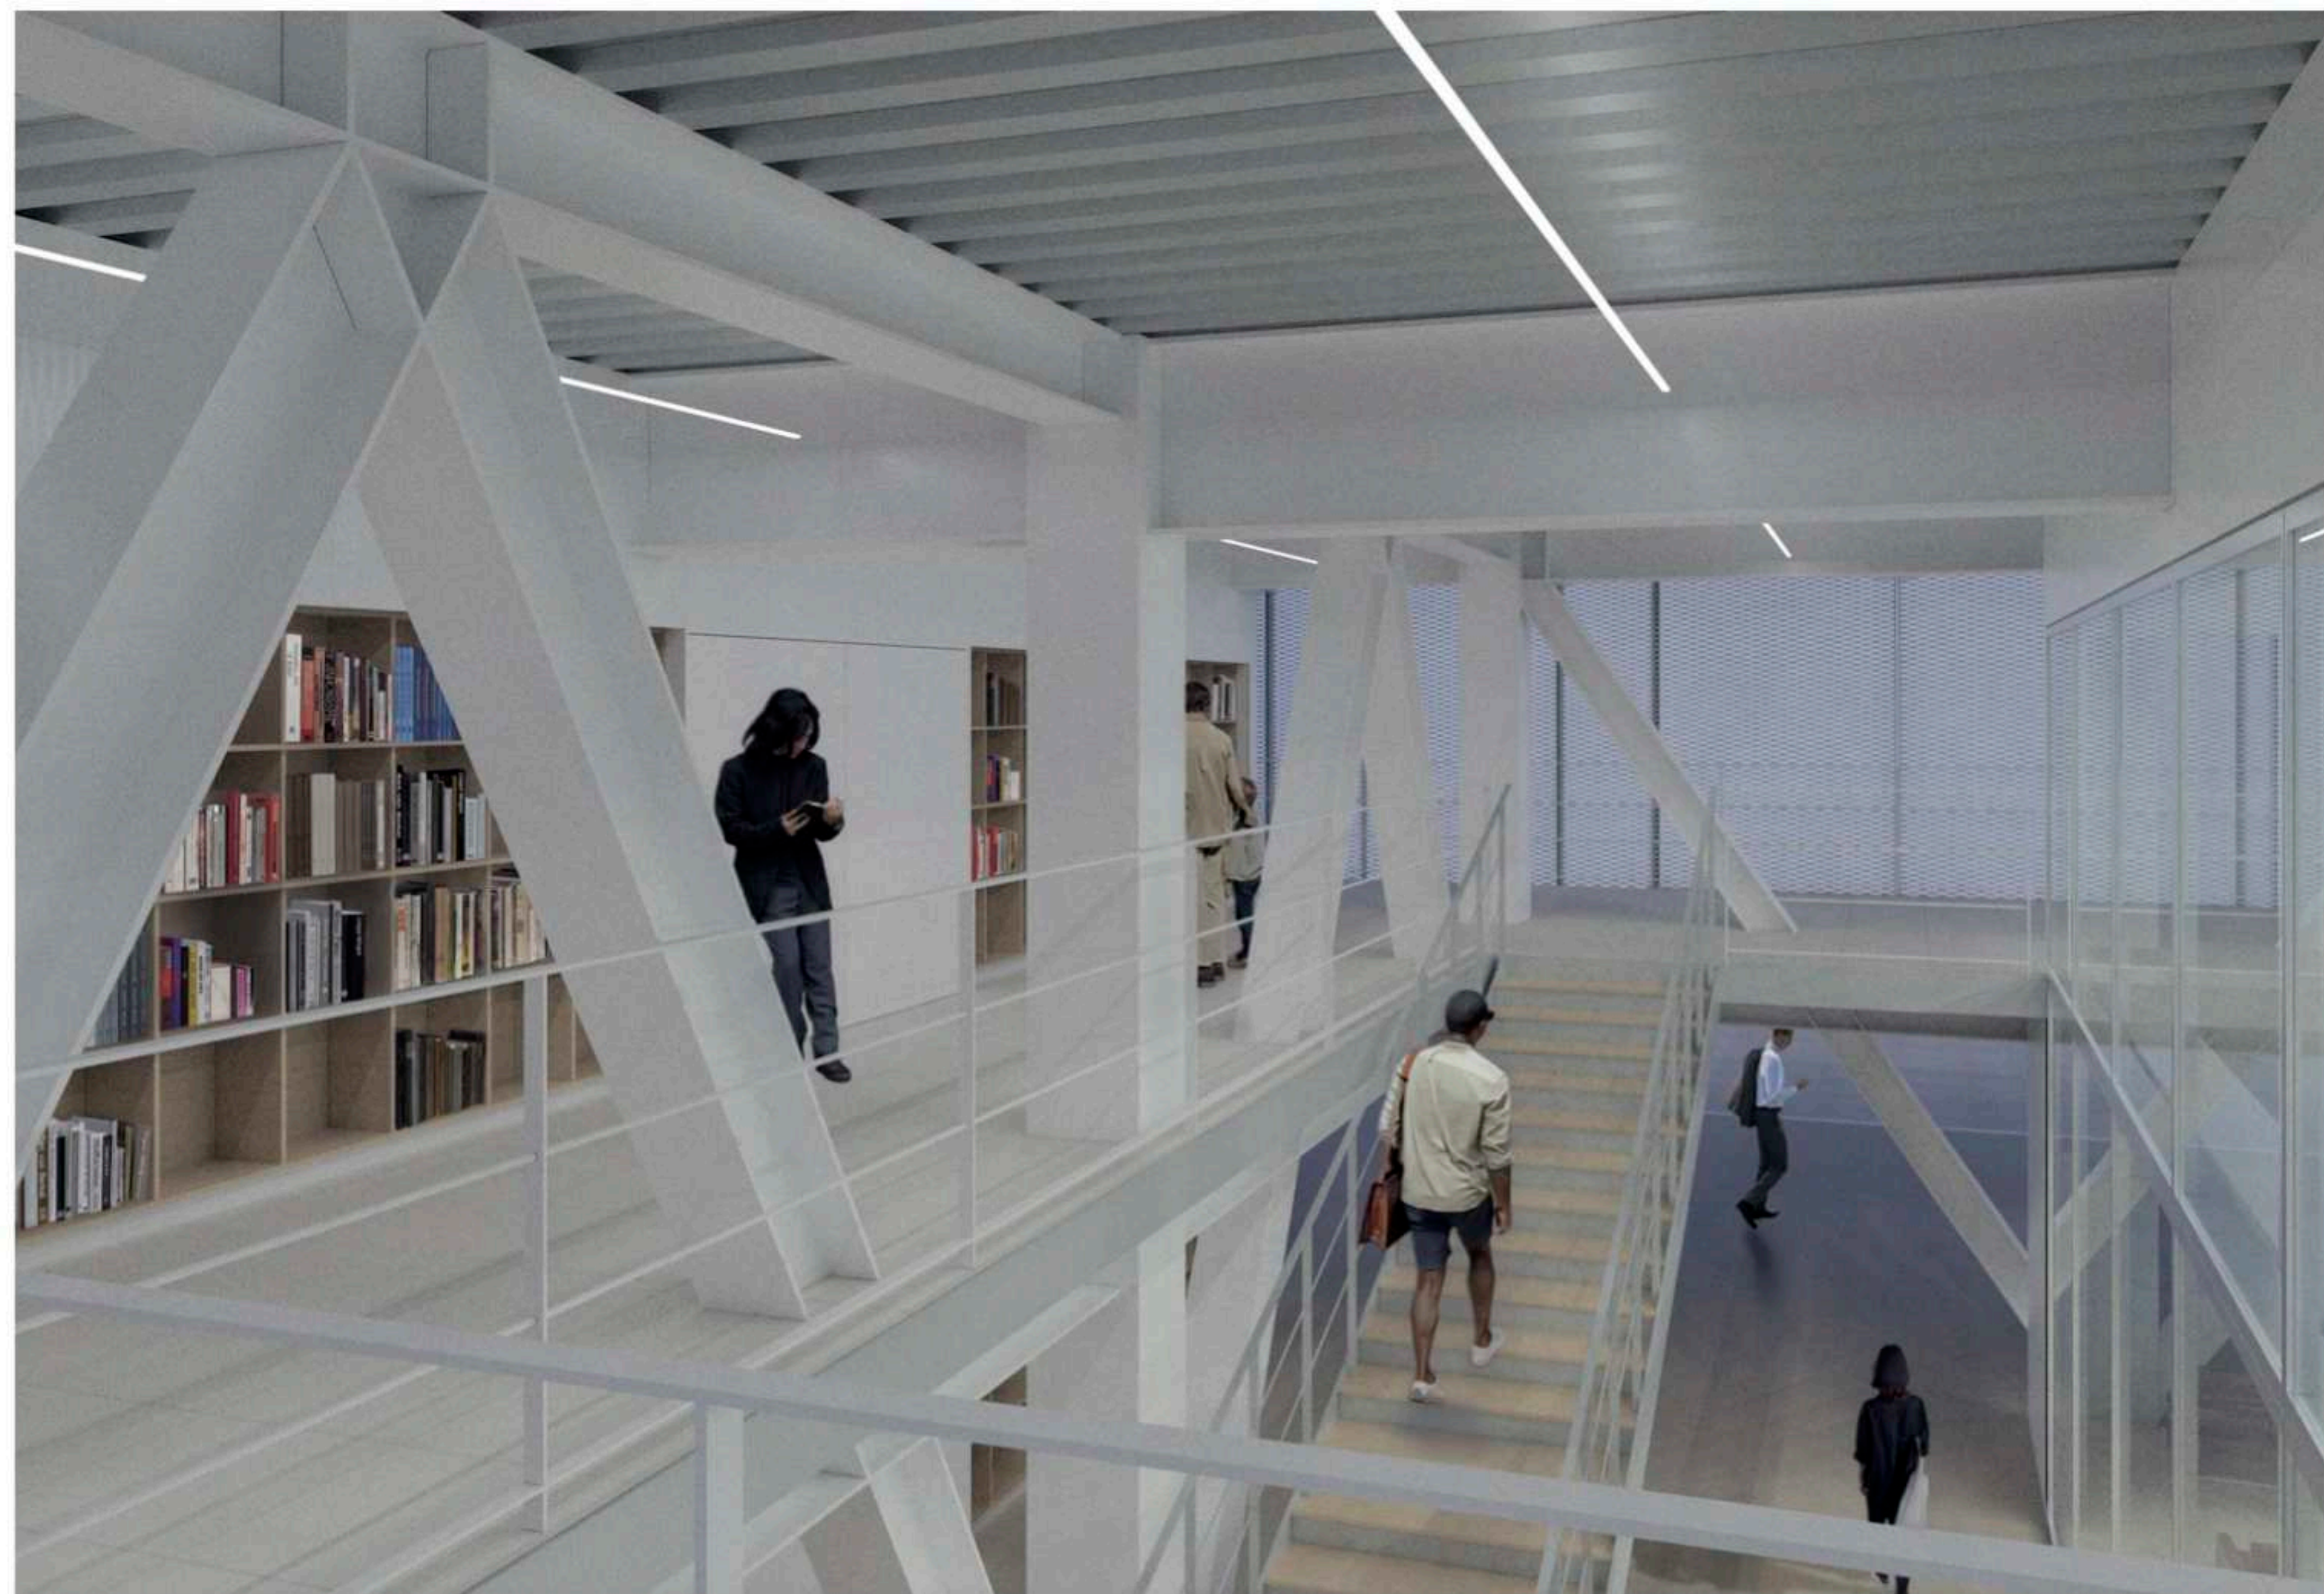

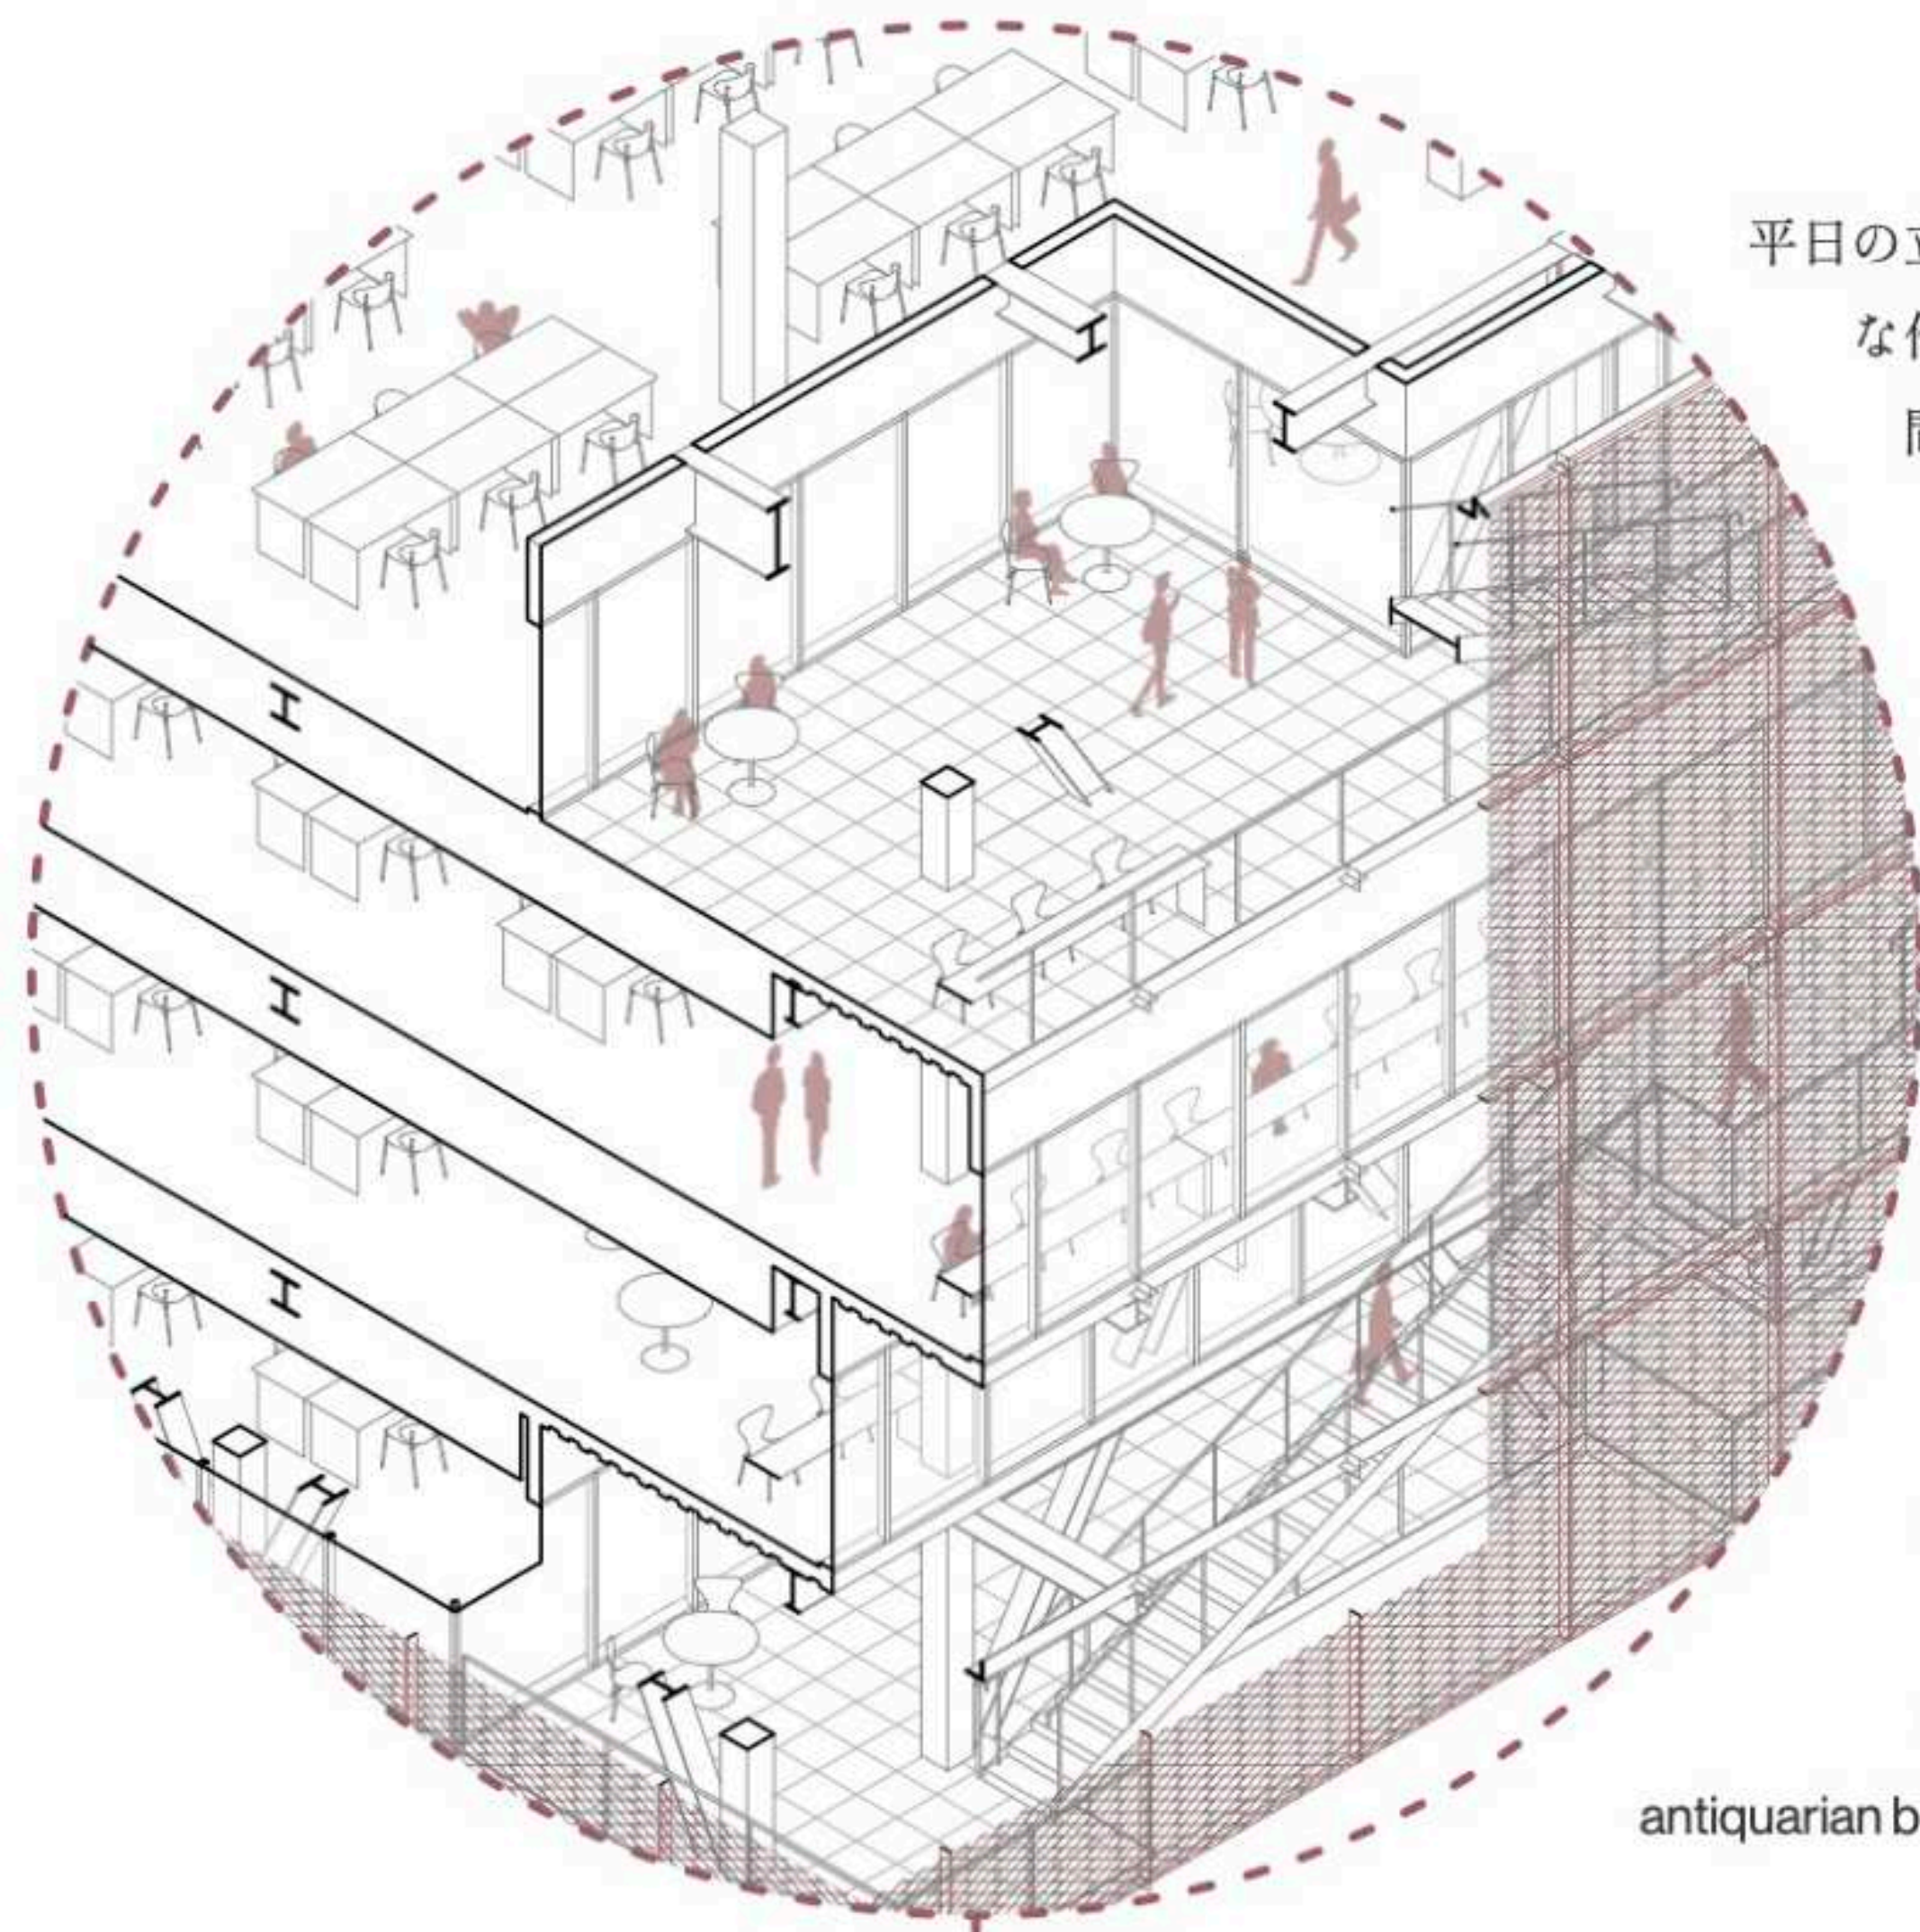

基準階

平日の立体広場（テラス）は、別フロアへの移動時だけでなく、オルタナティブな作業場所として、また、他企業との交流の場としても使用される。この空間は、オフィスワーカーにとっては働きながら都市の公共空間との交わりを絶たないバッファーとしても機能している。


休日の立体広場は、古書店街の訪問客の休憩場所や、書籍の購入者がその場で読書することができる自由な滞在空間として機能する。このように、日々の絶え間ない人々の活動は、この建築のファサードを形づくり、都市をもっと活き活きとした風景に作り替える。

Typical Floor

On weekdays, the vertical plaza — functioning as a series of terraces — is used not only as a means of moving between floors, but also as an alternative workspace and a venue for interaction between different companies and their employees. For office workers, this space also acts as a buffer, allowing them to remain connected to the public life of the city even while at work.

On weekends, the vertical plaza transforms into a place of rest for visitors to the antiquarian booksellers' district, as well as a relaxed space where those who have purchased books can linger and read at leisure.

In this way, the continuous and ever-changing activity of people across the course of each day gives form to the facade of the building, remaking the city into a more vivid and animated landscape.

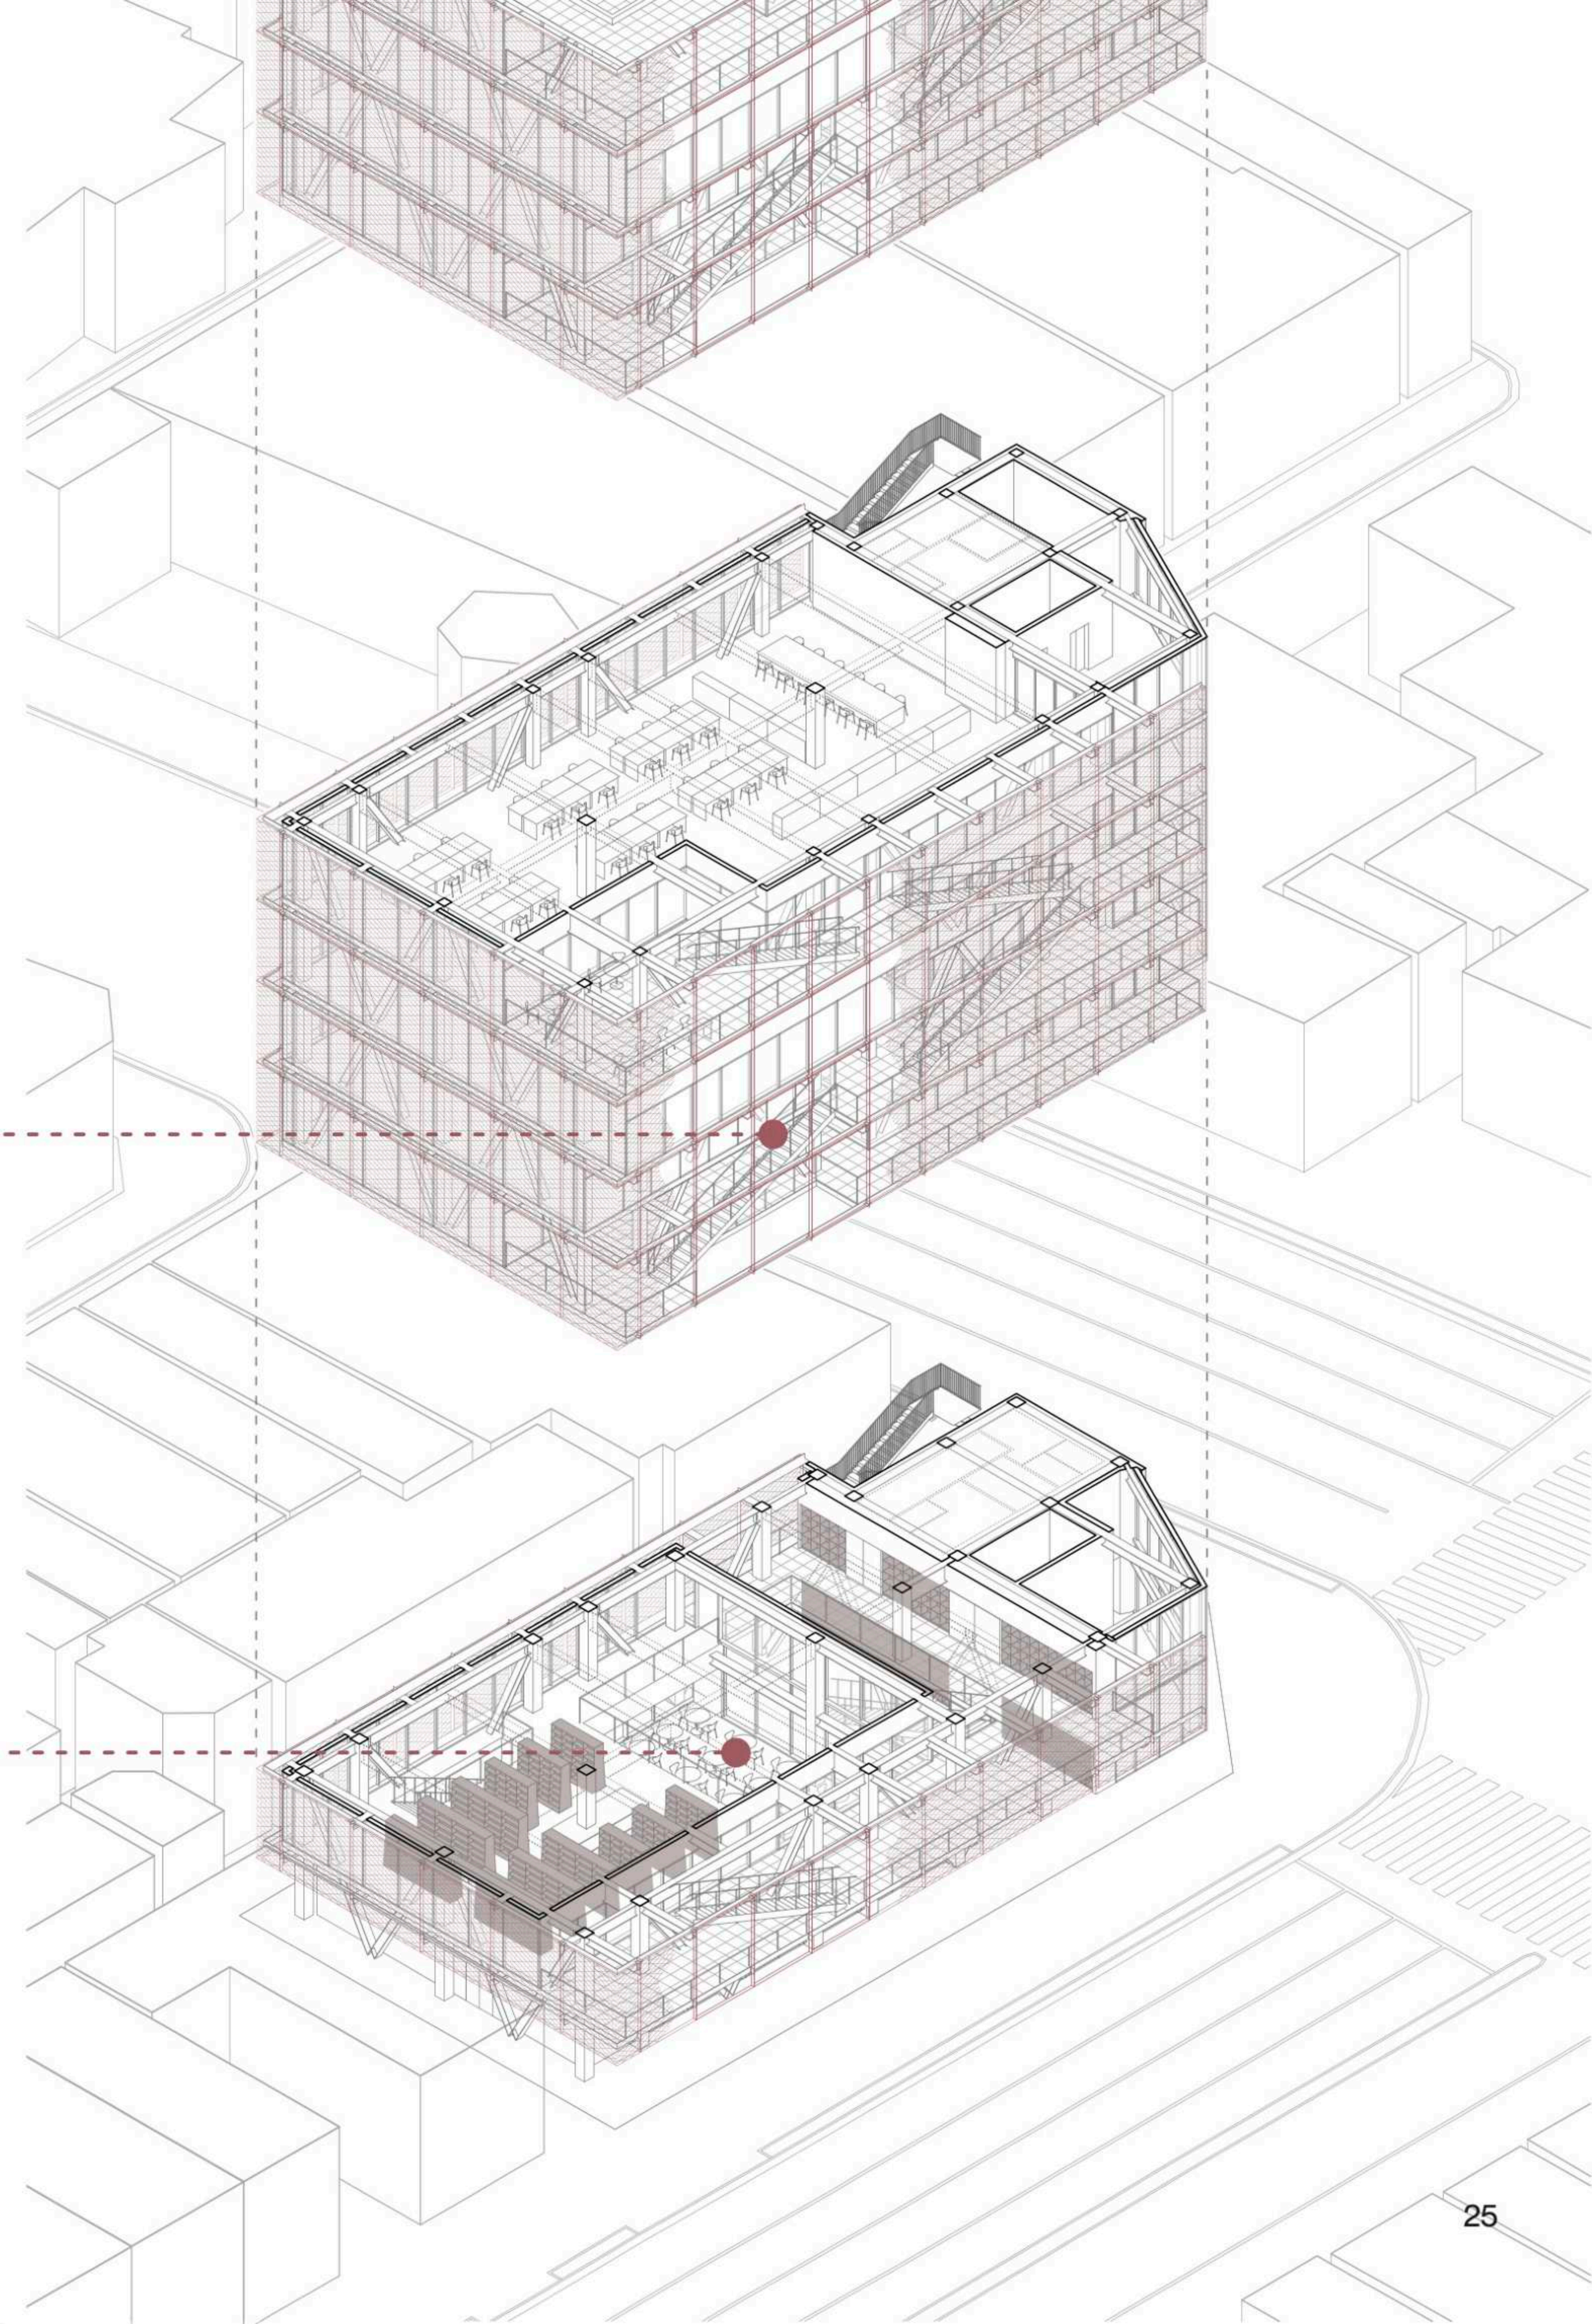


低層階


神保町に古くからある露店は、天候からの影響や書籍の保存などの難点が多い。そのため、低層階の書店は、屋内と半屋外に設けた。半屋外の書店部分は、大通りに直交する新たな路地をつくり、立体広場へ入り込む起点でもある。屋内の書店は、カフェ部分との接続を重視し、快適なブックカフェの滞在体験を提供している。

Lower Floors

The open-air stalls that have long been a fixture of Jinbōchō face considerable practical challenges, including exposure to the elements and the difficulty of preserving books in outdoor conditions. For this reason, the bookshop on the lower floors is divided between an indoor section and a semi-outdoor section.

The semi-outdoor portion creates a new alley running perpendicular to the main boulevard, serving as the point of entry into the vertical plaza. The indoor bookshop, by contrast, prioritises its connection to the café, offering a comfortable and immersive book café experience.

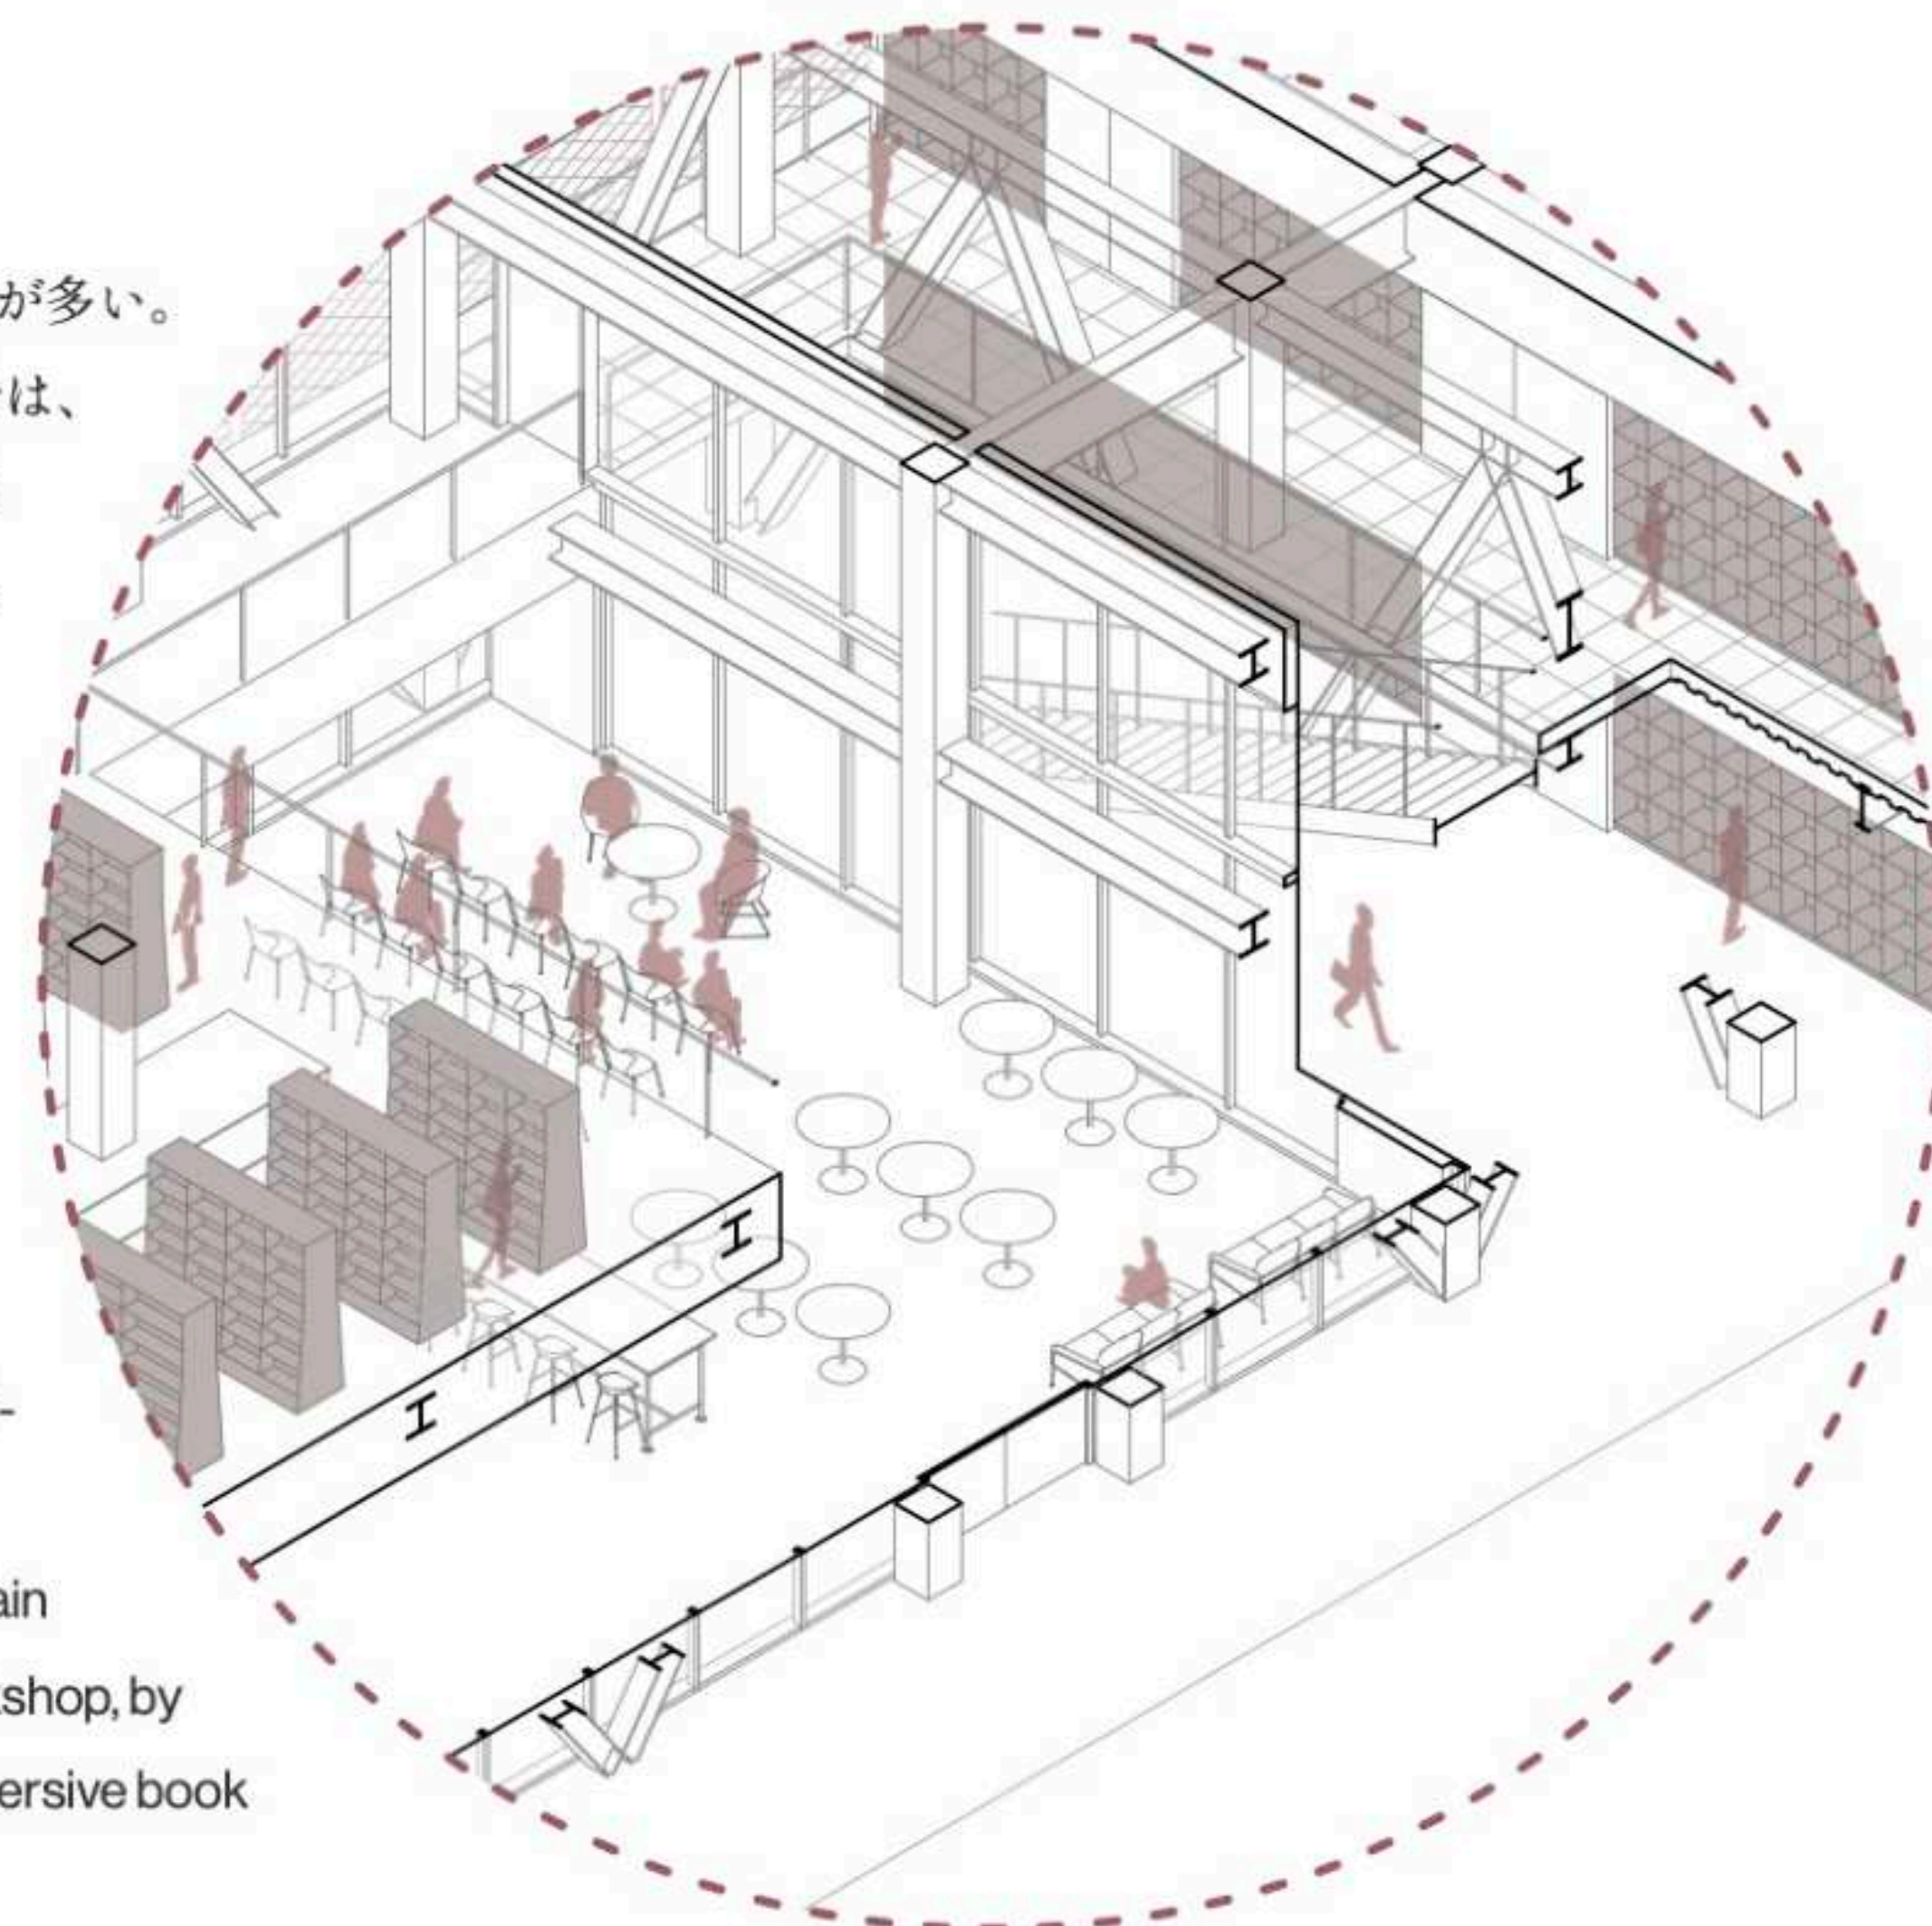

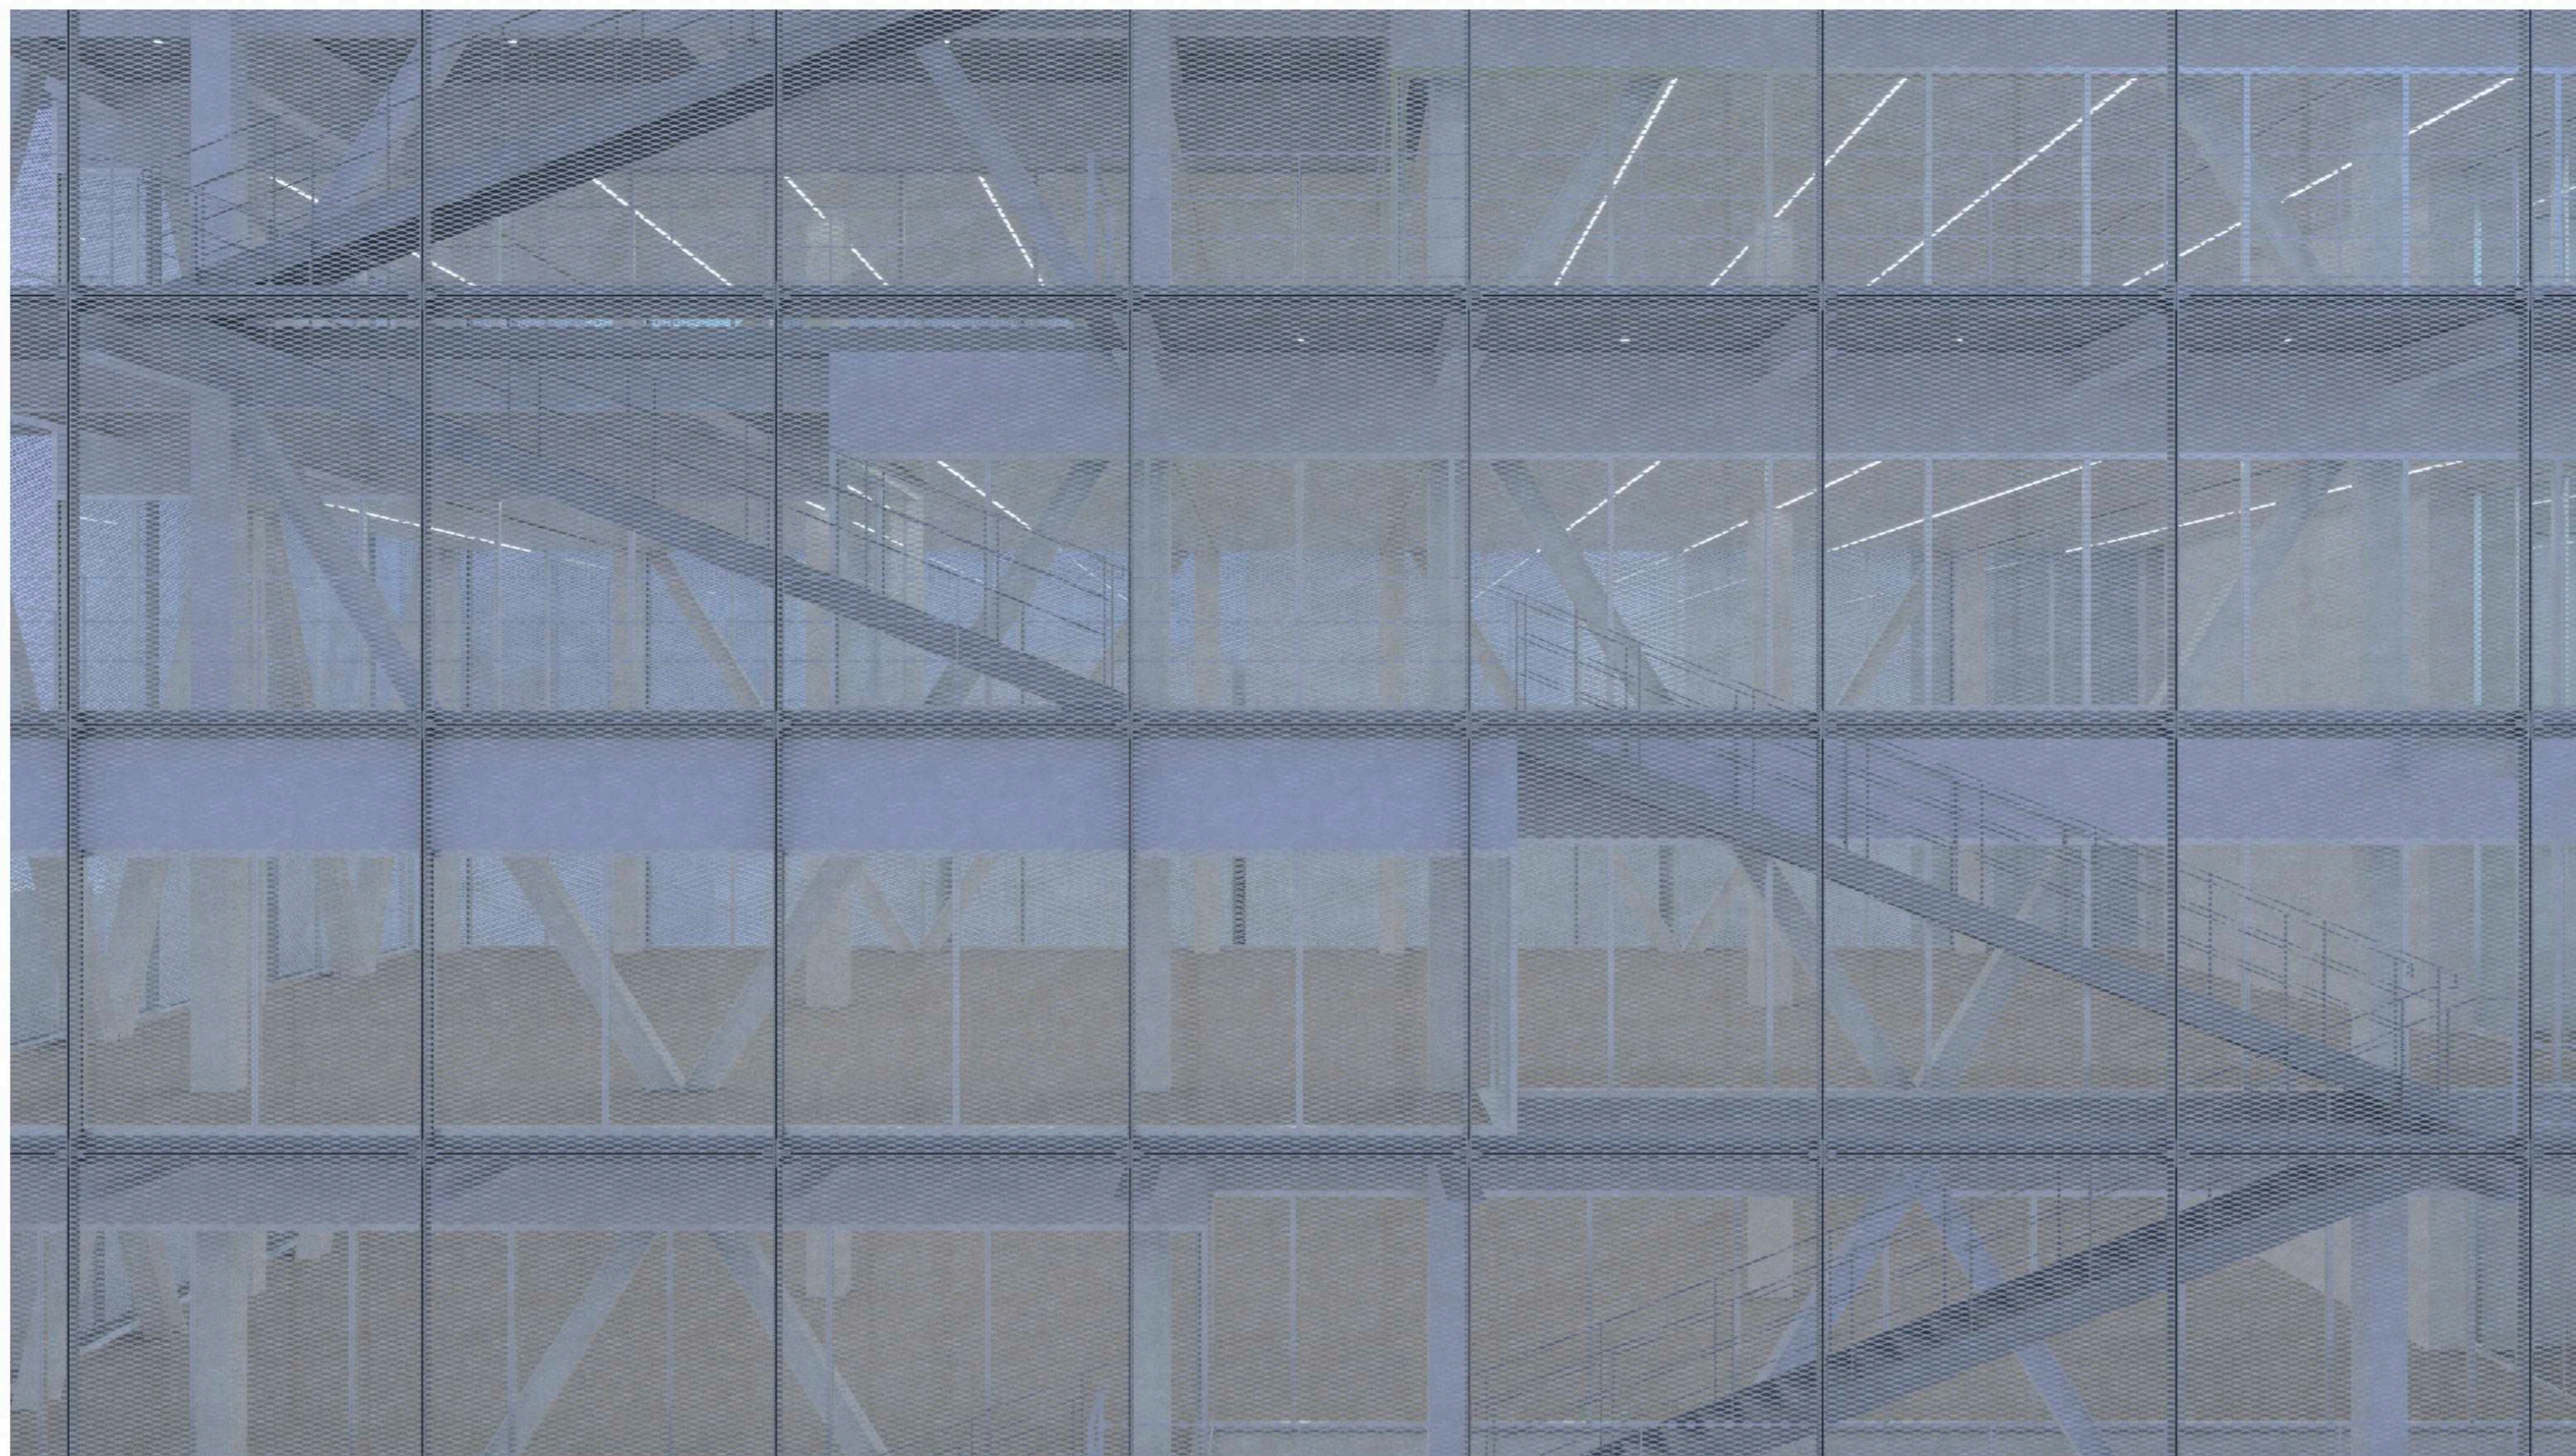

構造

自由で開放的な執務空間をつくるため、柱や梁を可能な限り落とさない合理的な構造計画を目指した。執務空間を取り囲む三方の周囲に H 鋼のブレースを用いて水平力を負担させ、大スパン部分の梁せいを 900mm にすることで、執務空間内に落とす柱を 2 本のみに留めた。

長手方向のスパンは屋外階段の寸法によって決められており、普段から使うゆったりとした寸法の直線階段と、鉄骨の構造が一体的になっている。最終的には、敷地を最大限に活用して 15 × 23m を基本とする巨大な執務空間を実現できた。


また、北側道路に面する立体広場は、通りと建築のやわらかい関係性を作るファサードになるように、柱を落とさず 2.5m の片持ち梁で支えられた空間になっている。




Structure


In pursuit of a free and open working environment, the structural scheme was developed with the aim of eliminating columns and beams as far as possible. Horizontal forces are resisted by H-section steel braces placed along three sides enclosing the office space, and by specifying a beam depth of 900 mm for the long-span sections, the number of columns introduced into the working area was reduced to just two.

The span in the longitudinal direction is determined by the dimensions of the external staircase, with the generously proportioned straight-run stair — designed for everyday use — integrated structurally with the steel frame as a unified assembly. The result is a vast, column-free working space of 15 × 23 m that makes full use of the site.


Furthermore, the vertical plaza facing the northern road is suspended on 2.5 m cantilever beams with no columns dropped to the ground below, forming a facade that establishes a gentle and permeable relationship between the street and the building.

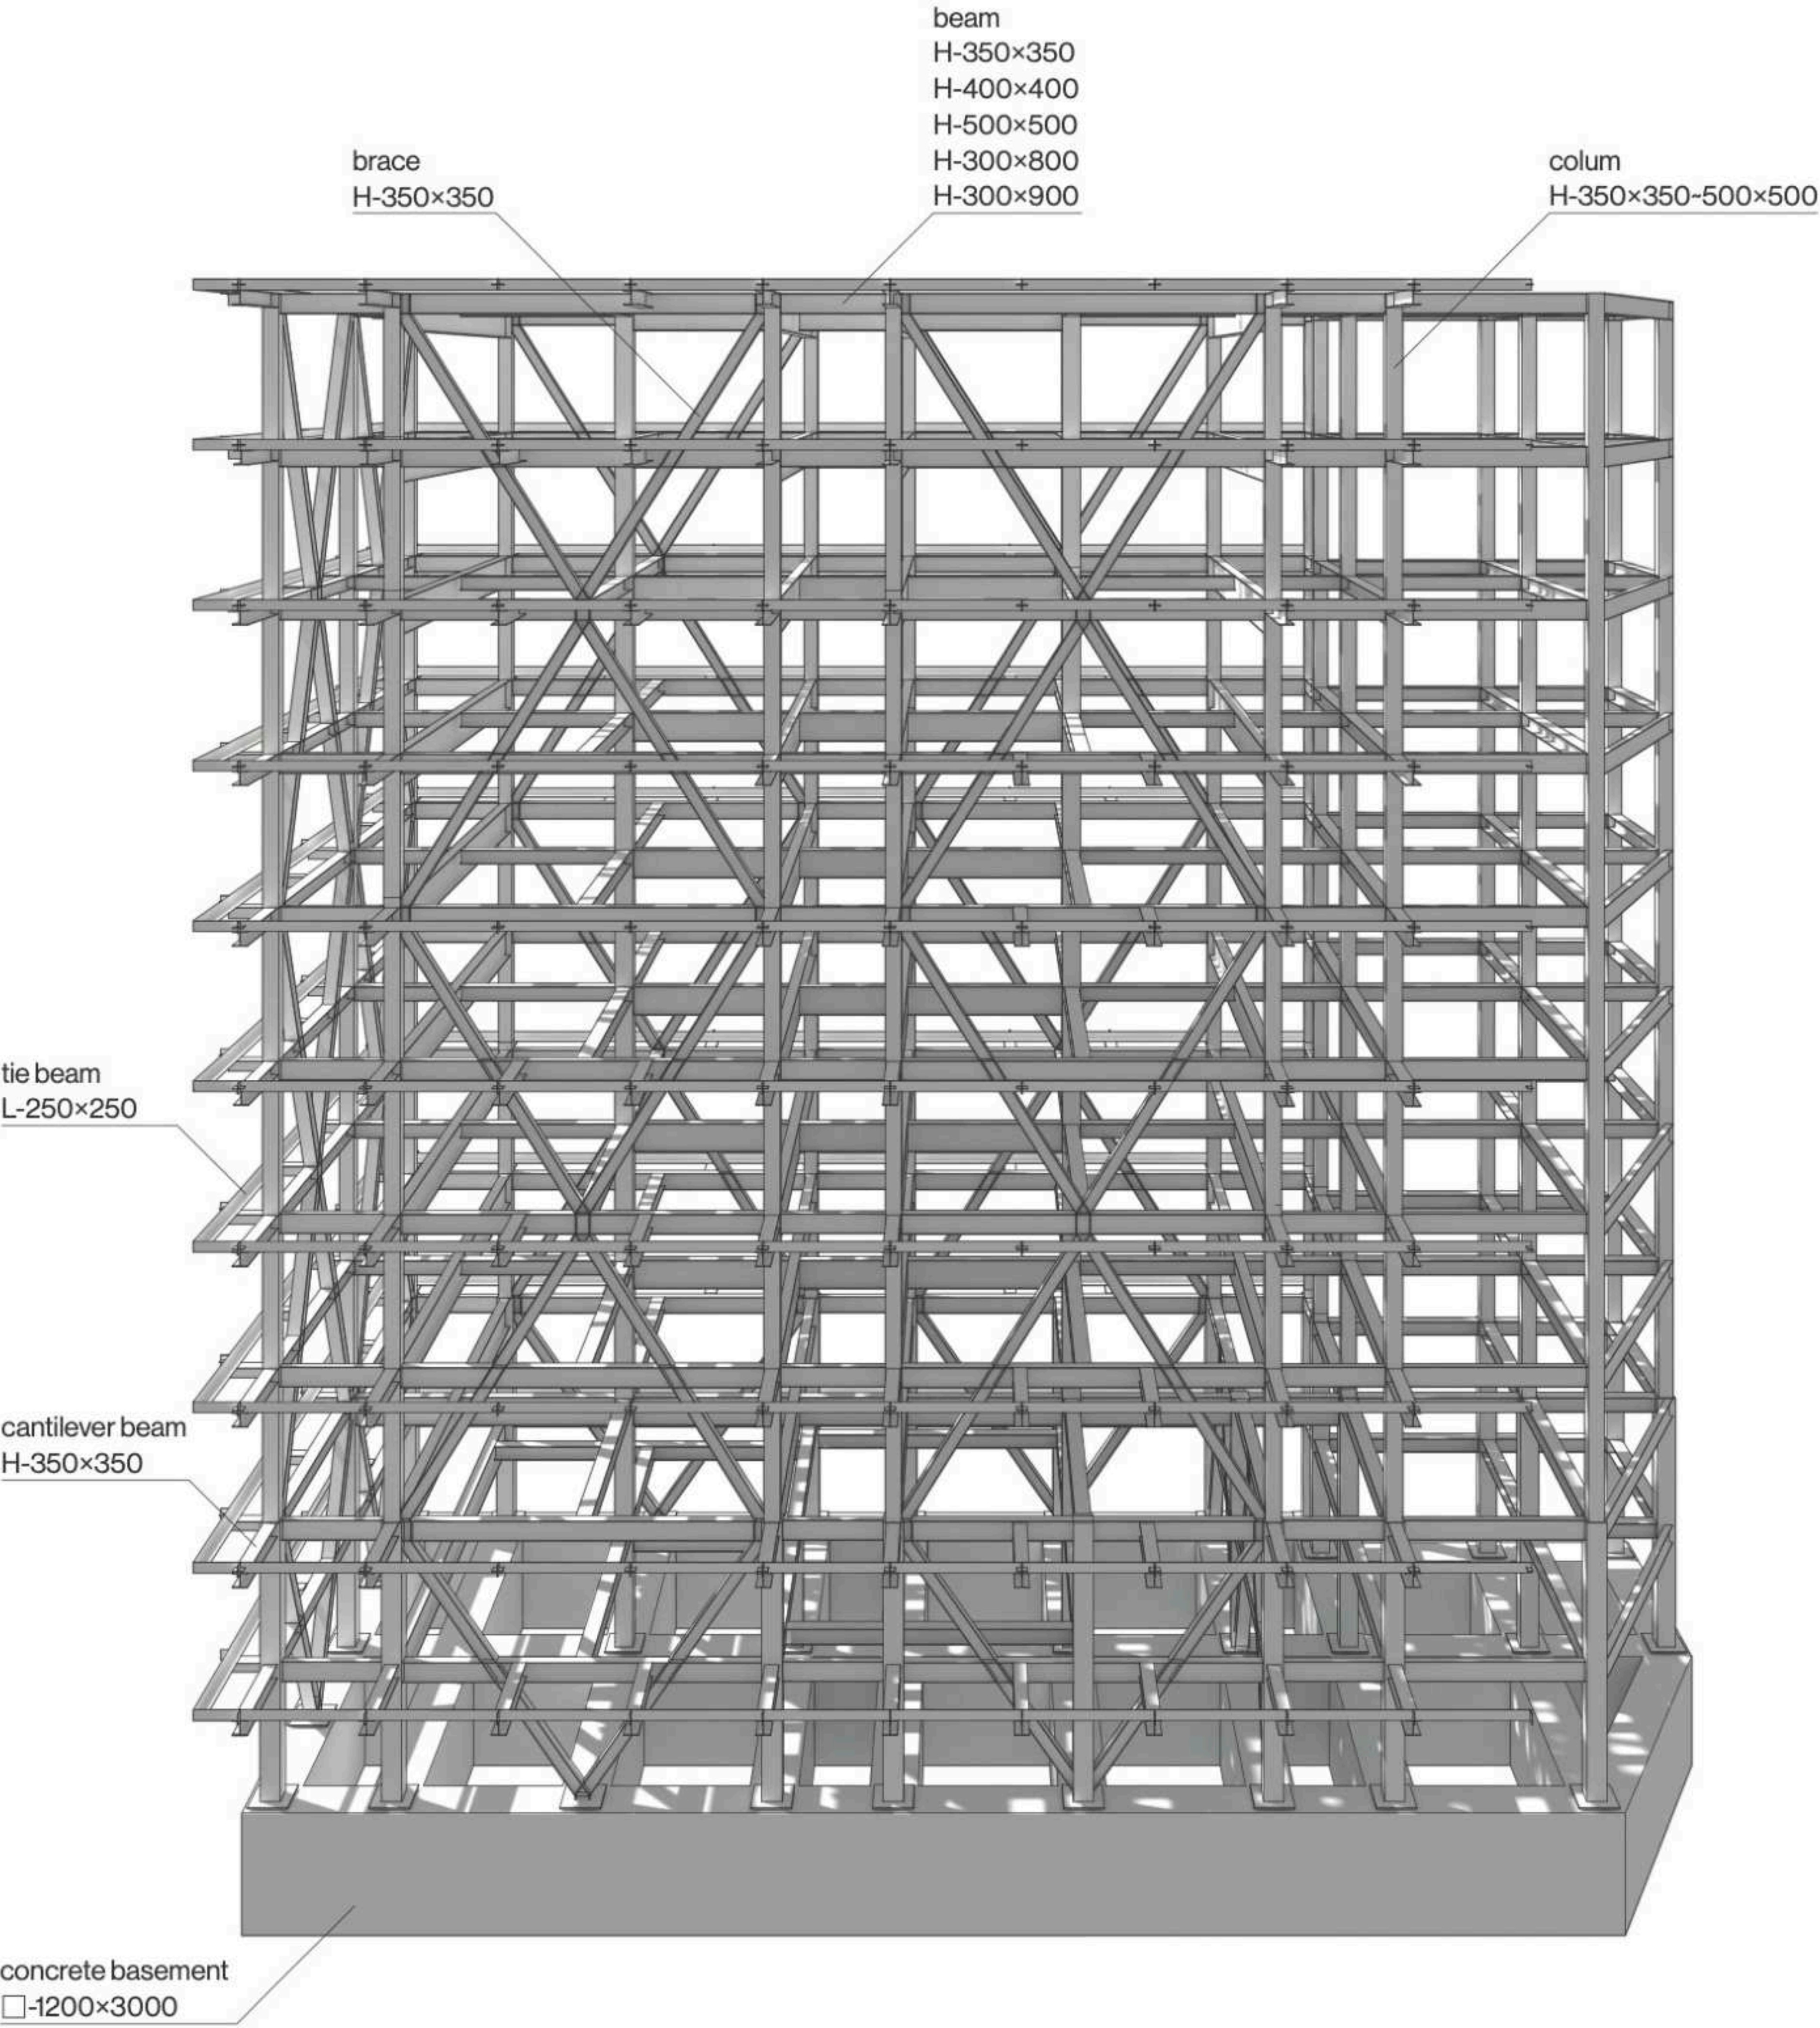

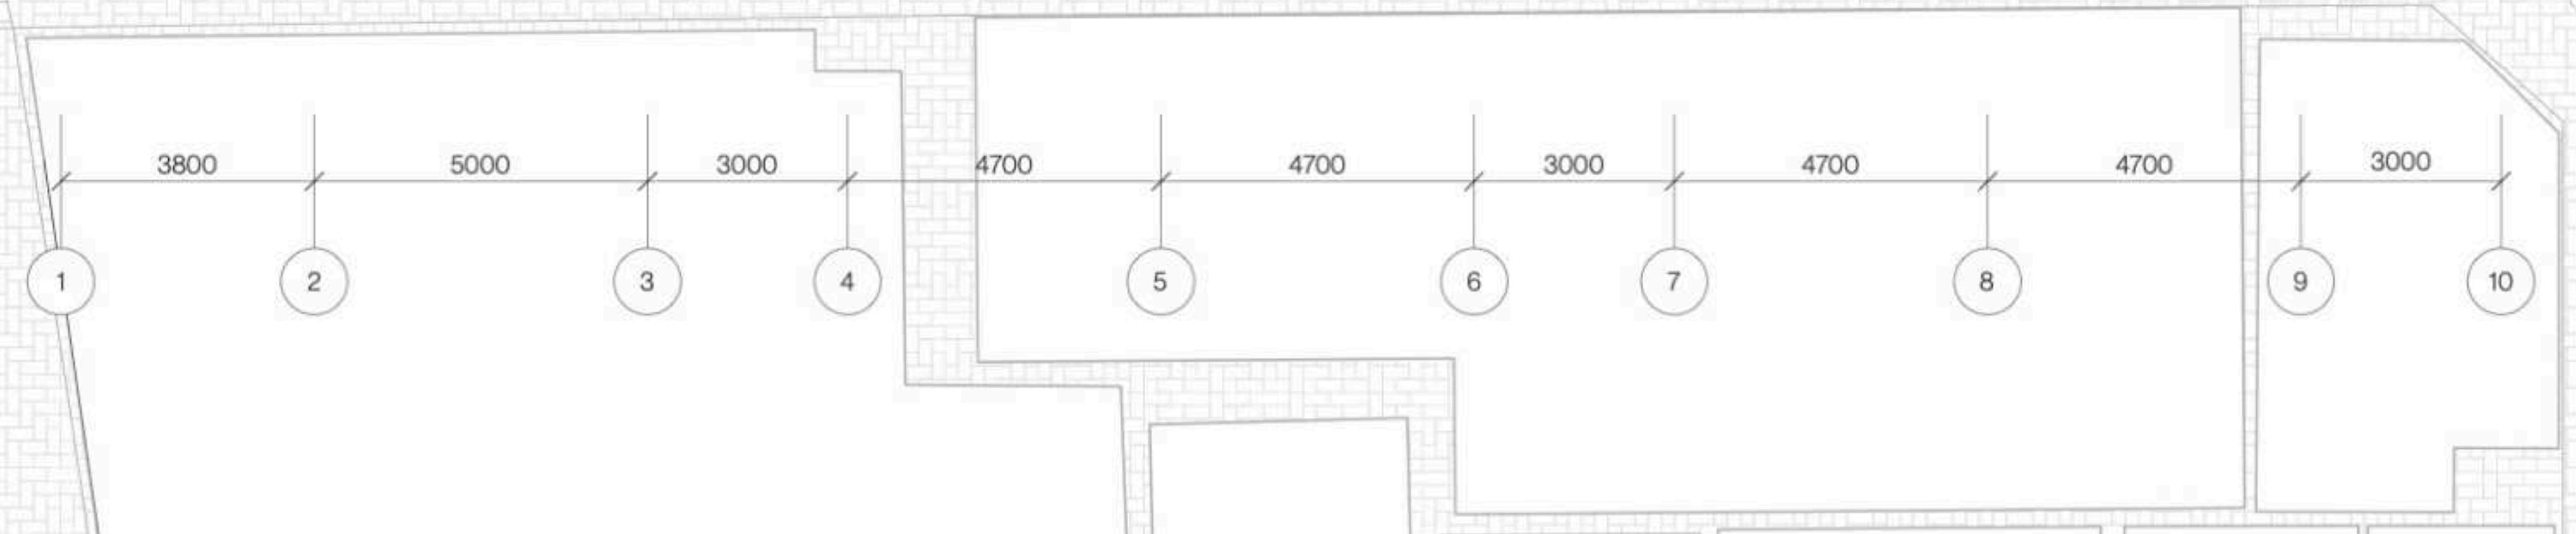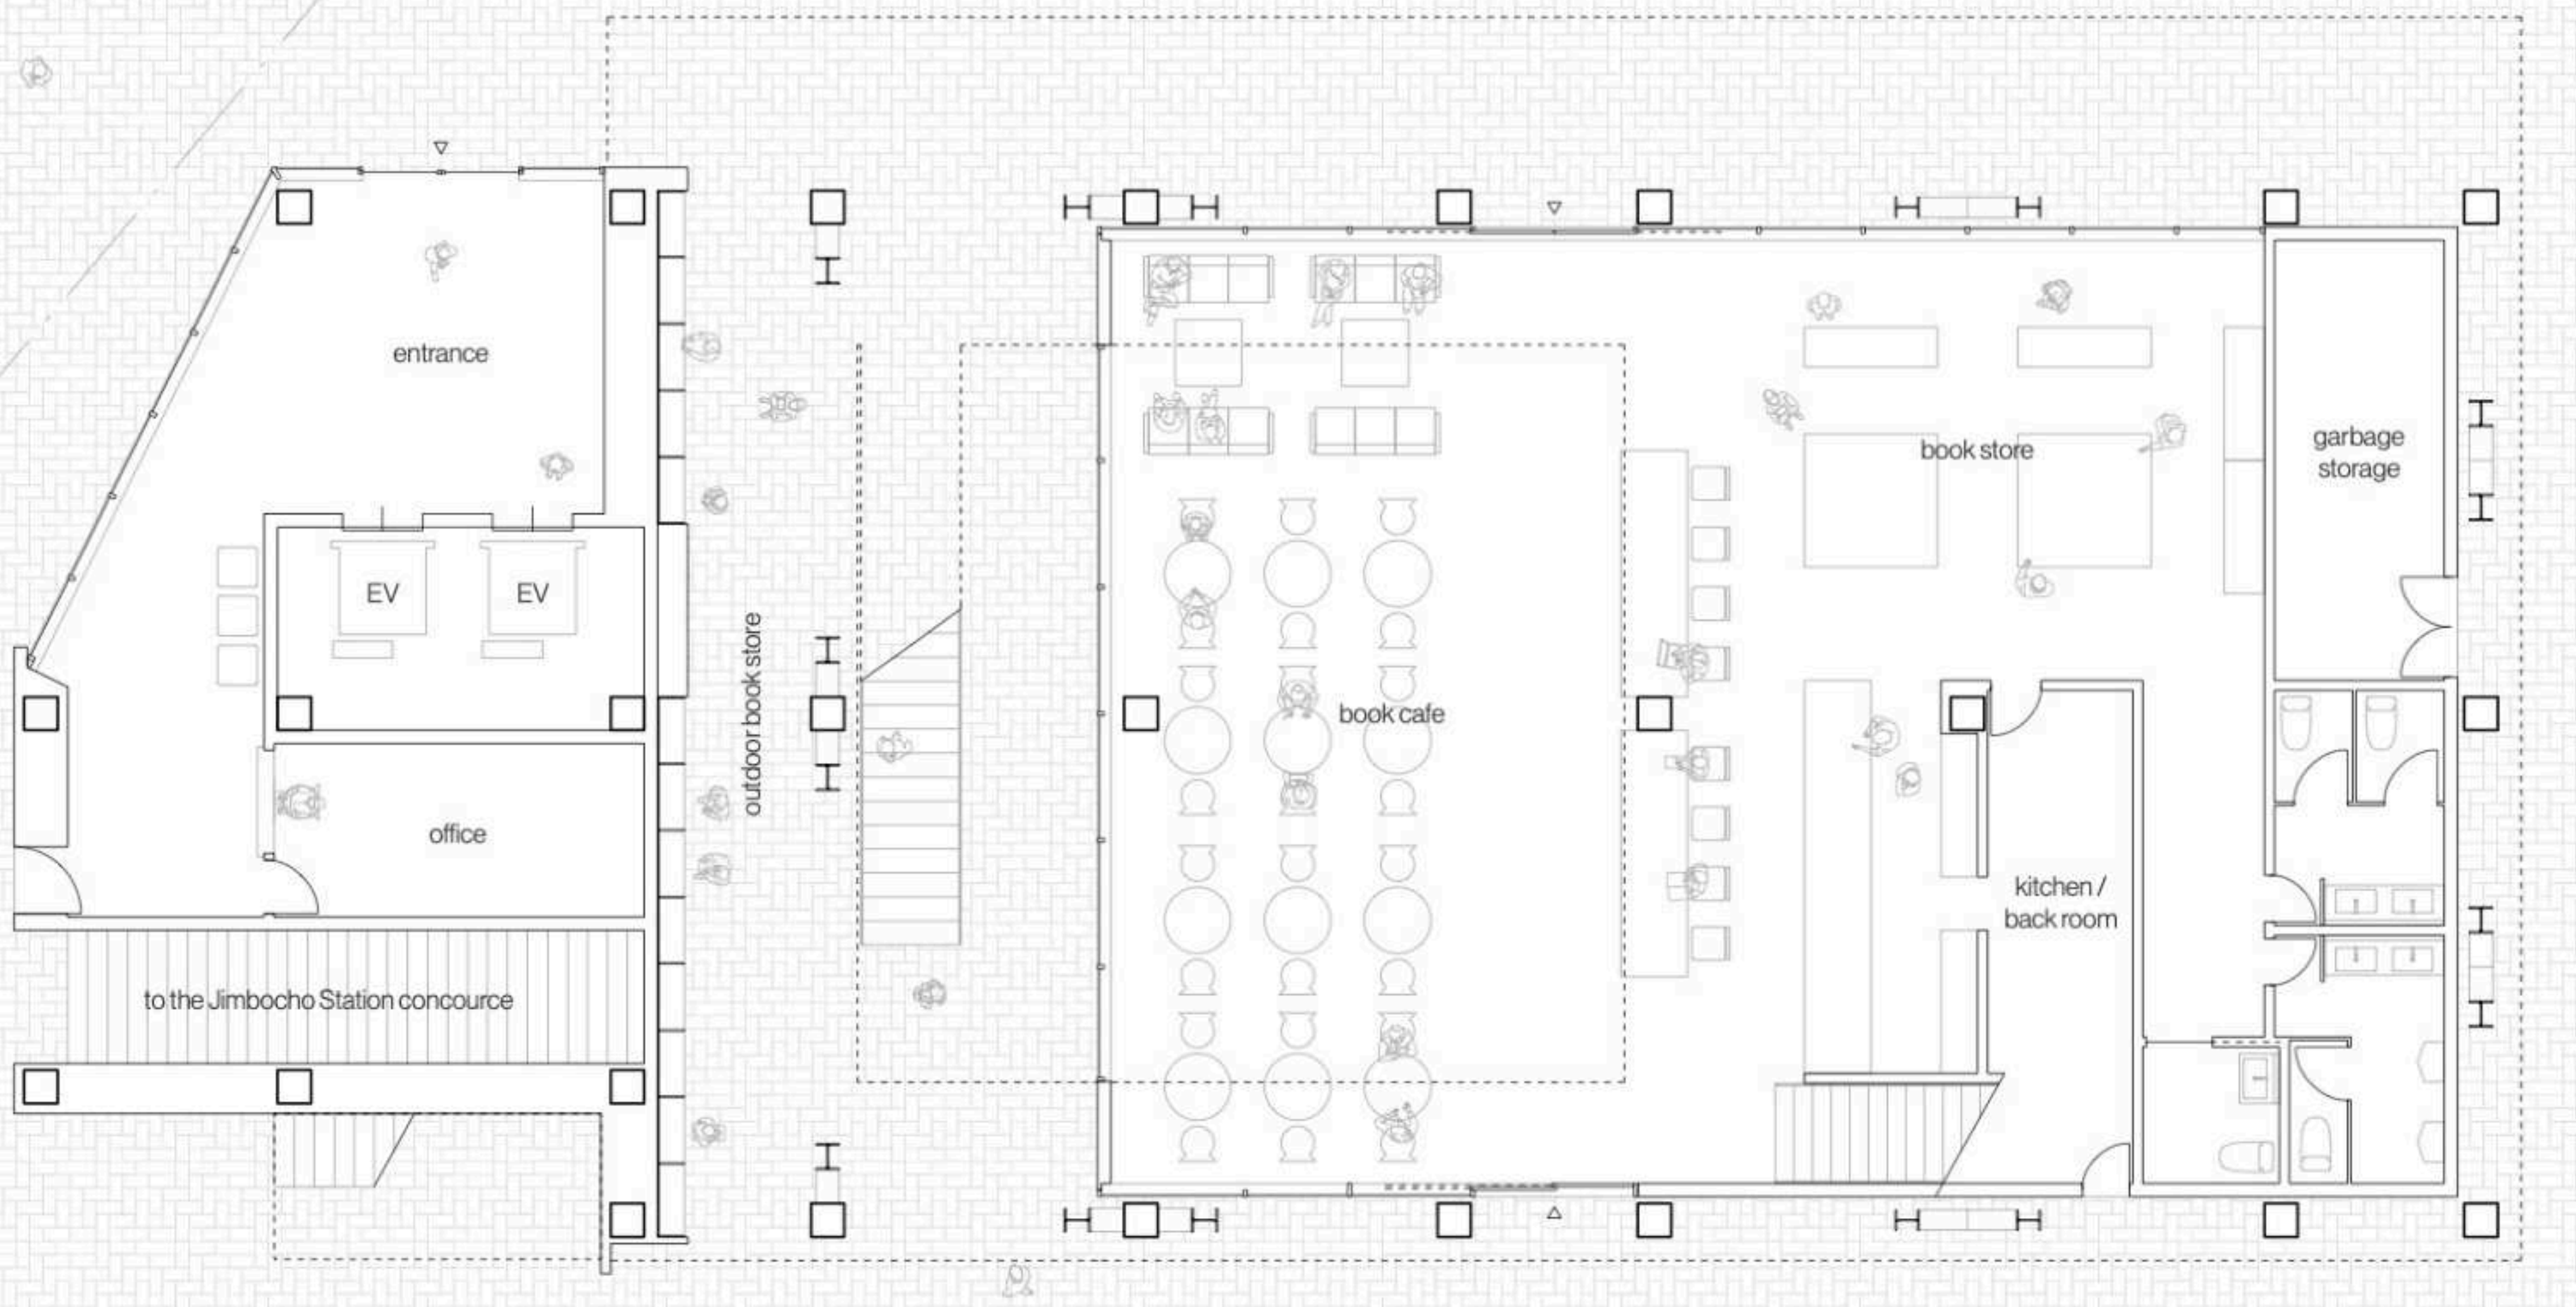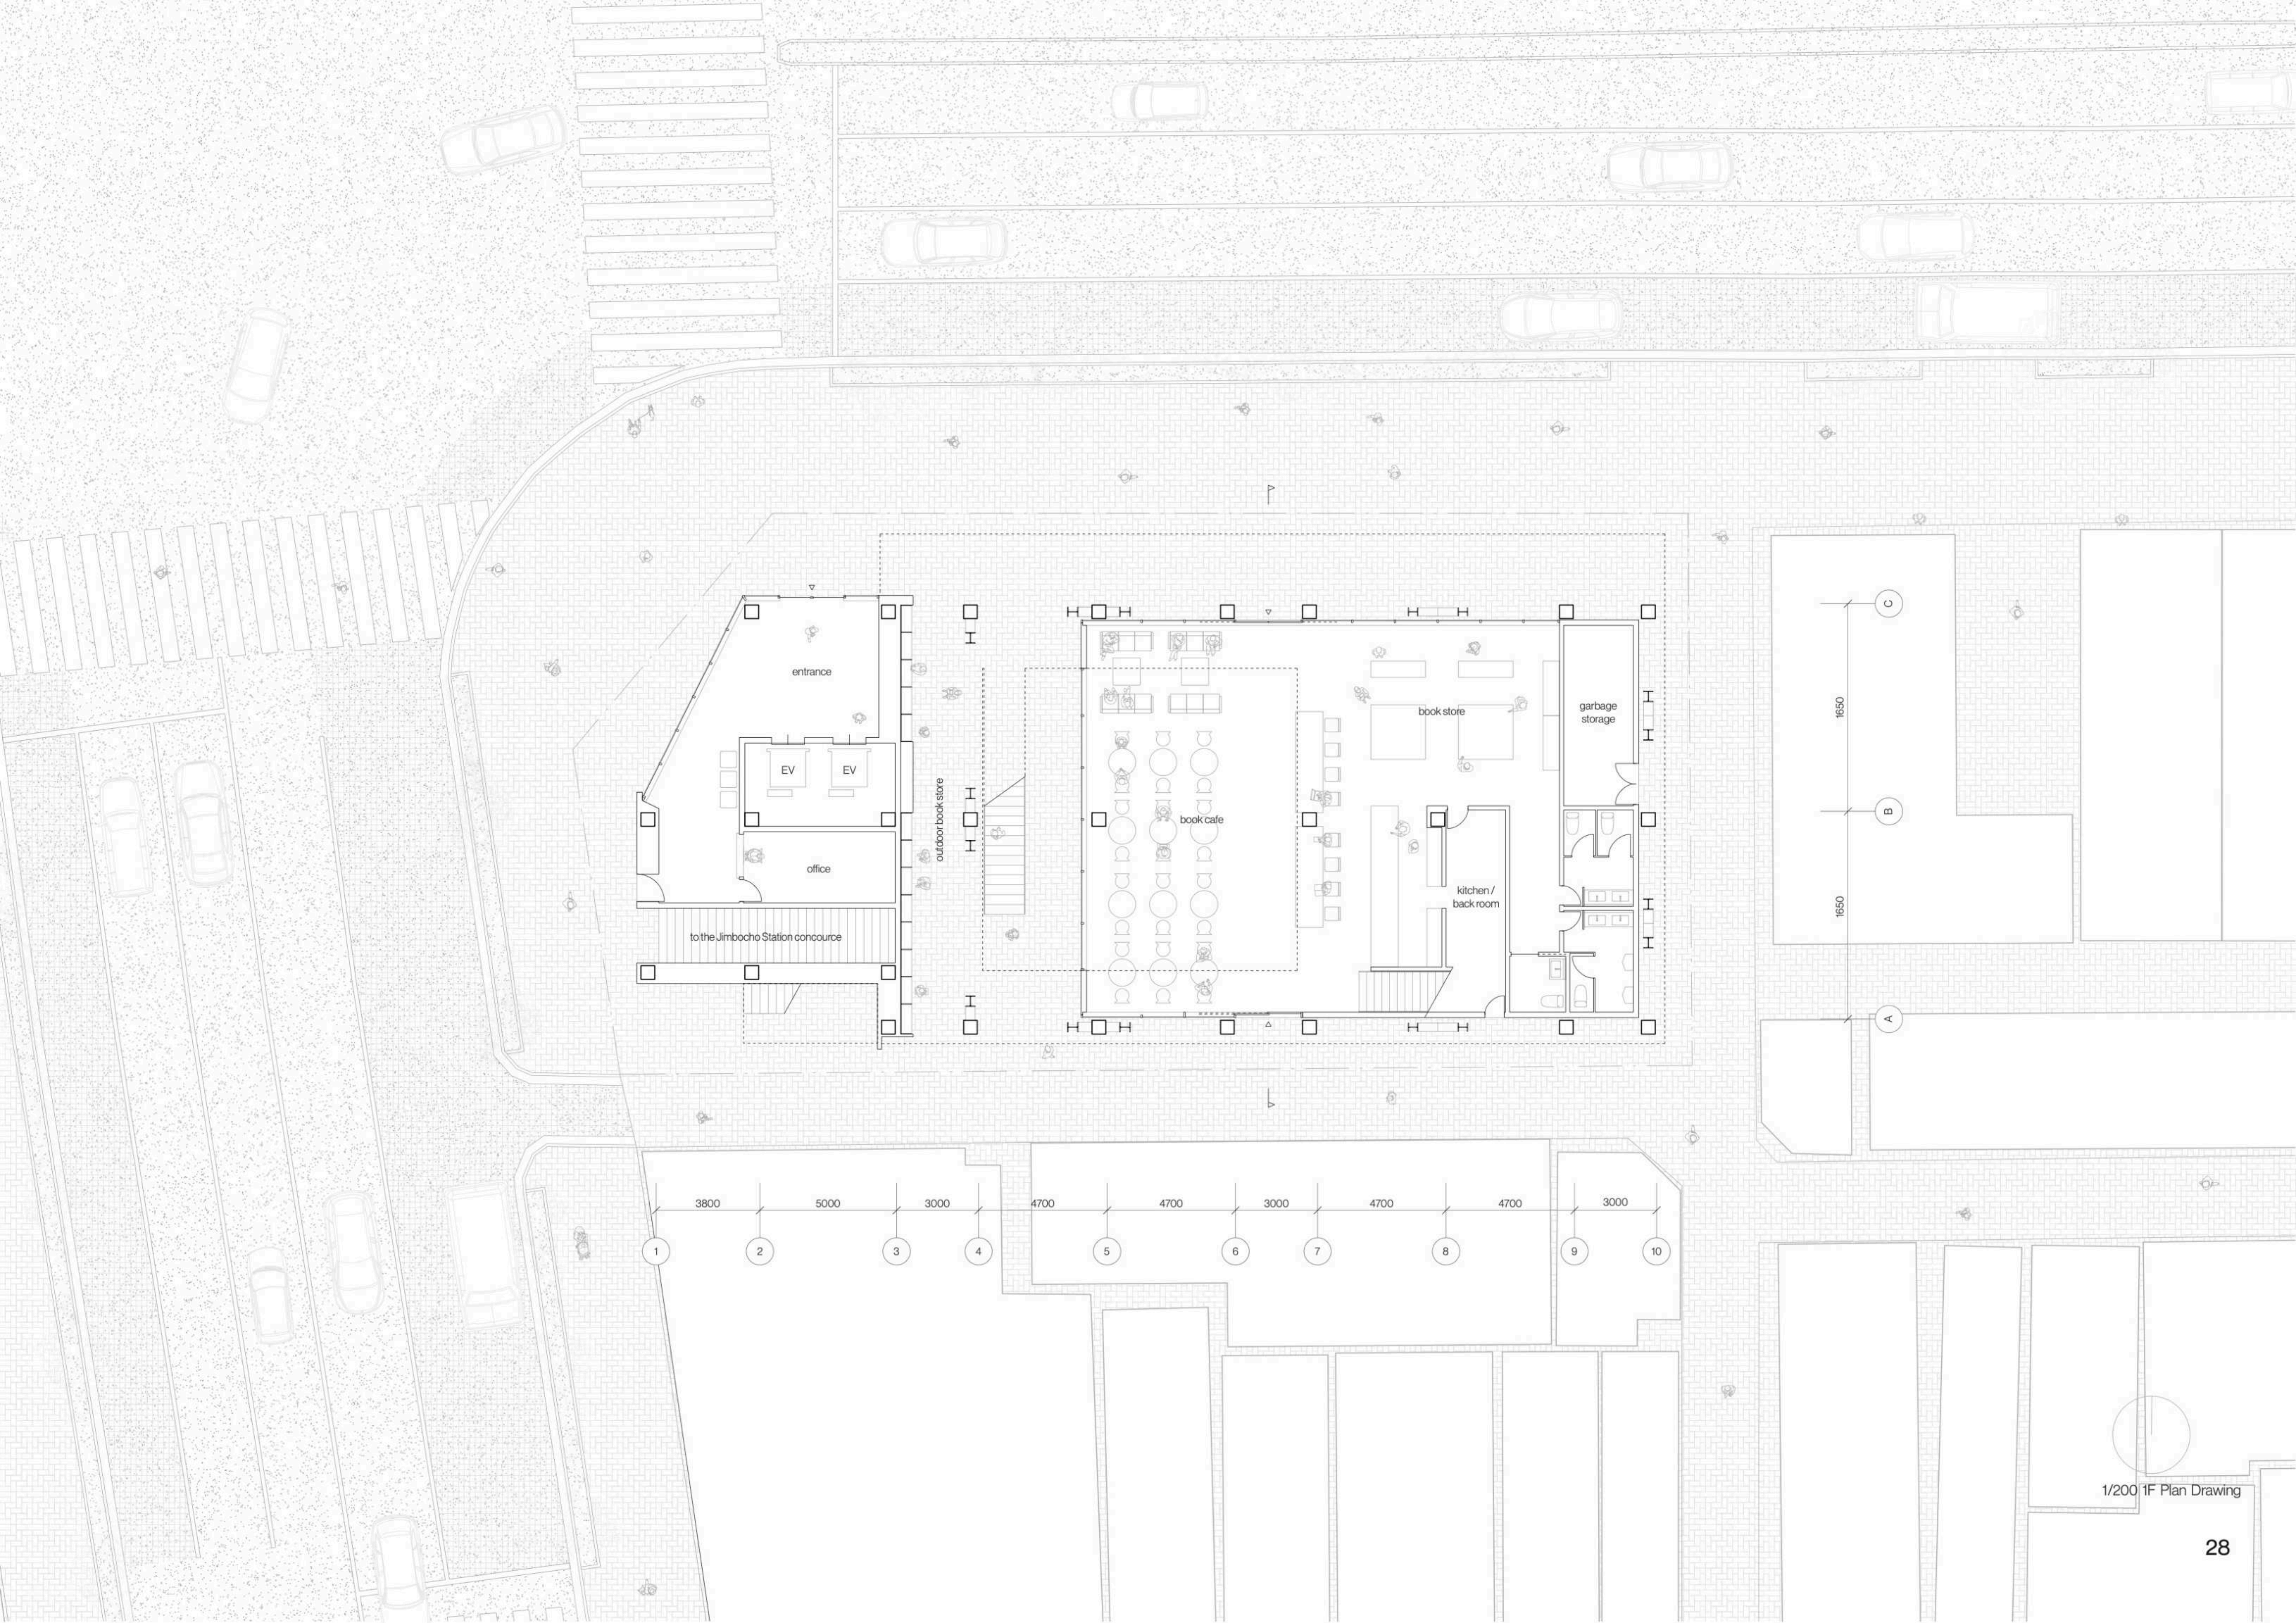


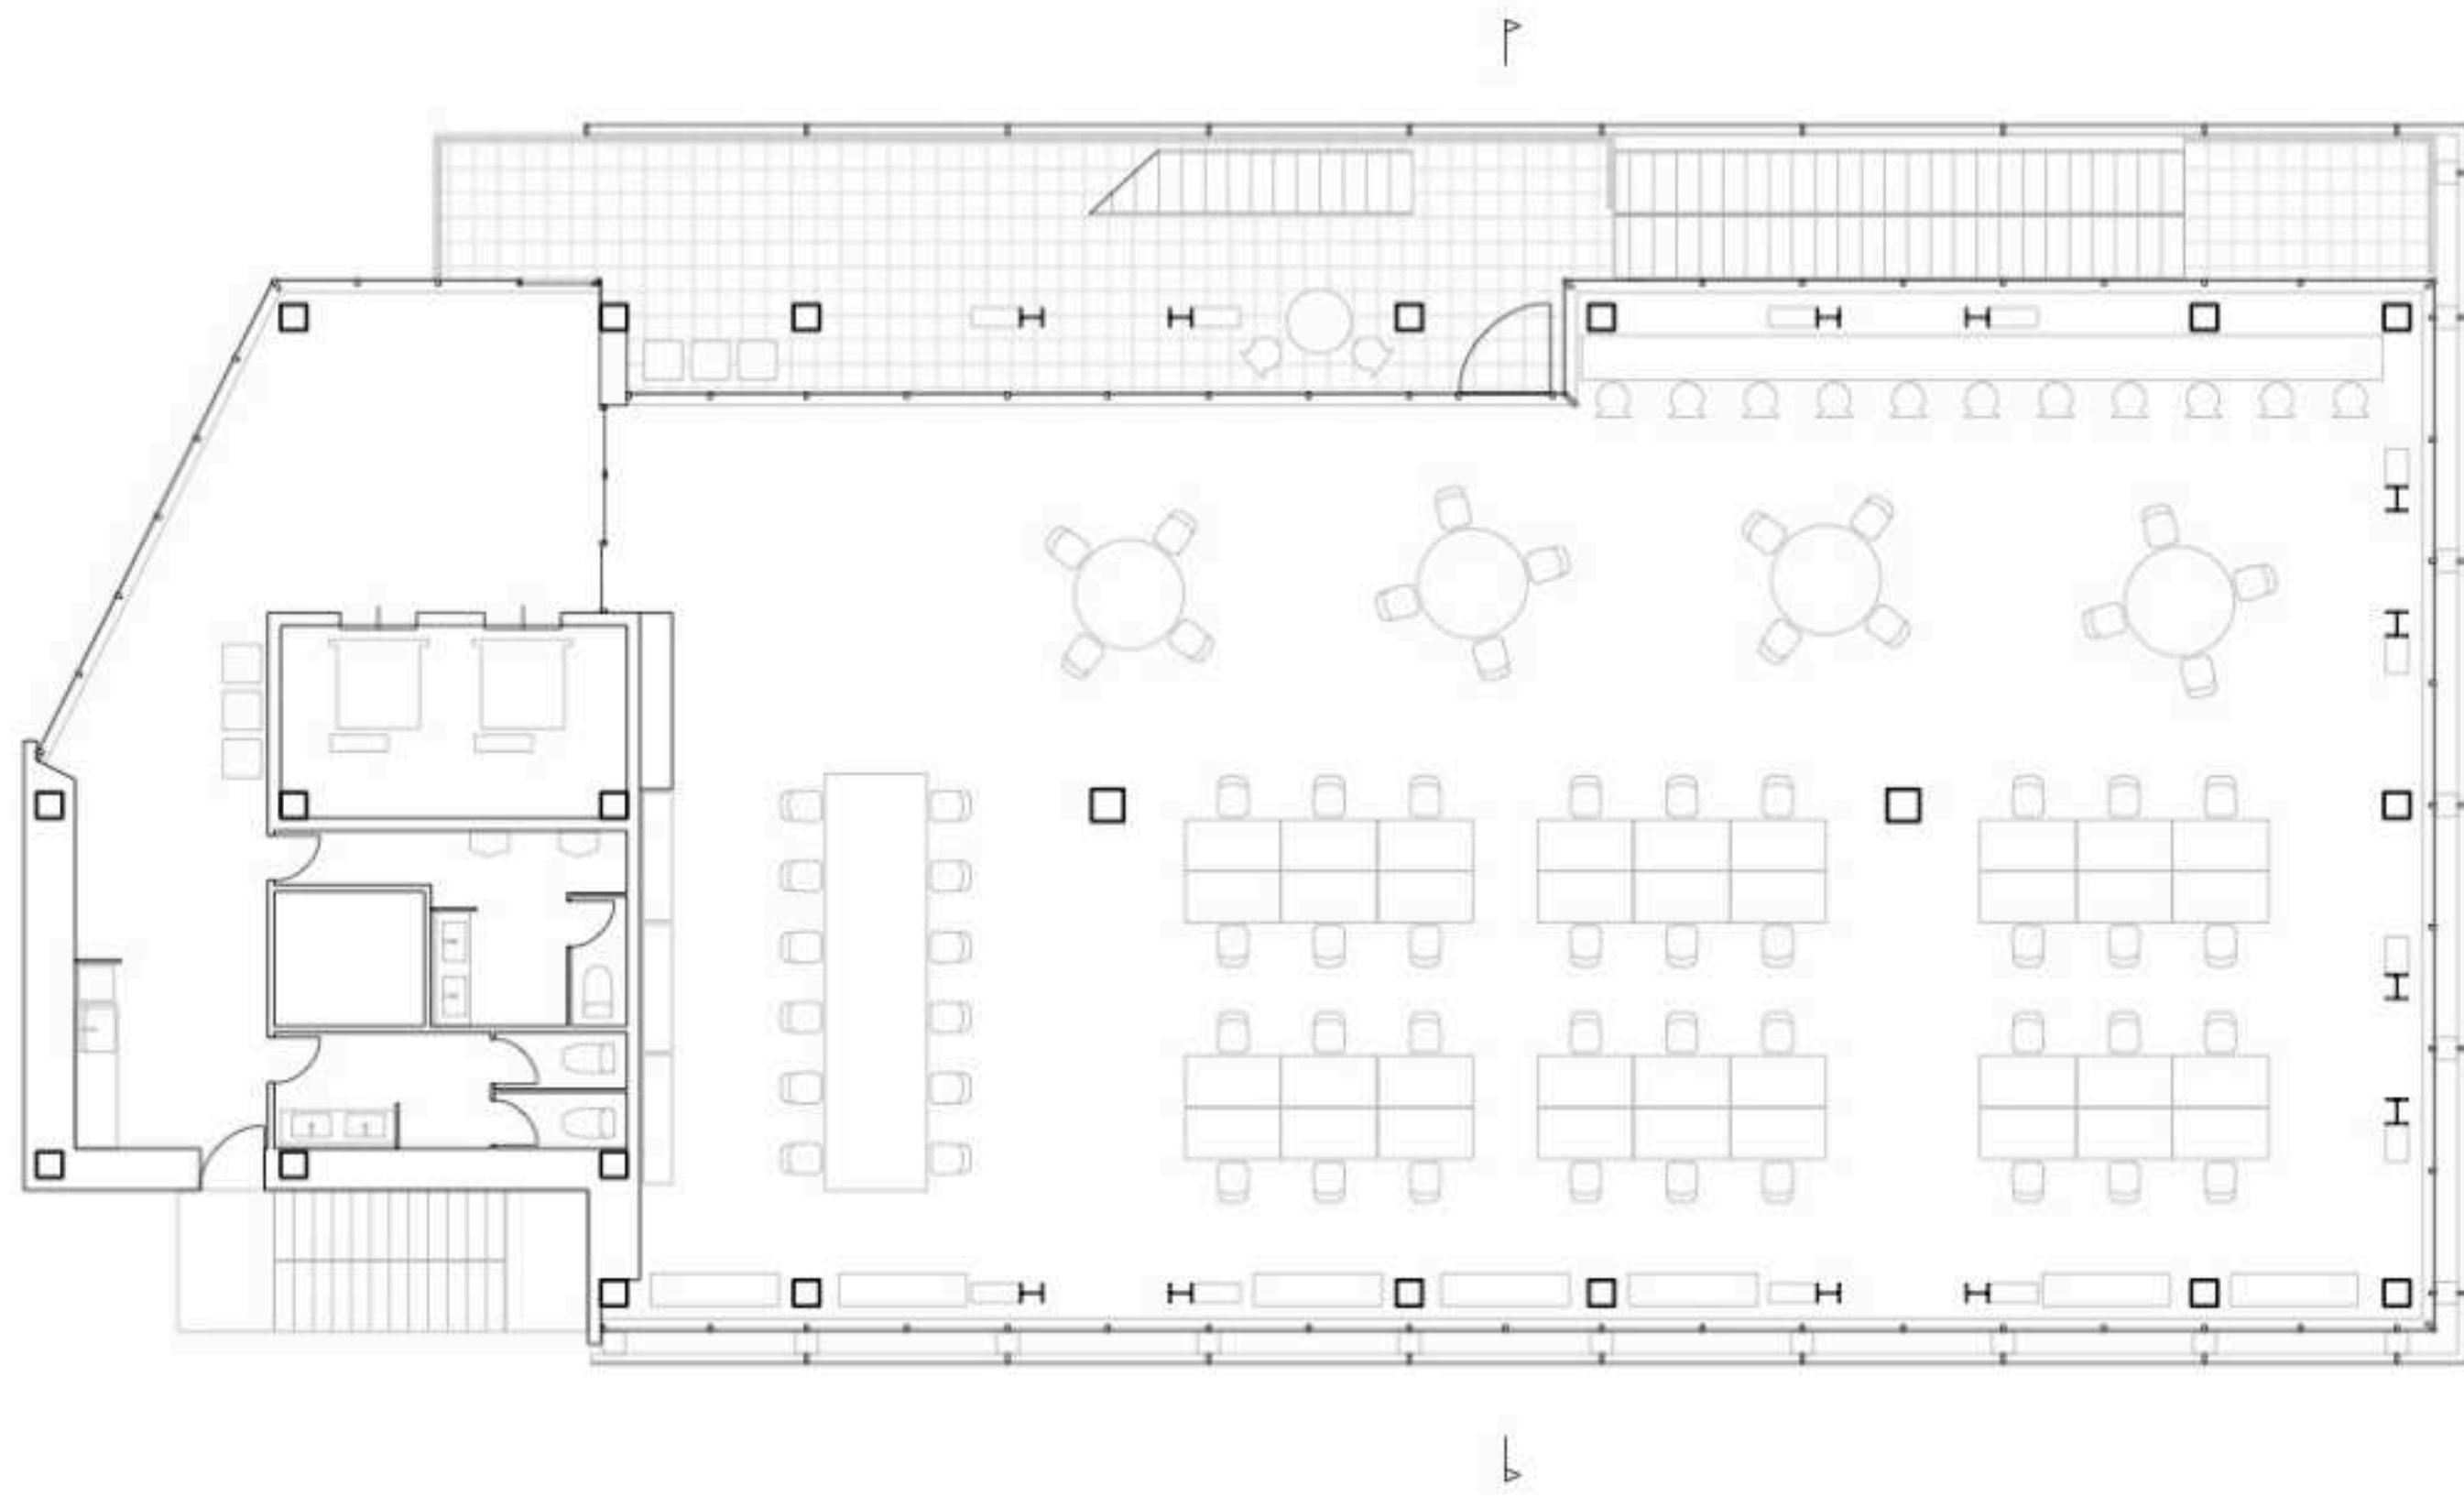


1/300 4F Plan Drawing

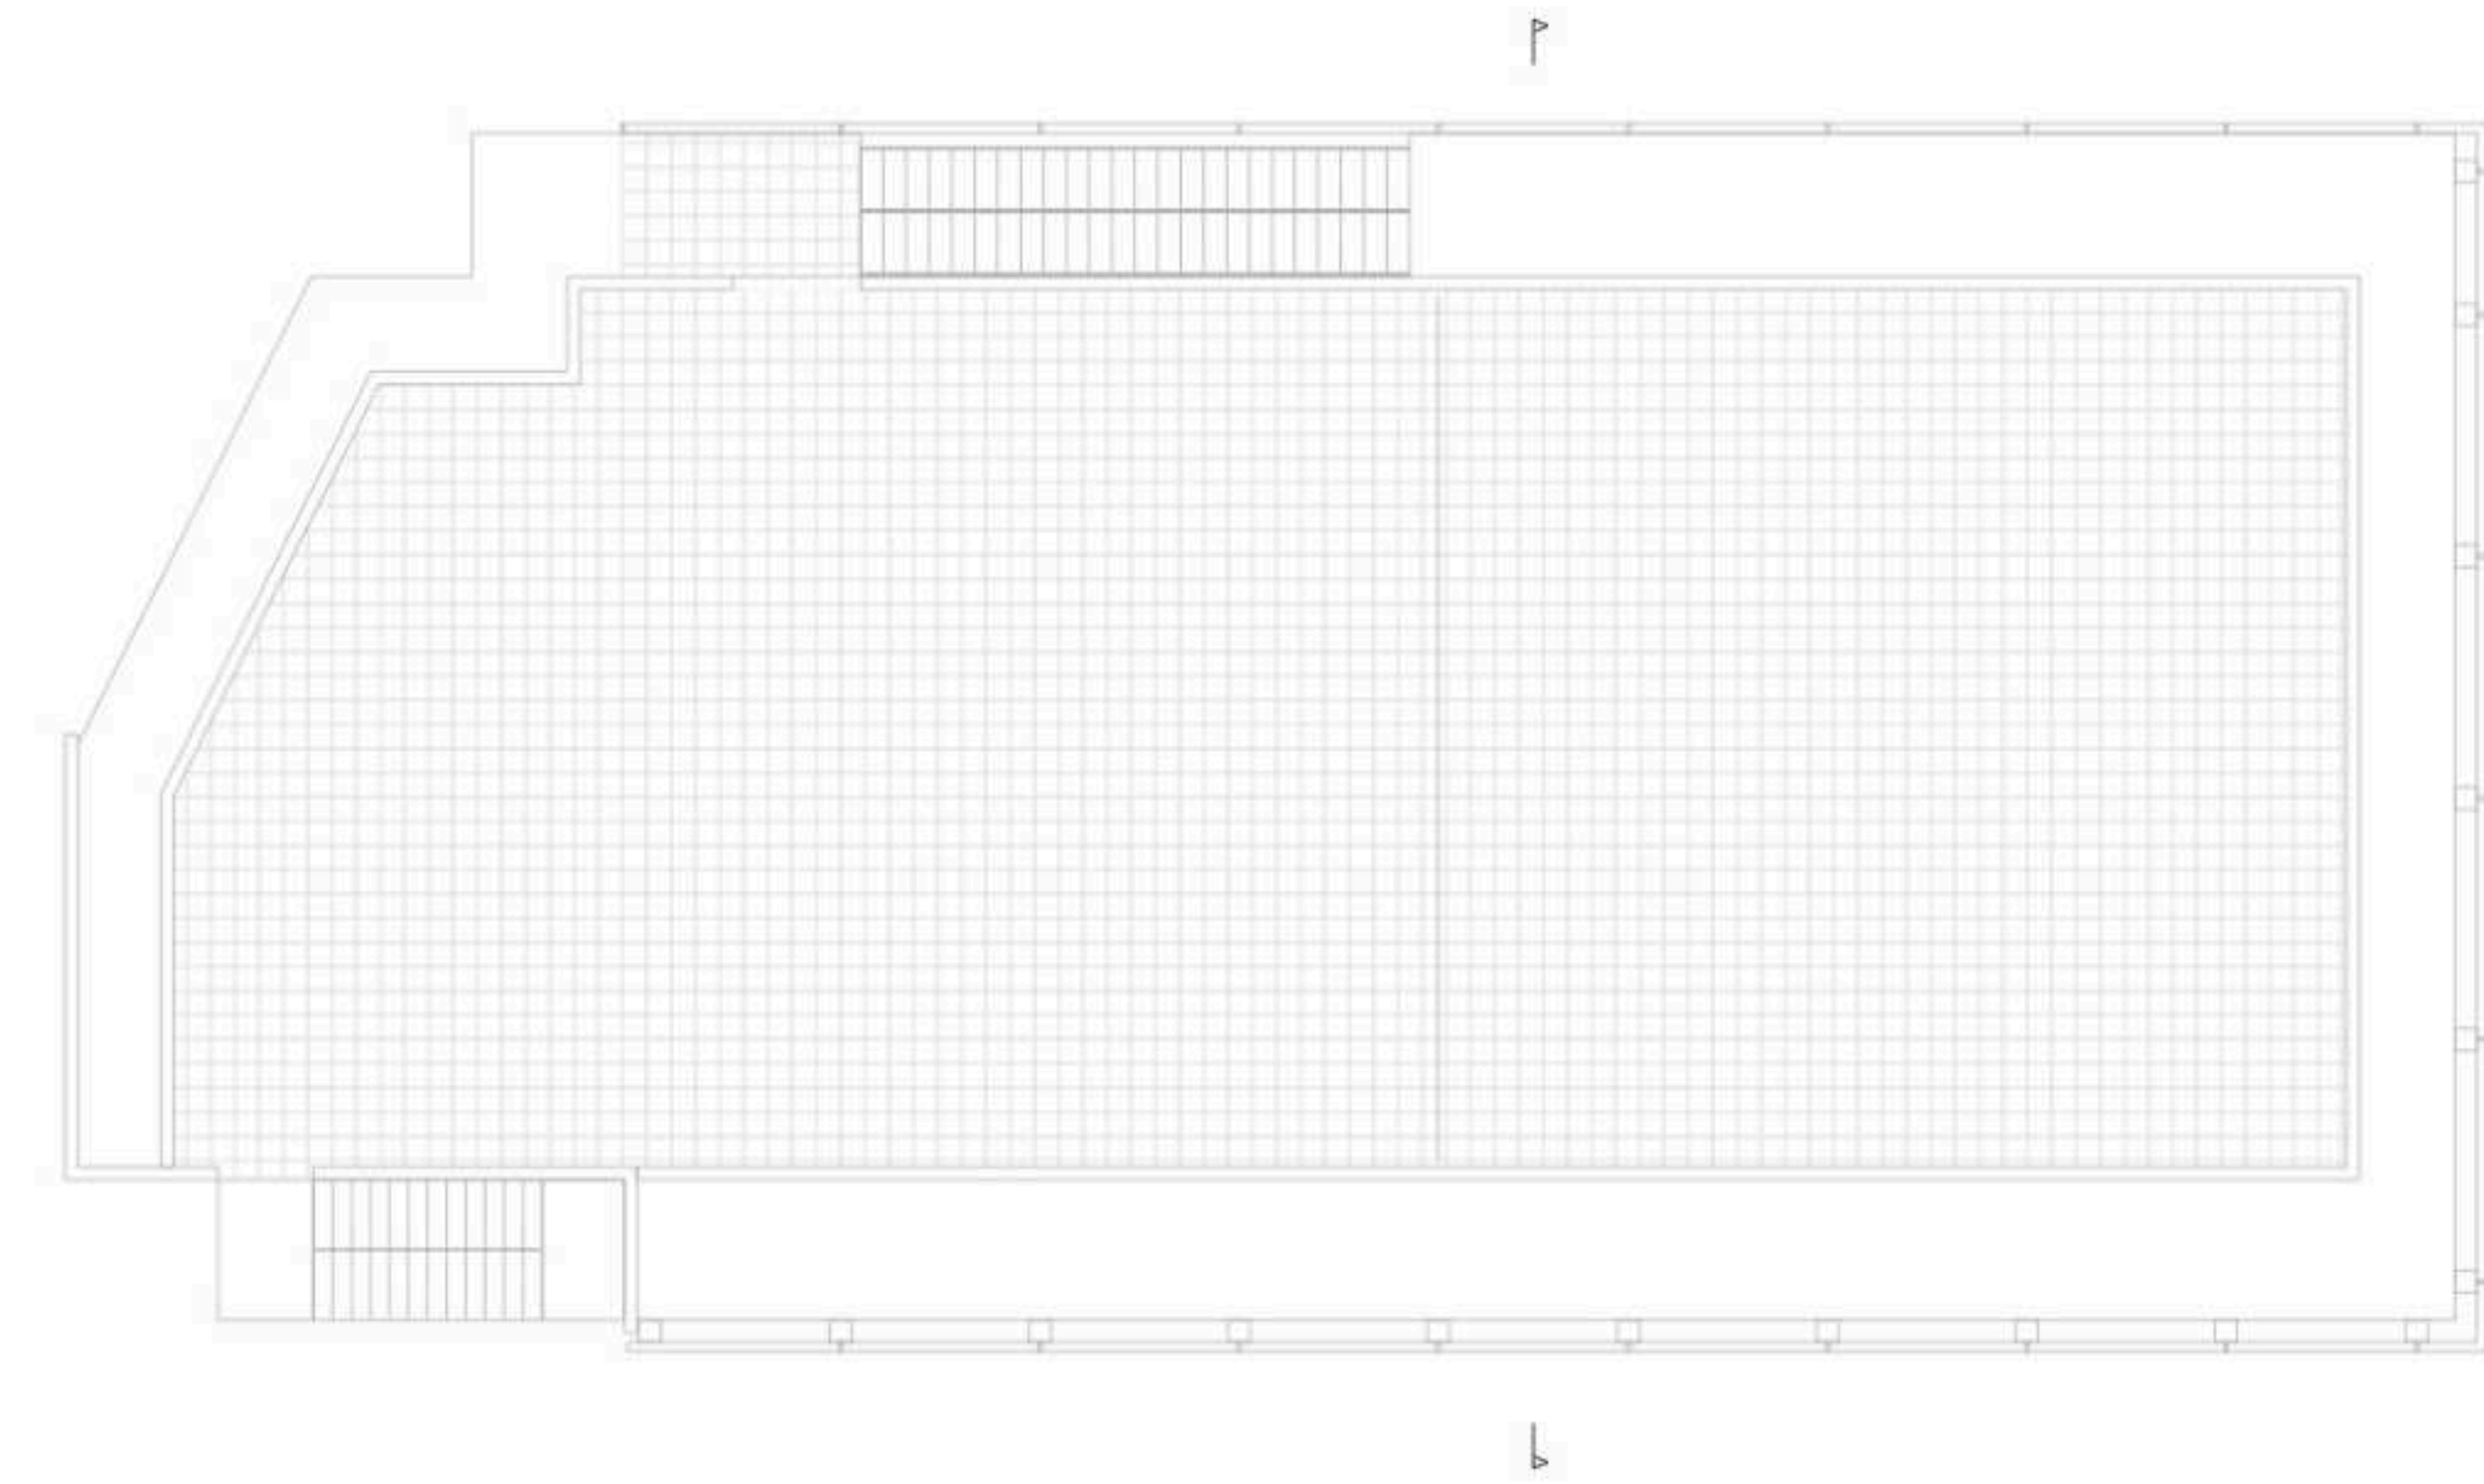


1/300 RF Plan Drawing

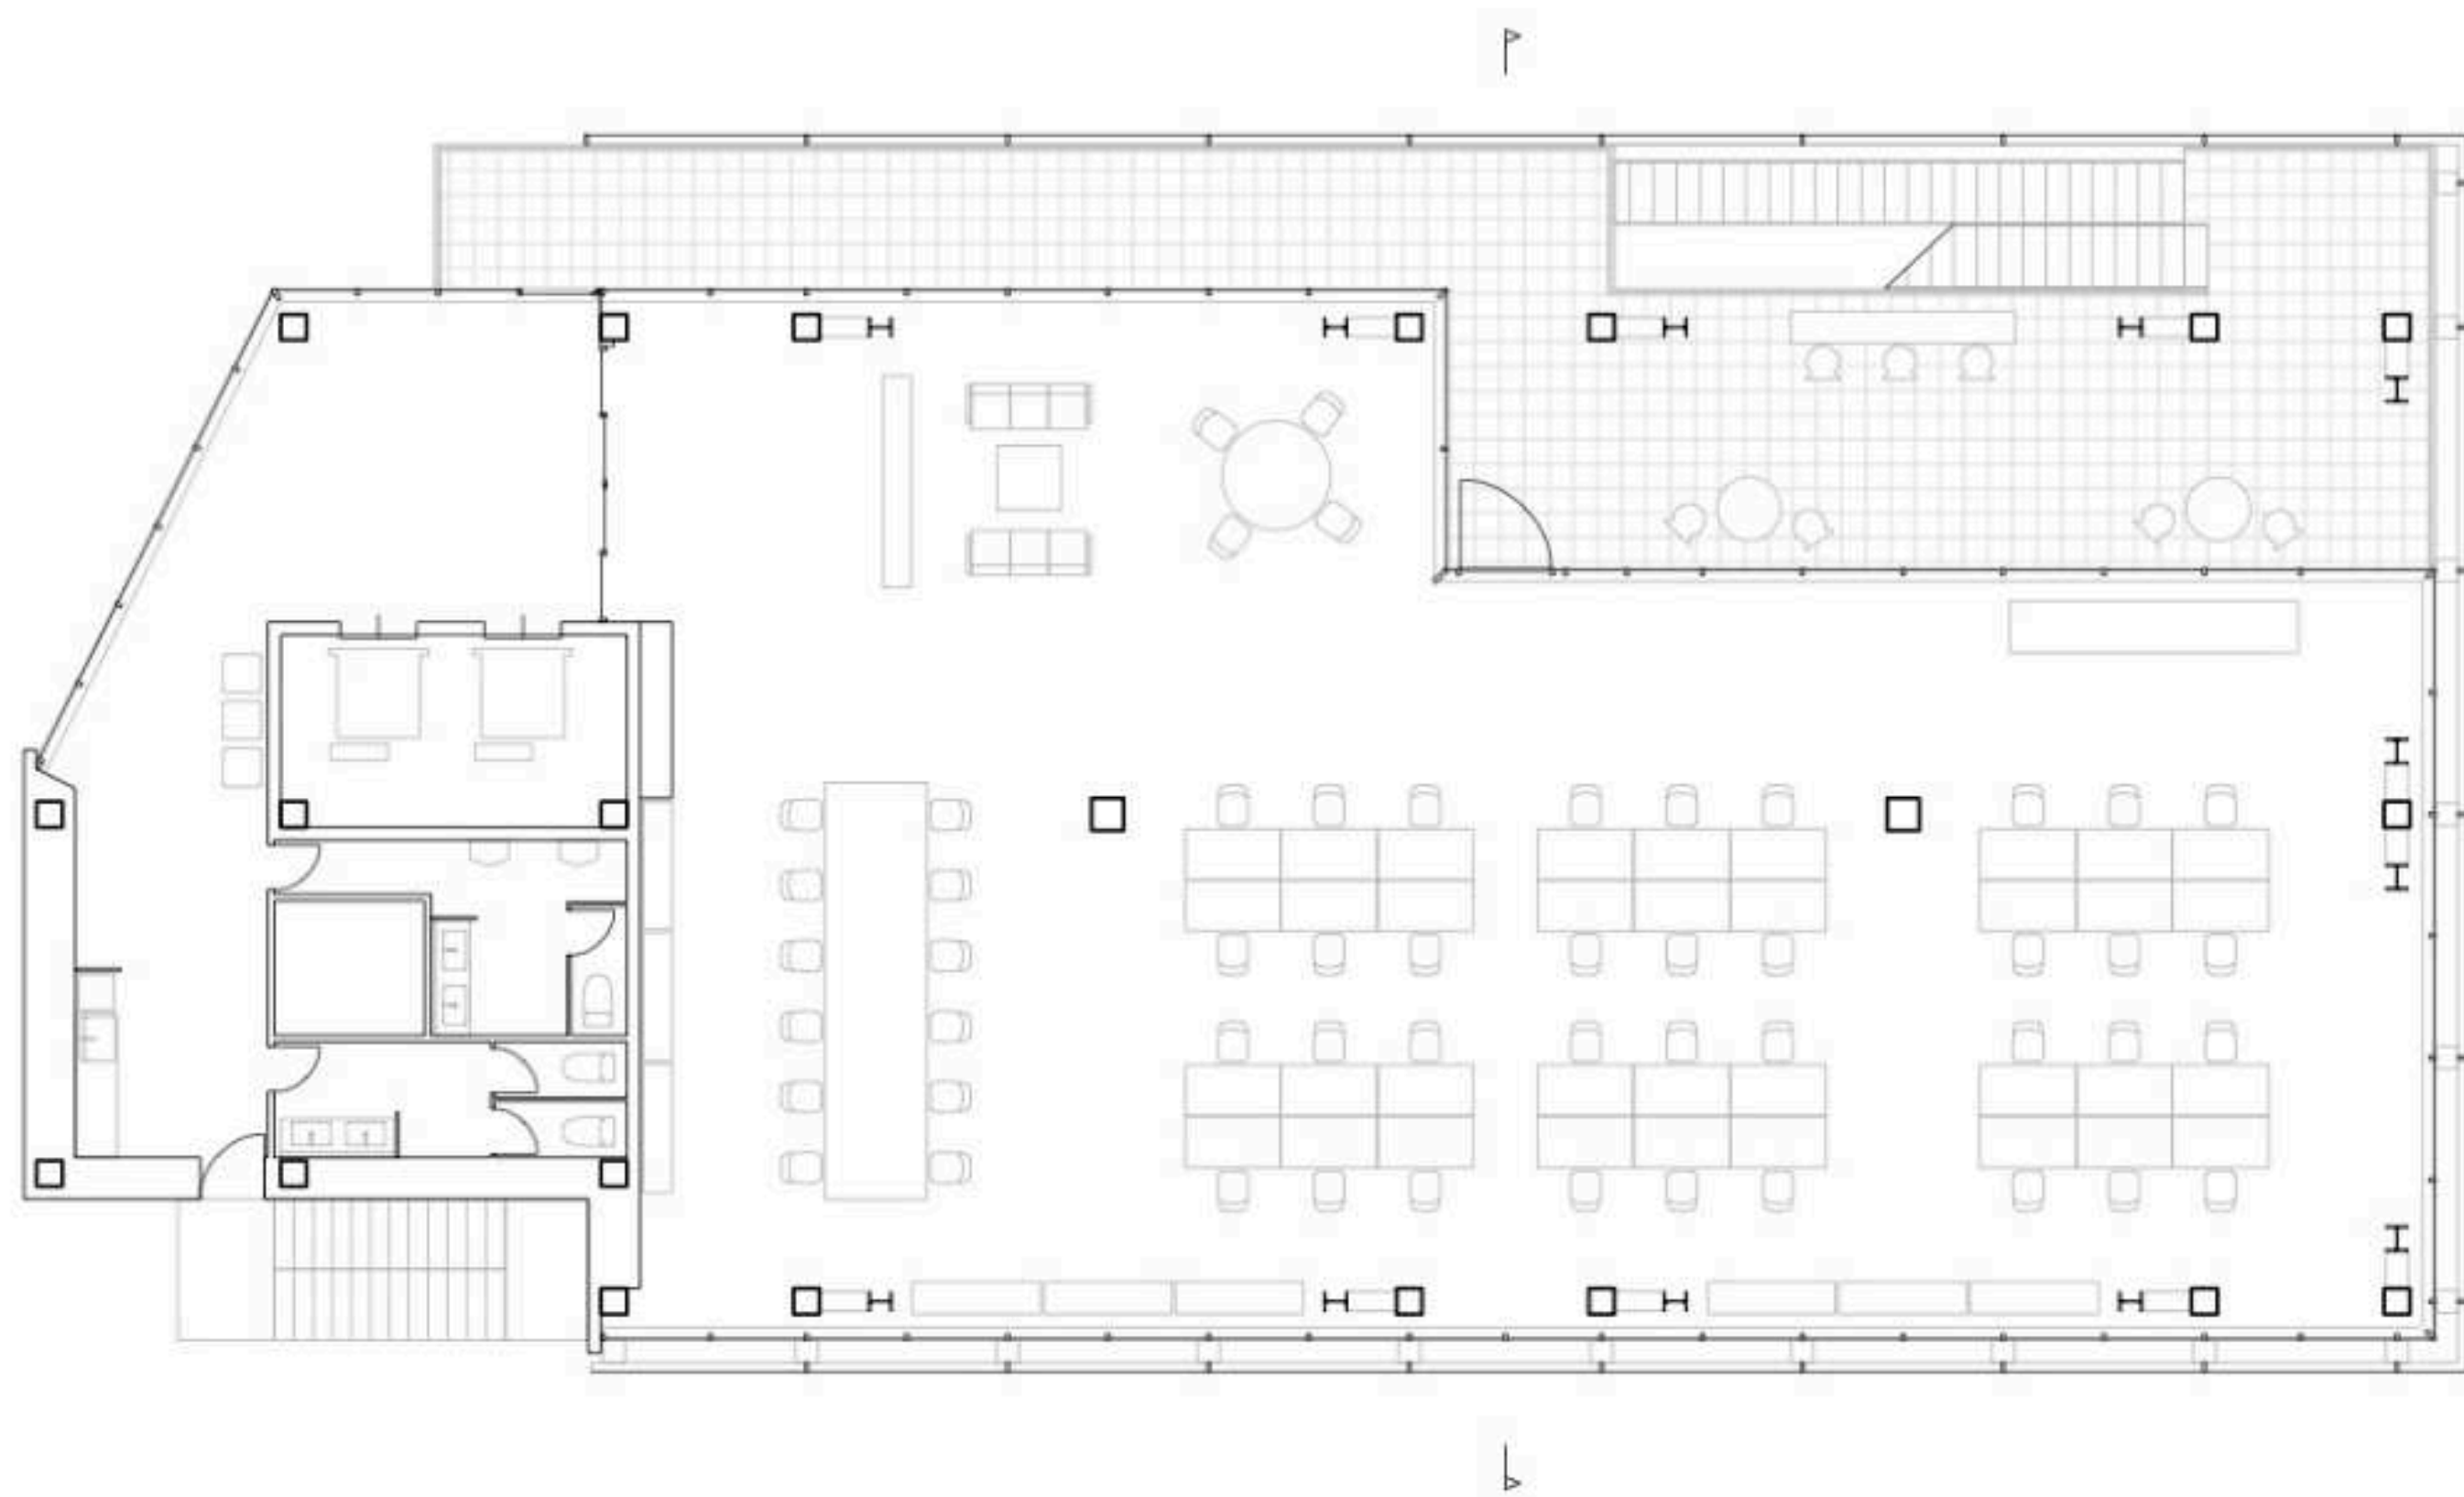


1/300 3F Plan Drawing

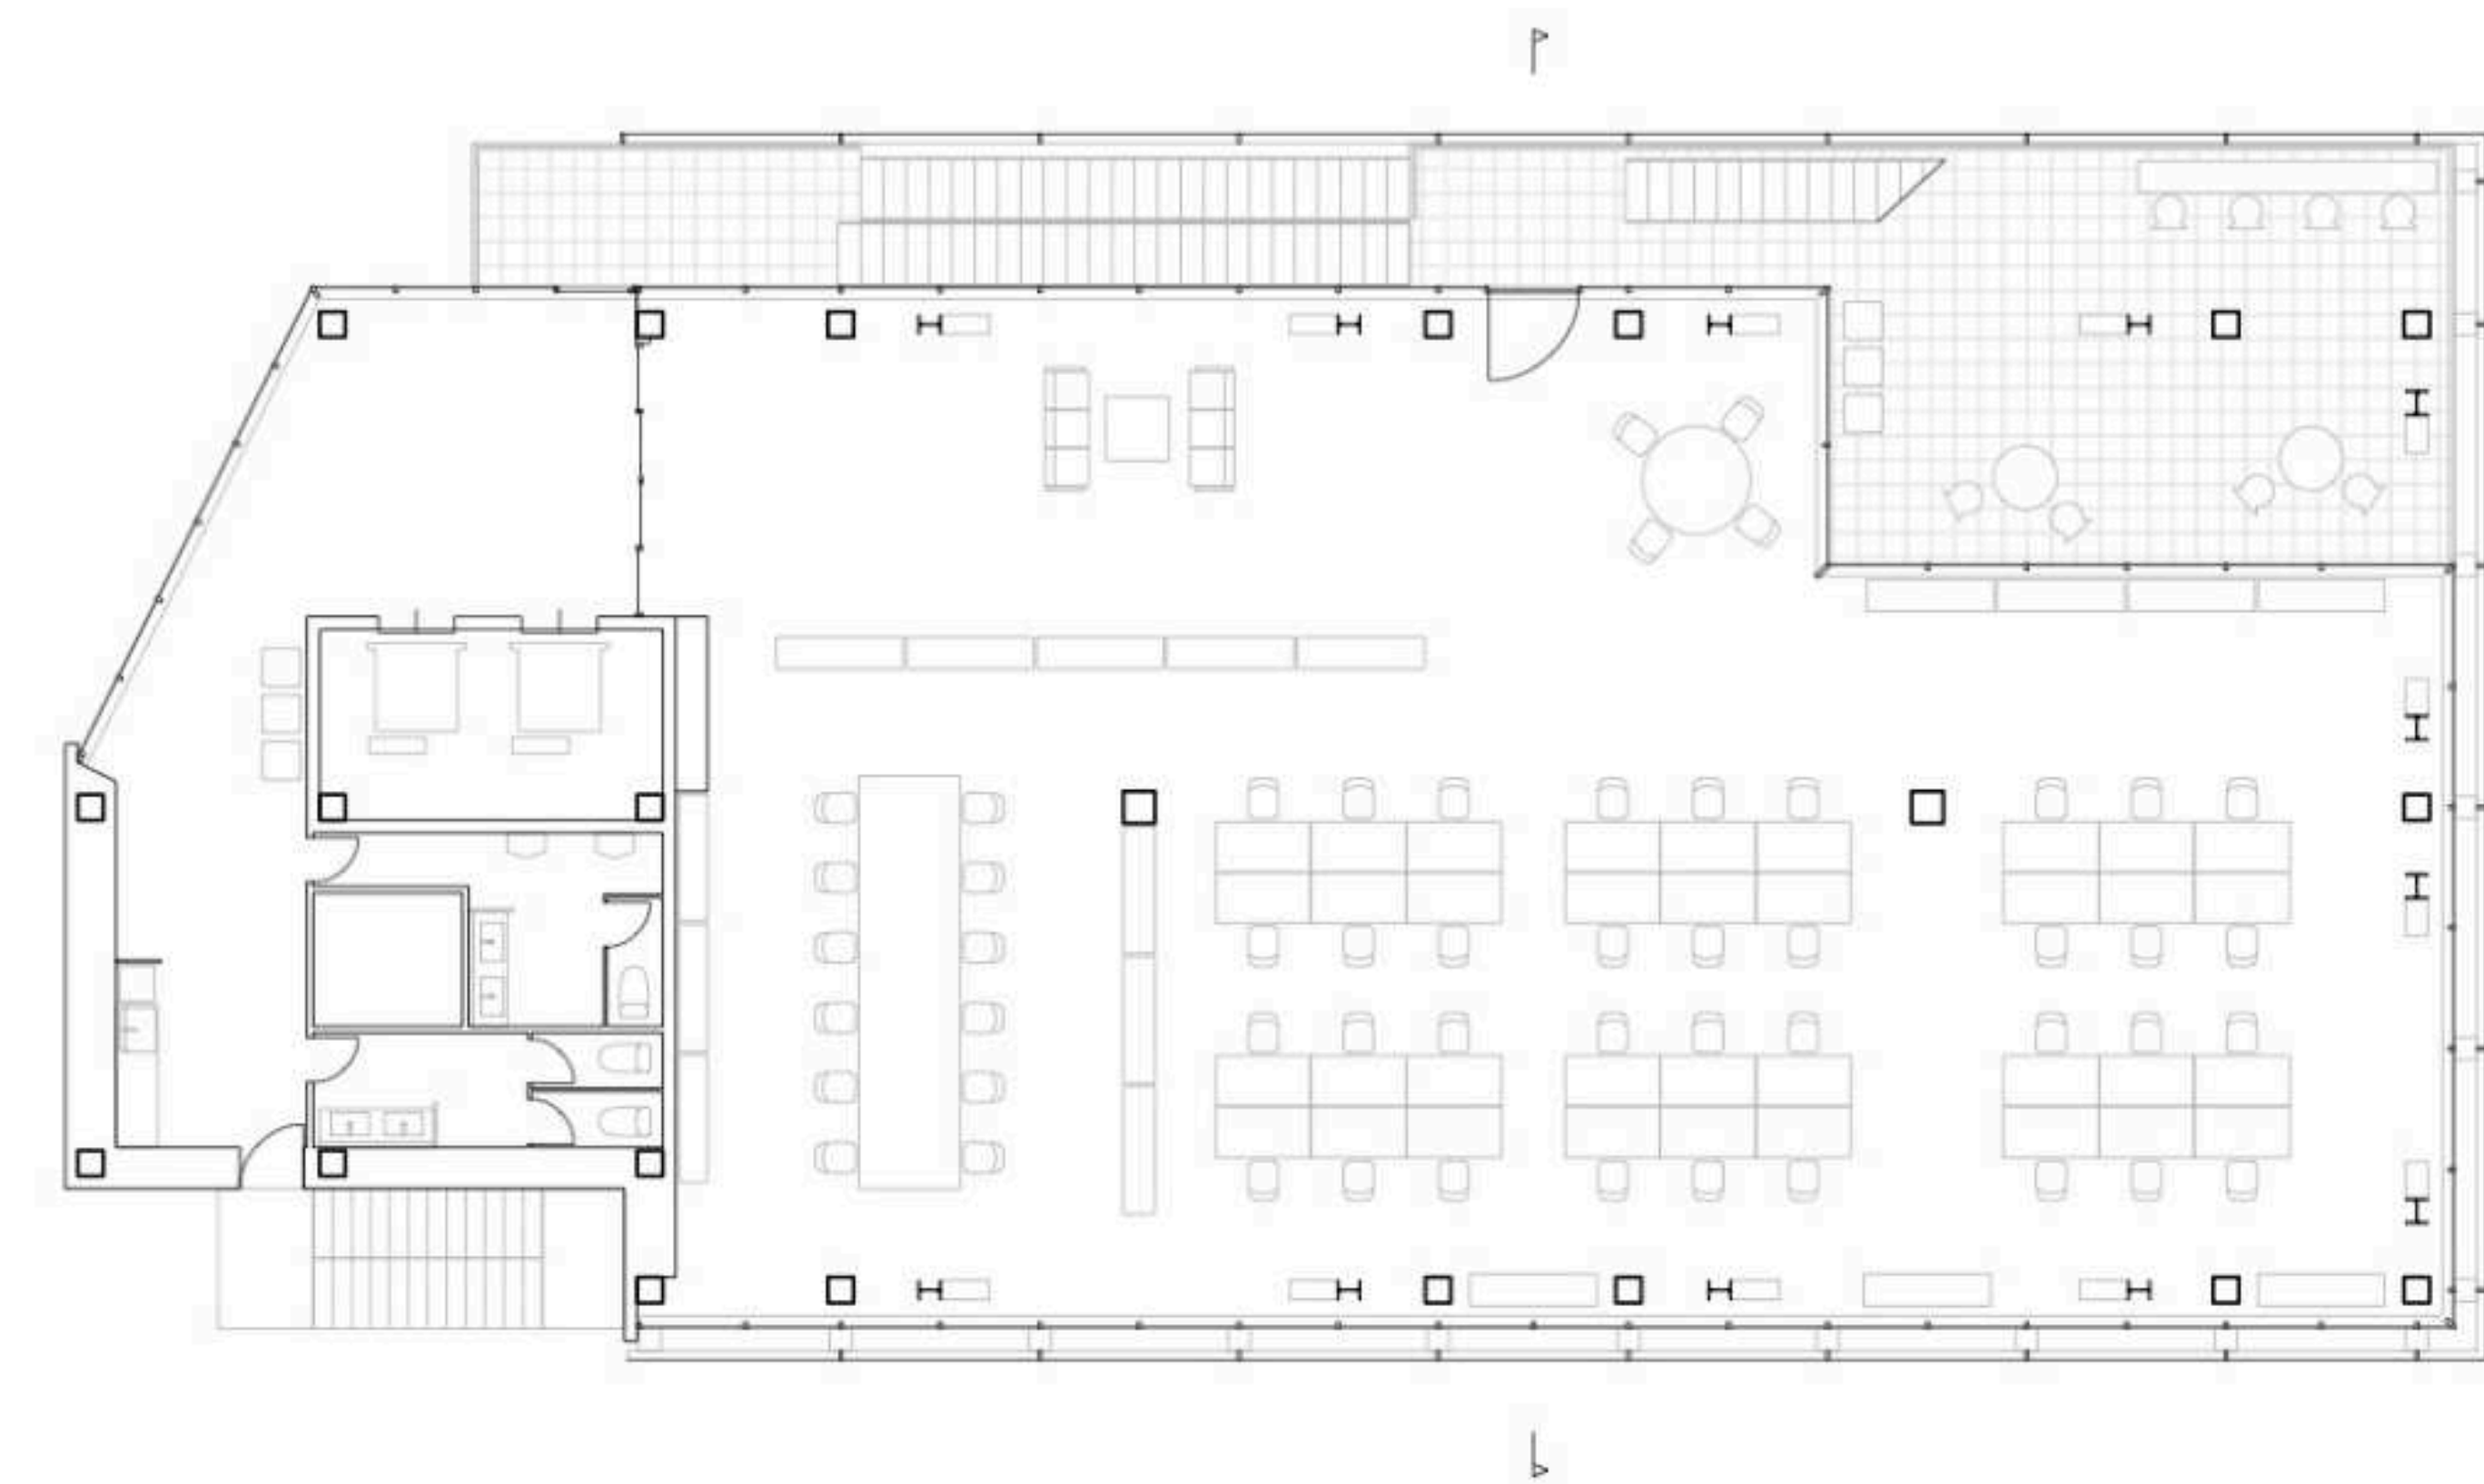

1/300 6F Plan Drawing

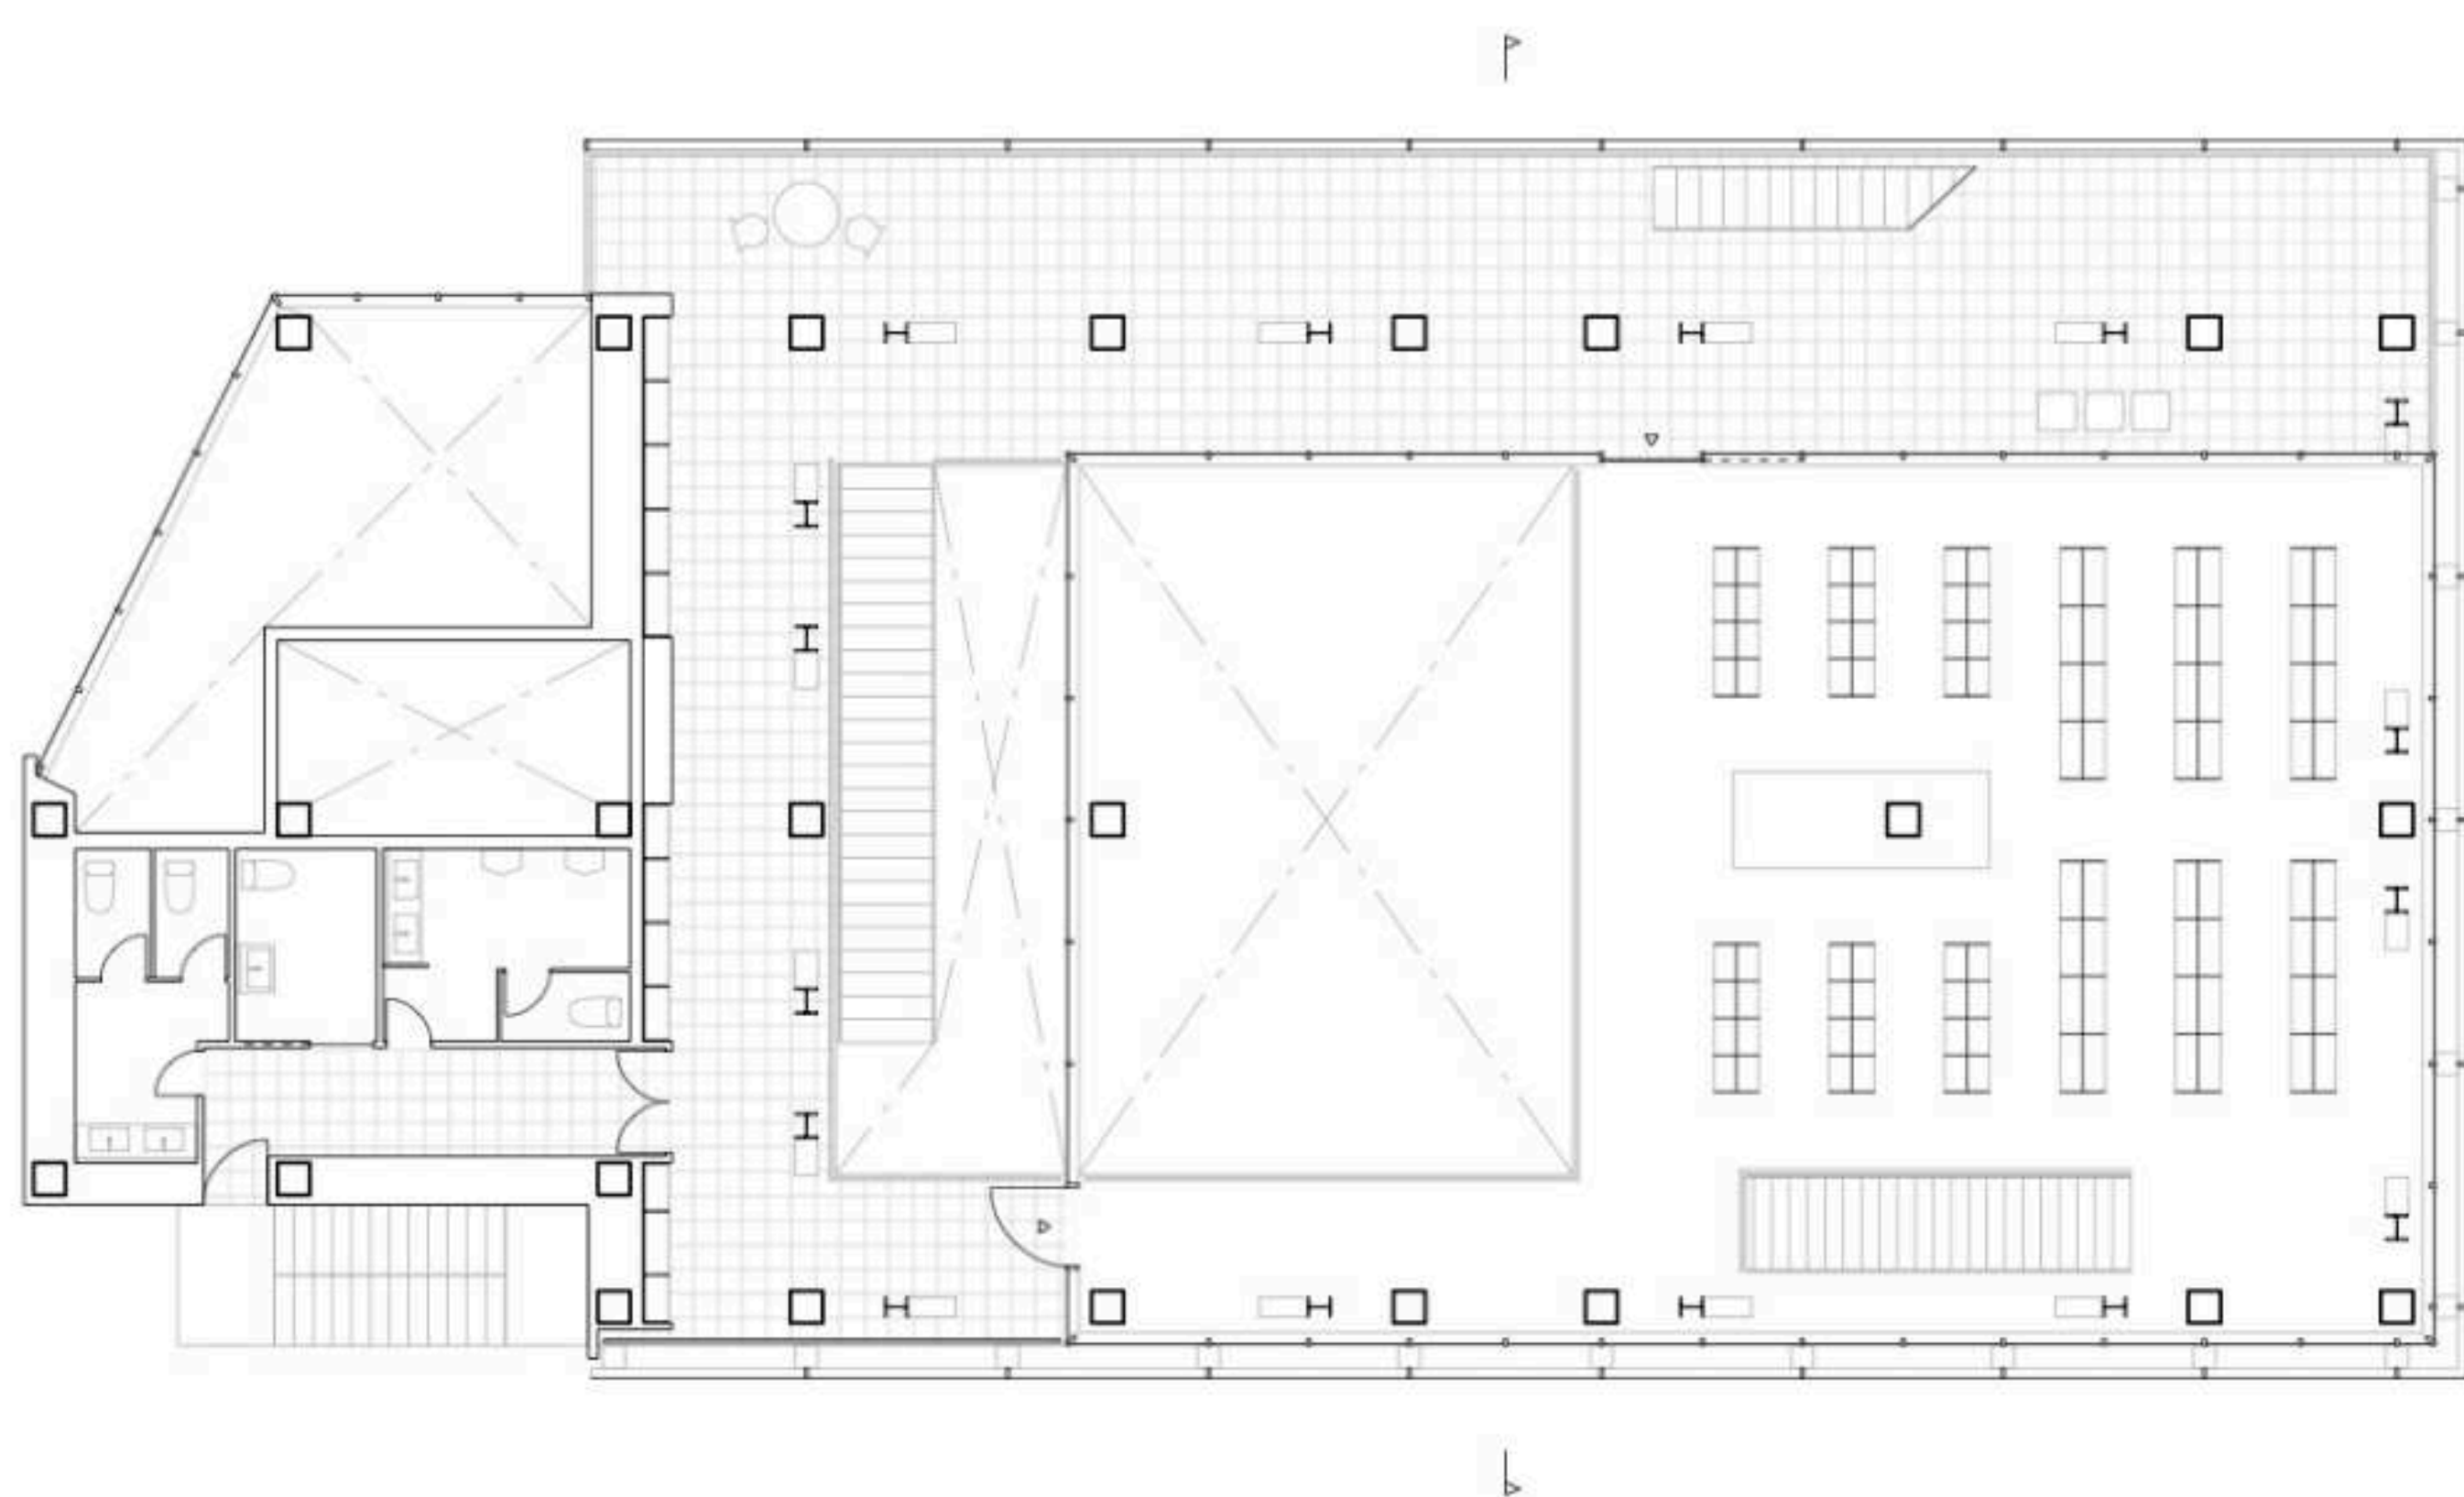

1/300 2F Plan Drawing

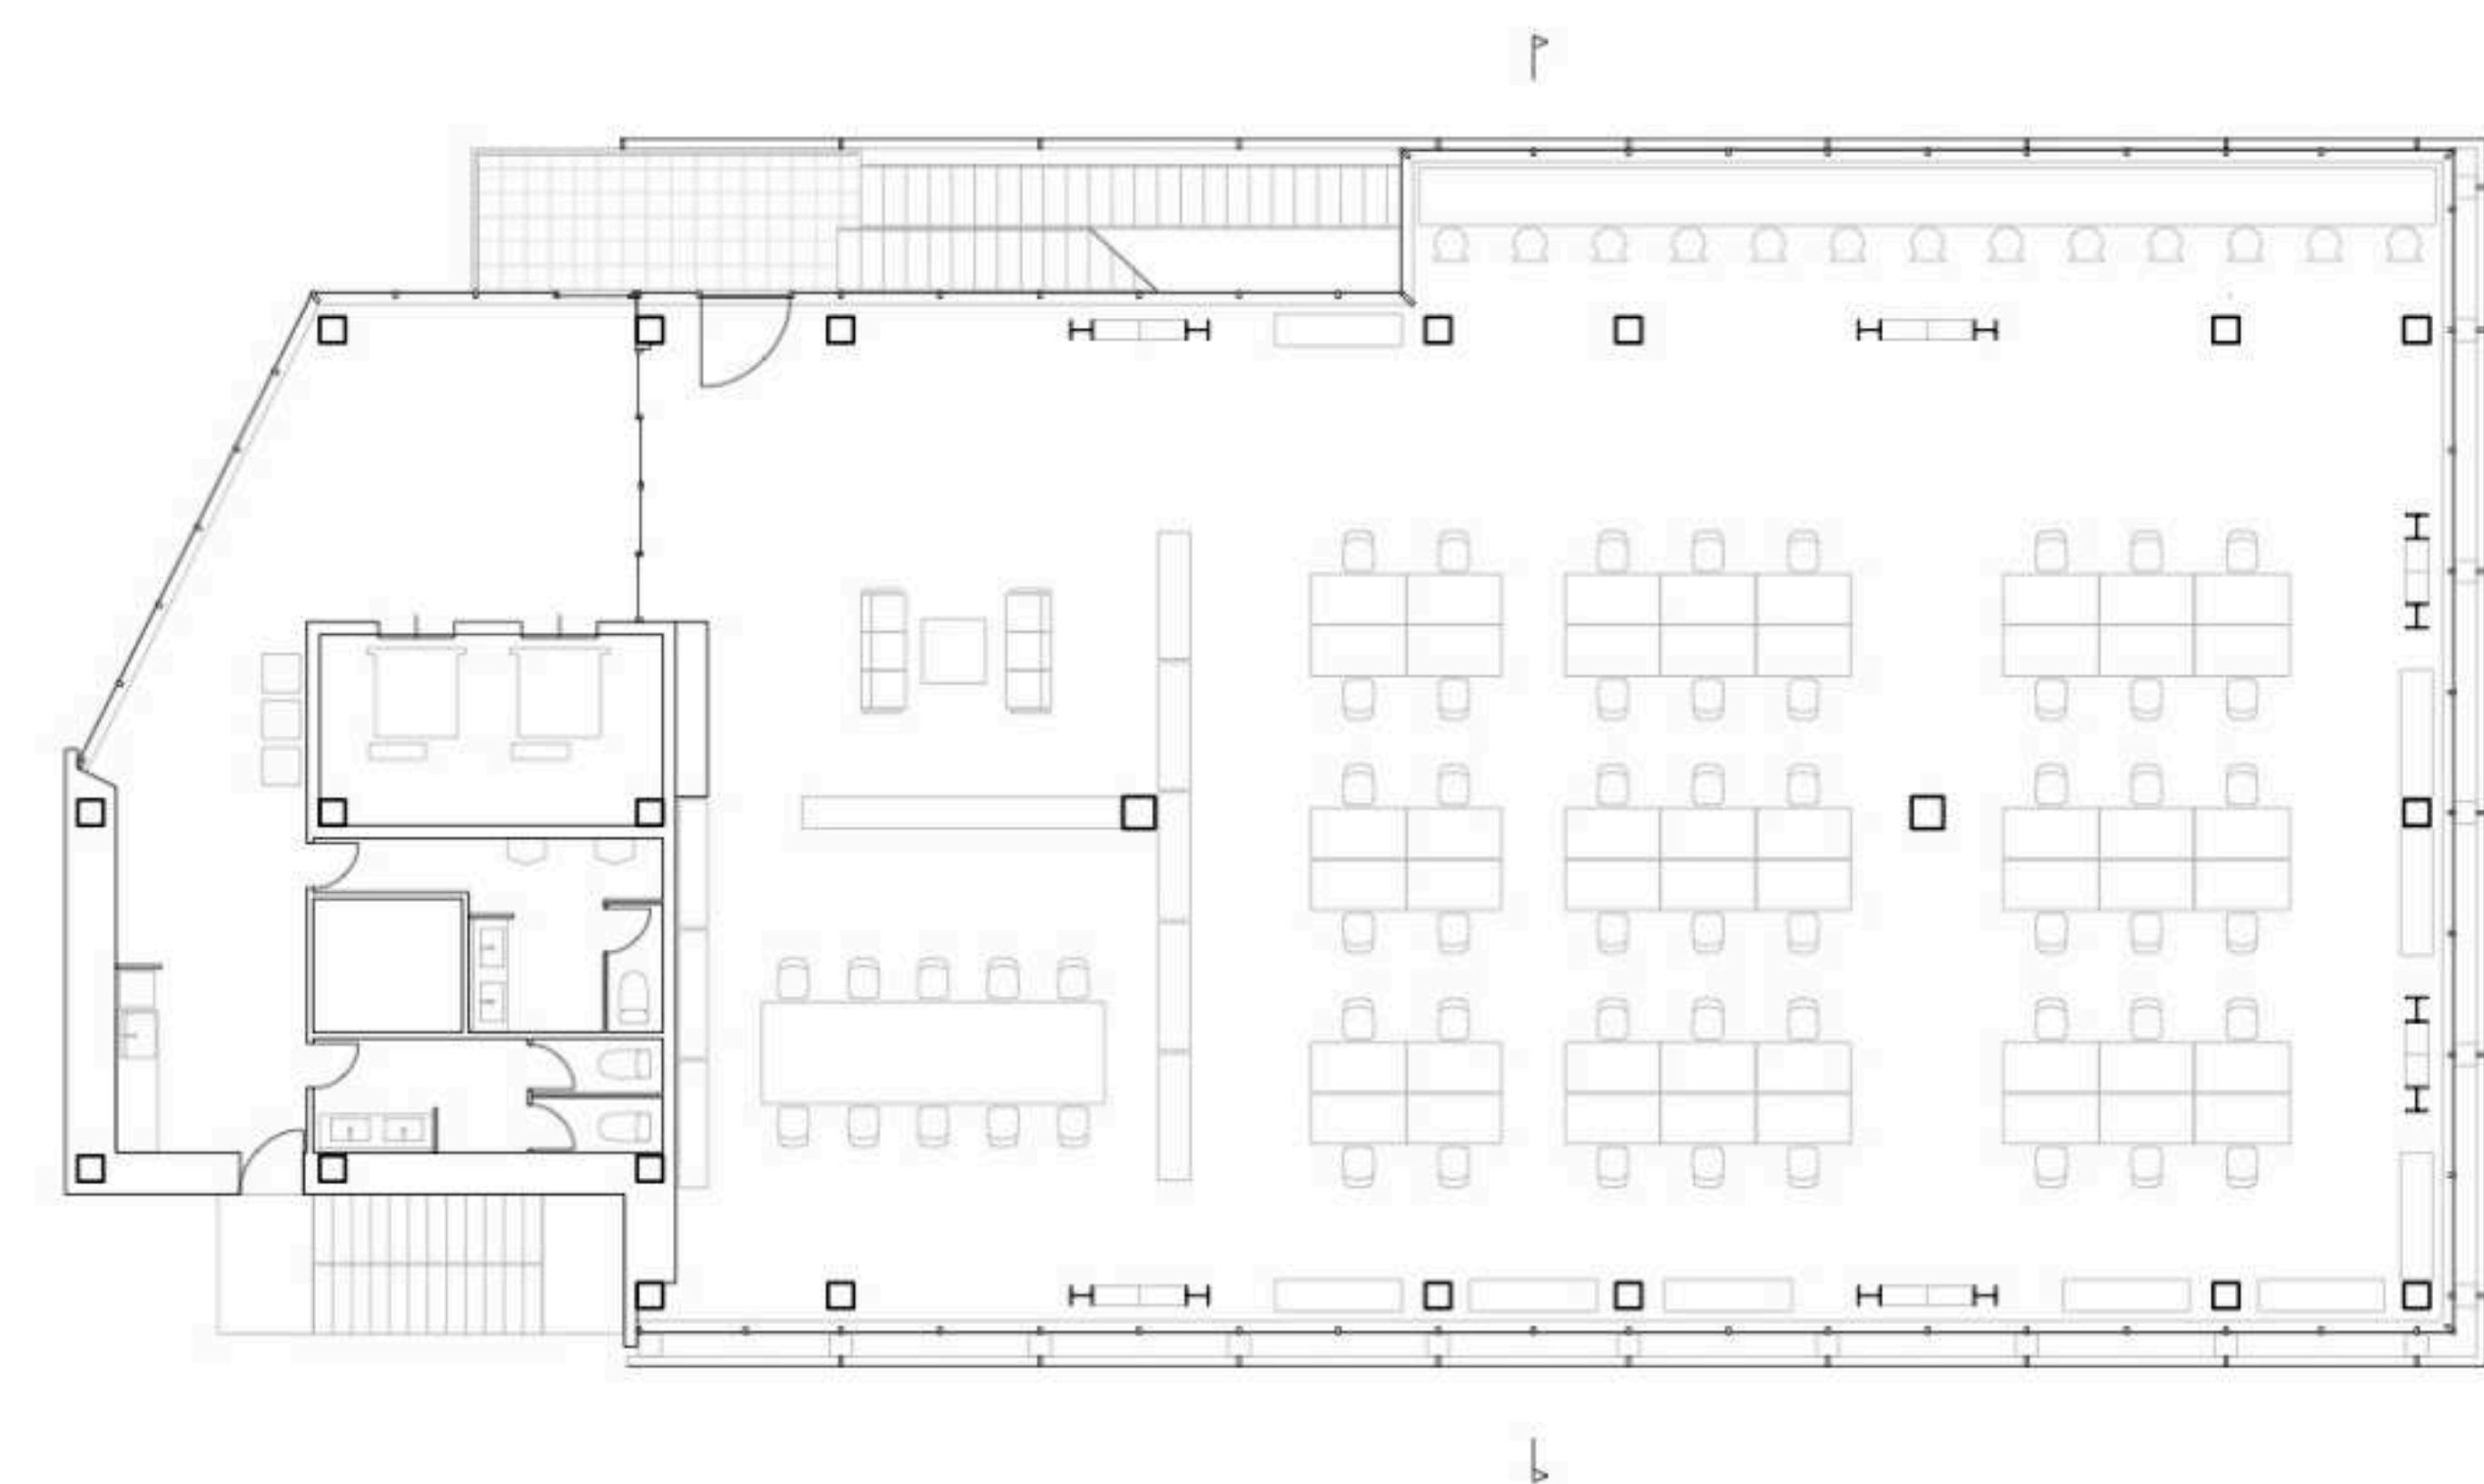

1/300 5F Plan Drawing

1. facade :


expanded metal mesh
150×16mm steel plate
2. outer wall :

corrugated galvalume steel sheet
vapor permeable waterproof sheet
calcium silicate board t=12.5+12.5mm
lip channel steel
plaster board t=12.5+12.5mm
glossy emulsion paint
3. terrace floor :

concrete tile t=40
water proof coating
concrete slab t=80
steel deck t=50
4. interior floor :


floor carpet
raised floor t=100
5. ceiling :

glossy emulsion paint
plaster board t=12.5+12.5mm

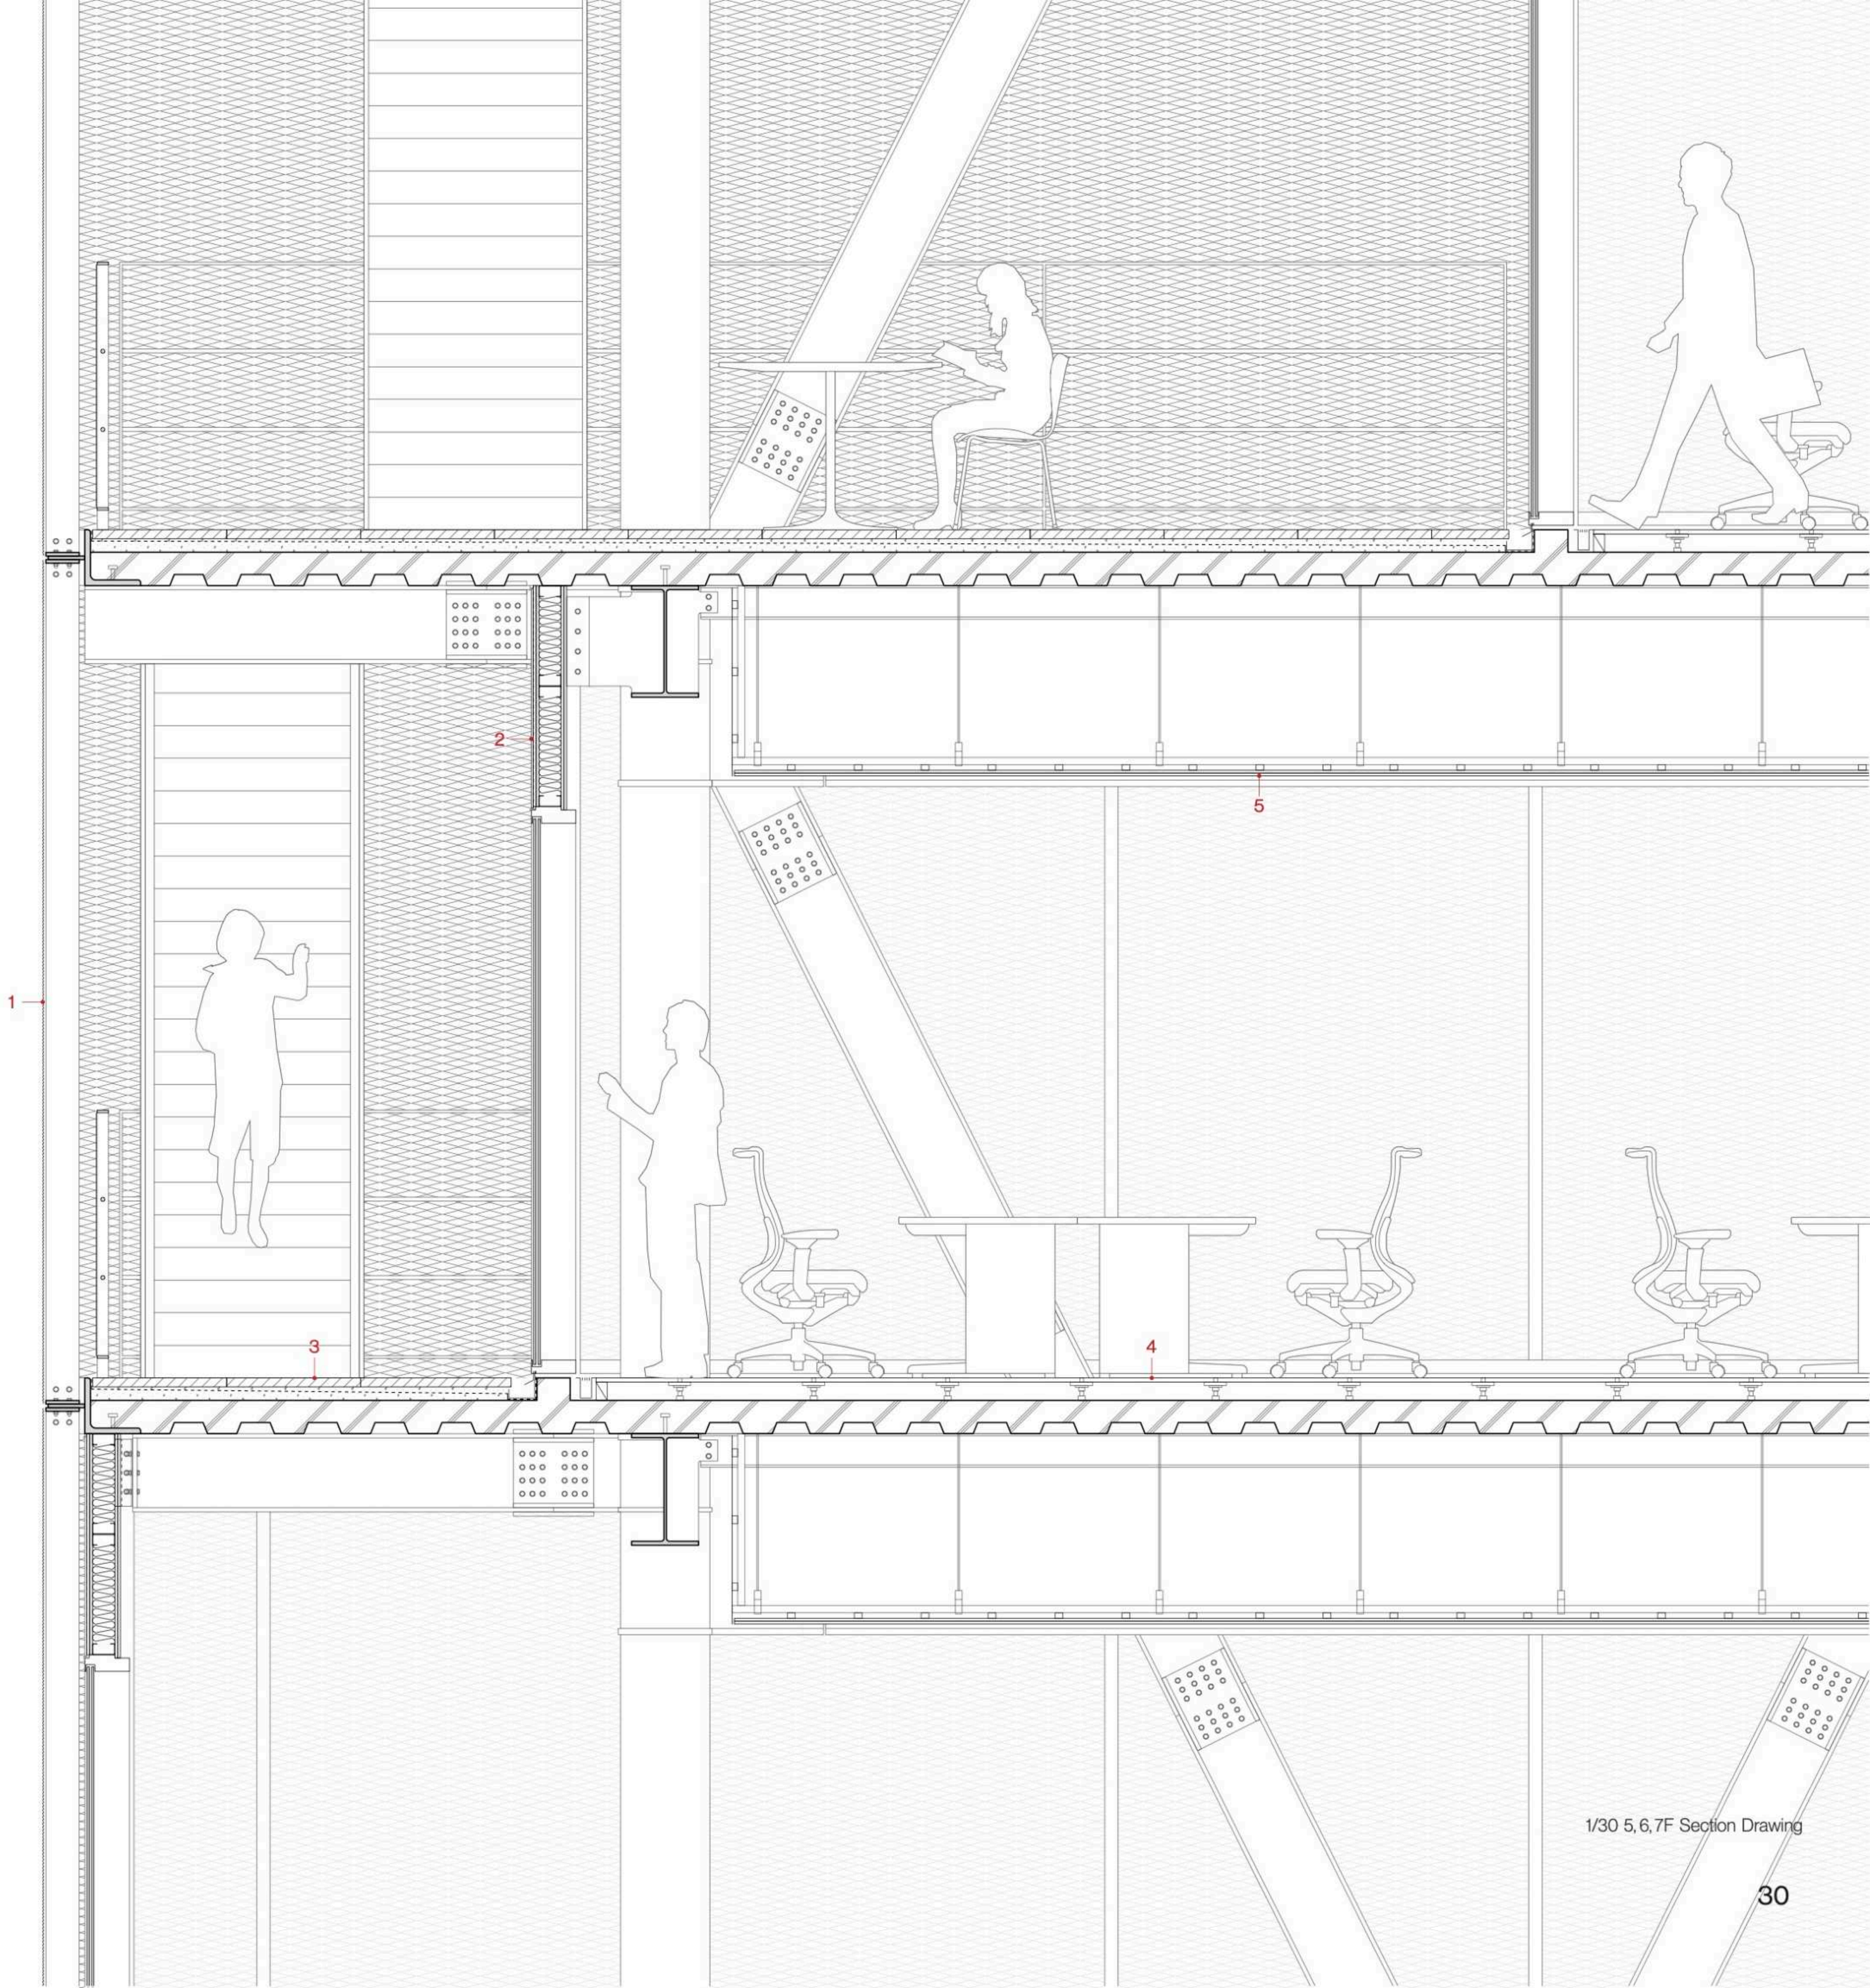

パブリックドローイング
東京計画 1960 丹下健三

Public Drawing
A Plan for Tokyo 1960 by Kenzo Tange

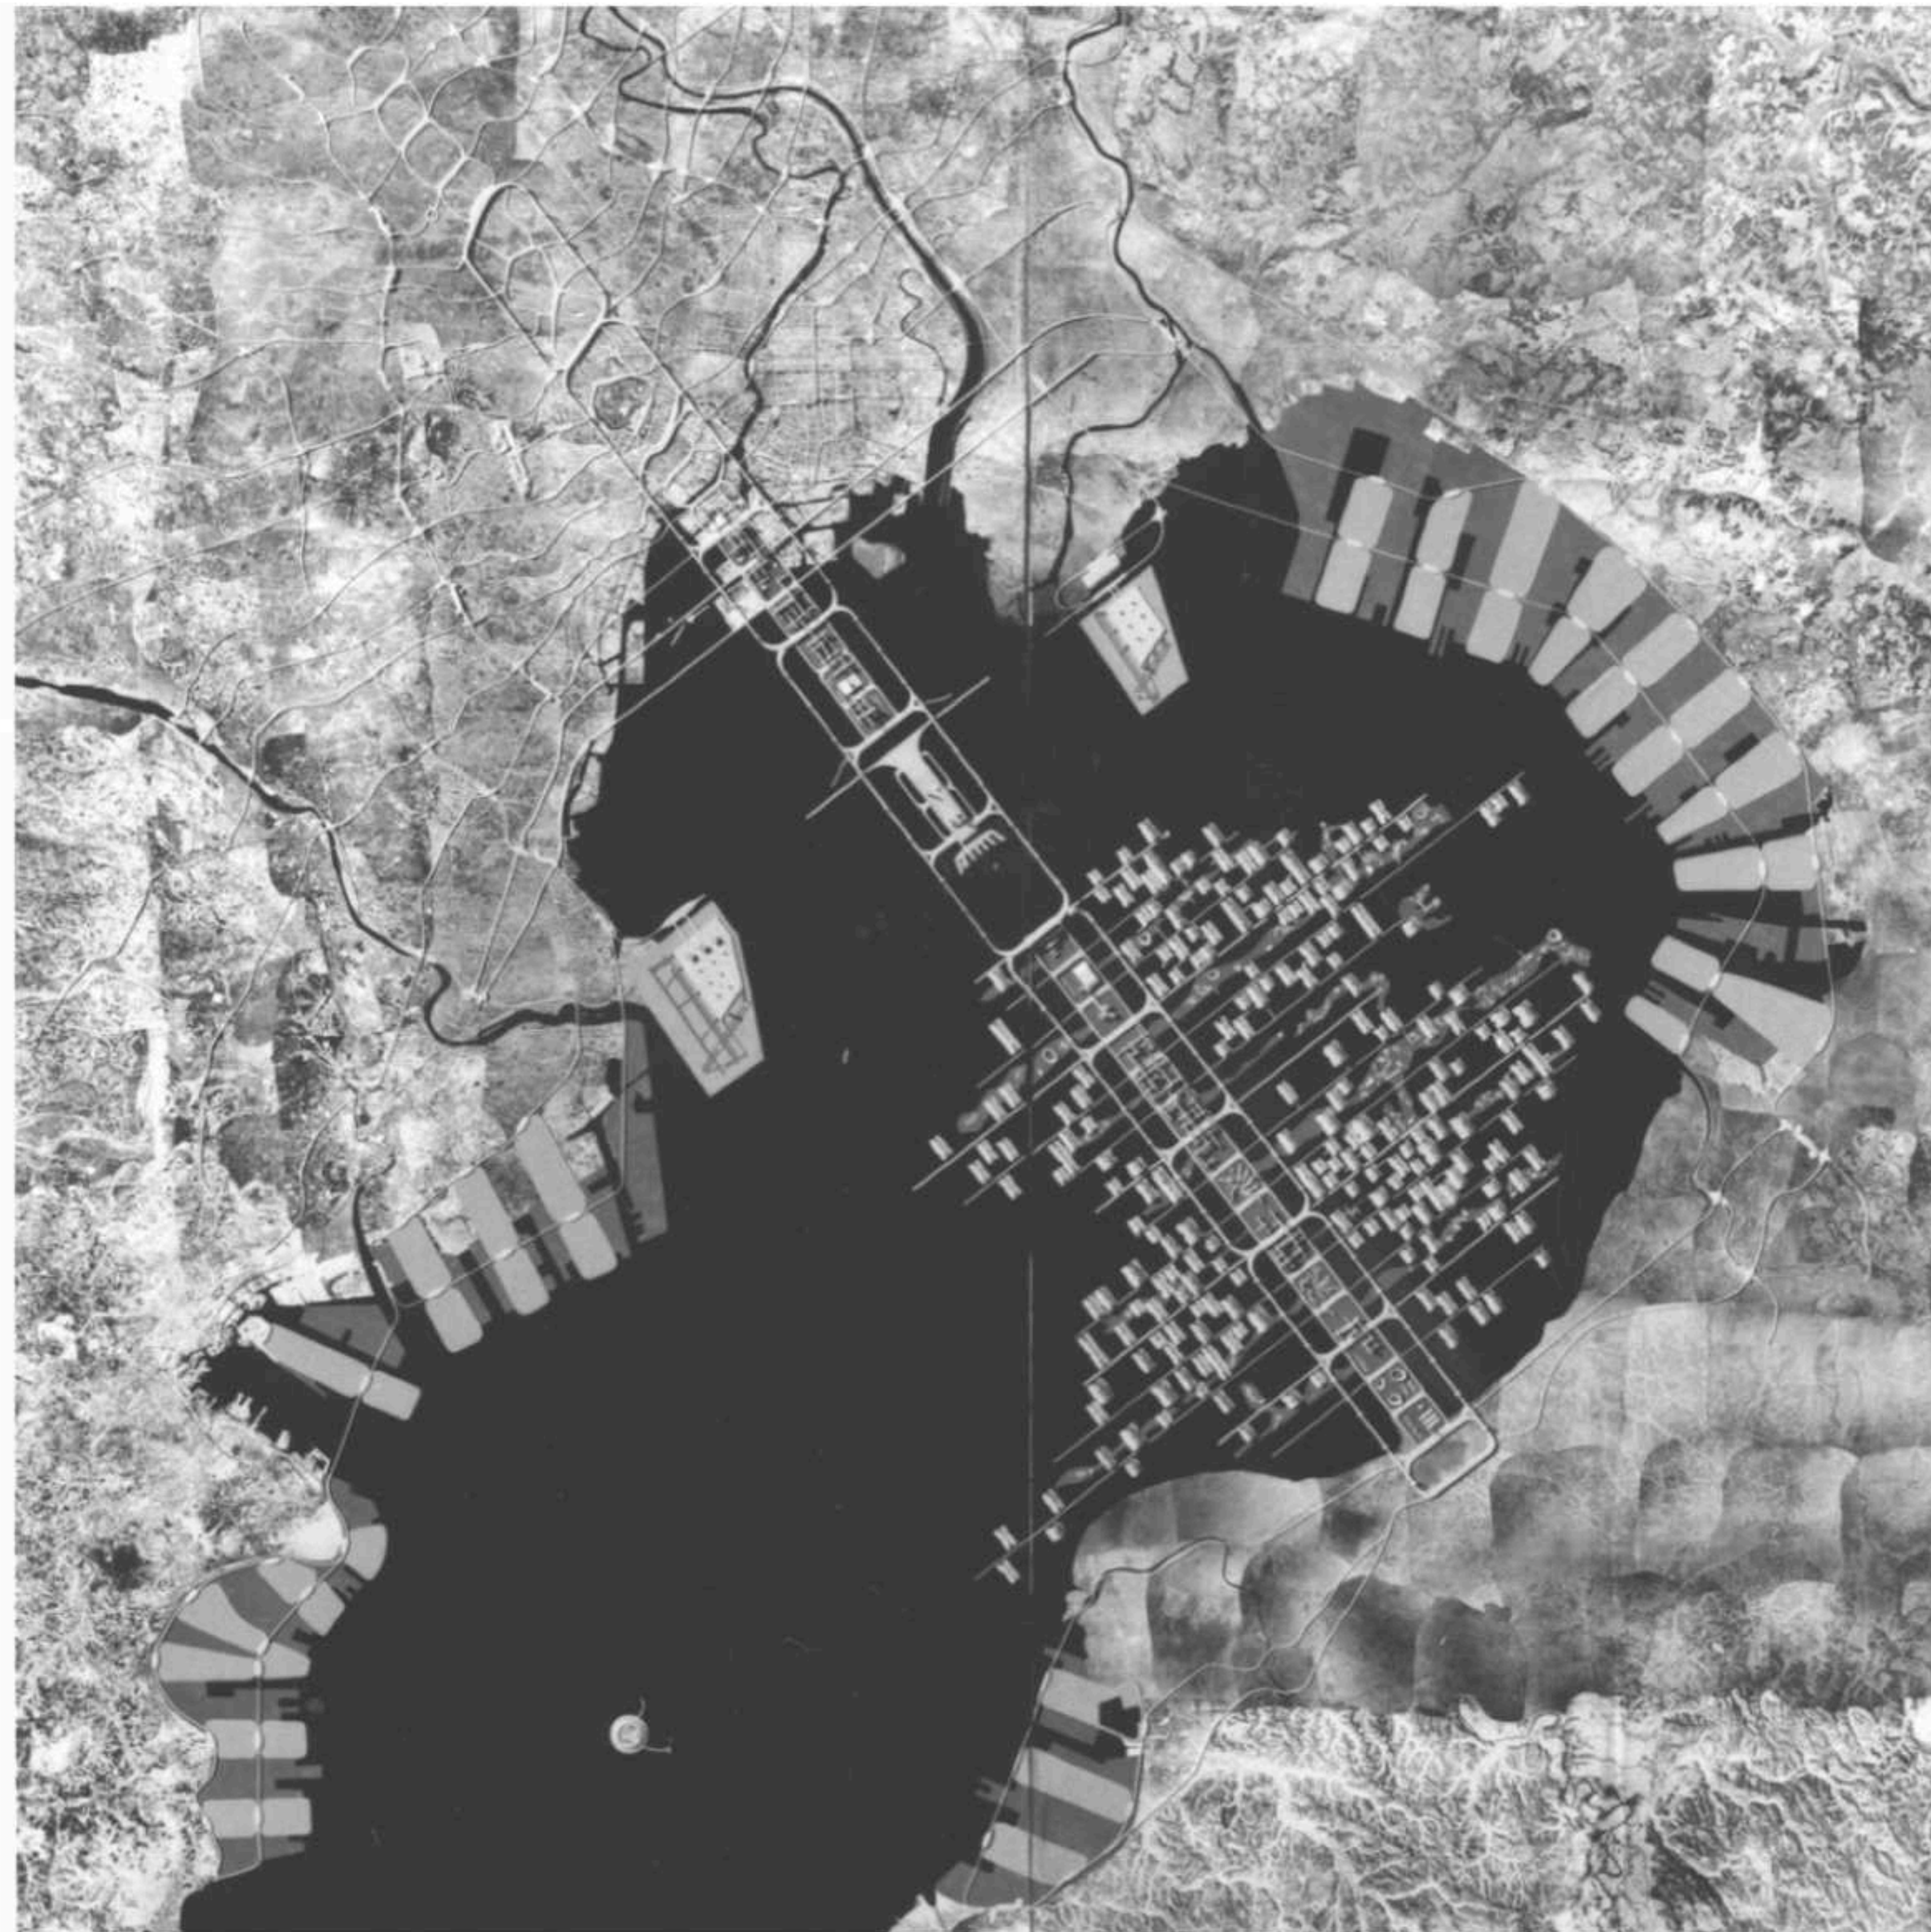

課題概要

大学院修士1年時に参加したグループワークスタジオの課題。留学生と英語でのディスカッションを行い、2週間で1200mm × 2400mm の模造紙に鉛筆と消しゴムのみを用いて記述した。

テーマは丹下健三の「東京計画 1960」。東京湾に浮かぶ巨大都市構想がもし実現していたら、現代ではどのような姿になっているかを一枚の紙の中に納めた。

Project Overview

This was an assignment from a group work studio undertaken during the first year of a master's programme. Discussions were conducted in English with international students, and the work was produced over two weeks on a 1,200 mm × 2,400 mm sheet of paper using only pencil and eraser.

The theme was Kenzo Tange's "Plan for Tokyo 1960" — a visionary proposal for a massive urban structure spanning Tokyo Bay. The drawing speculates on what this unrealised megastructure might look like today had it actually been built, capturing that imagined present within a single sheet.

ふるまいの記述

当計画は、環状道路によって囲まれた各エリアと、主要な構造物に直行する方向に伸びる栈橋状のエリアから成る 12 の地区から成り、それぞれ明確に機能が分かれている。授業では、グループごとに居住エリア、商業エリア、インフラエリアなどがそれぞれ割り当てられた。

私たちのグループは、行政・立法・司法地区が割り当てられ、丹下研究室が残した数少ない模型写真や平面図を元に、この地区での建物の機能配置や動線について留学生とともに話し合った。そして最終的なドローイングでは、左から、A: 司法、B: 行政、C: 立法というように建物ごとに機能を明確に分断しており、足元には国民のための広場が広がっている。


このように、丹下による民主主義的な理想を読み取り、人々のふるまいを記述した。

A Notation of Human Behaviour

The plan comprises twelve districts, each with a clearly defined function: areas enclosed by ring roads, and pier-like zones extending perpendicular to the primary structural axes. In the studio, each group was assigned a specific district — residential, commercial, infrastructural, and so on.


Our group was responsible for the administrative, legislative, and judicial district. Working from the limited number of model photographs and floor plans left by the Tange Laboratory, we discussed with international students the functional arrangement of buildings and the organisation of circulation within this district. In the final drawing, the functions are clearly delineated building by building from left to right — A: Judiciary, B: Administration, C: Legislature — with a civic plaza for the public spreading across the ground level below.

In this way, we interpreted the democratic ideals embedded in Tange's vision and gave form to the anticipated behaviours and movements of its inhabitants.

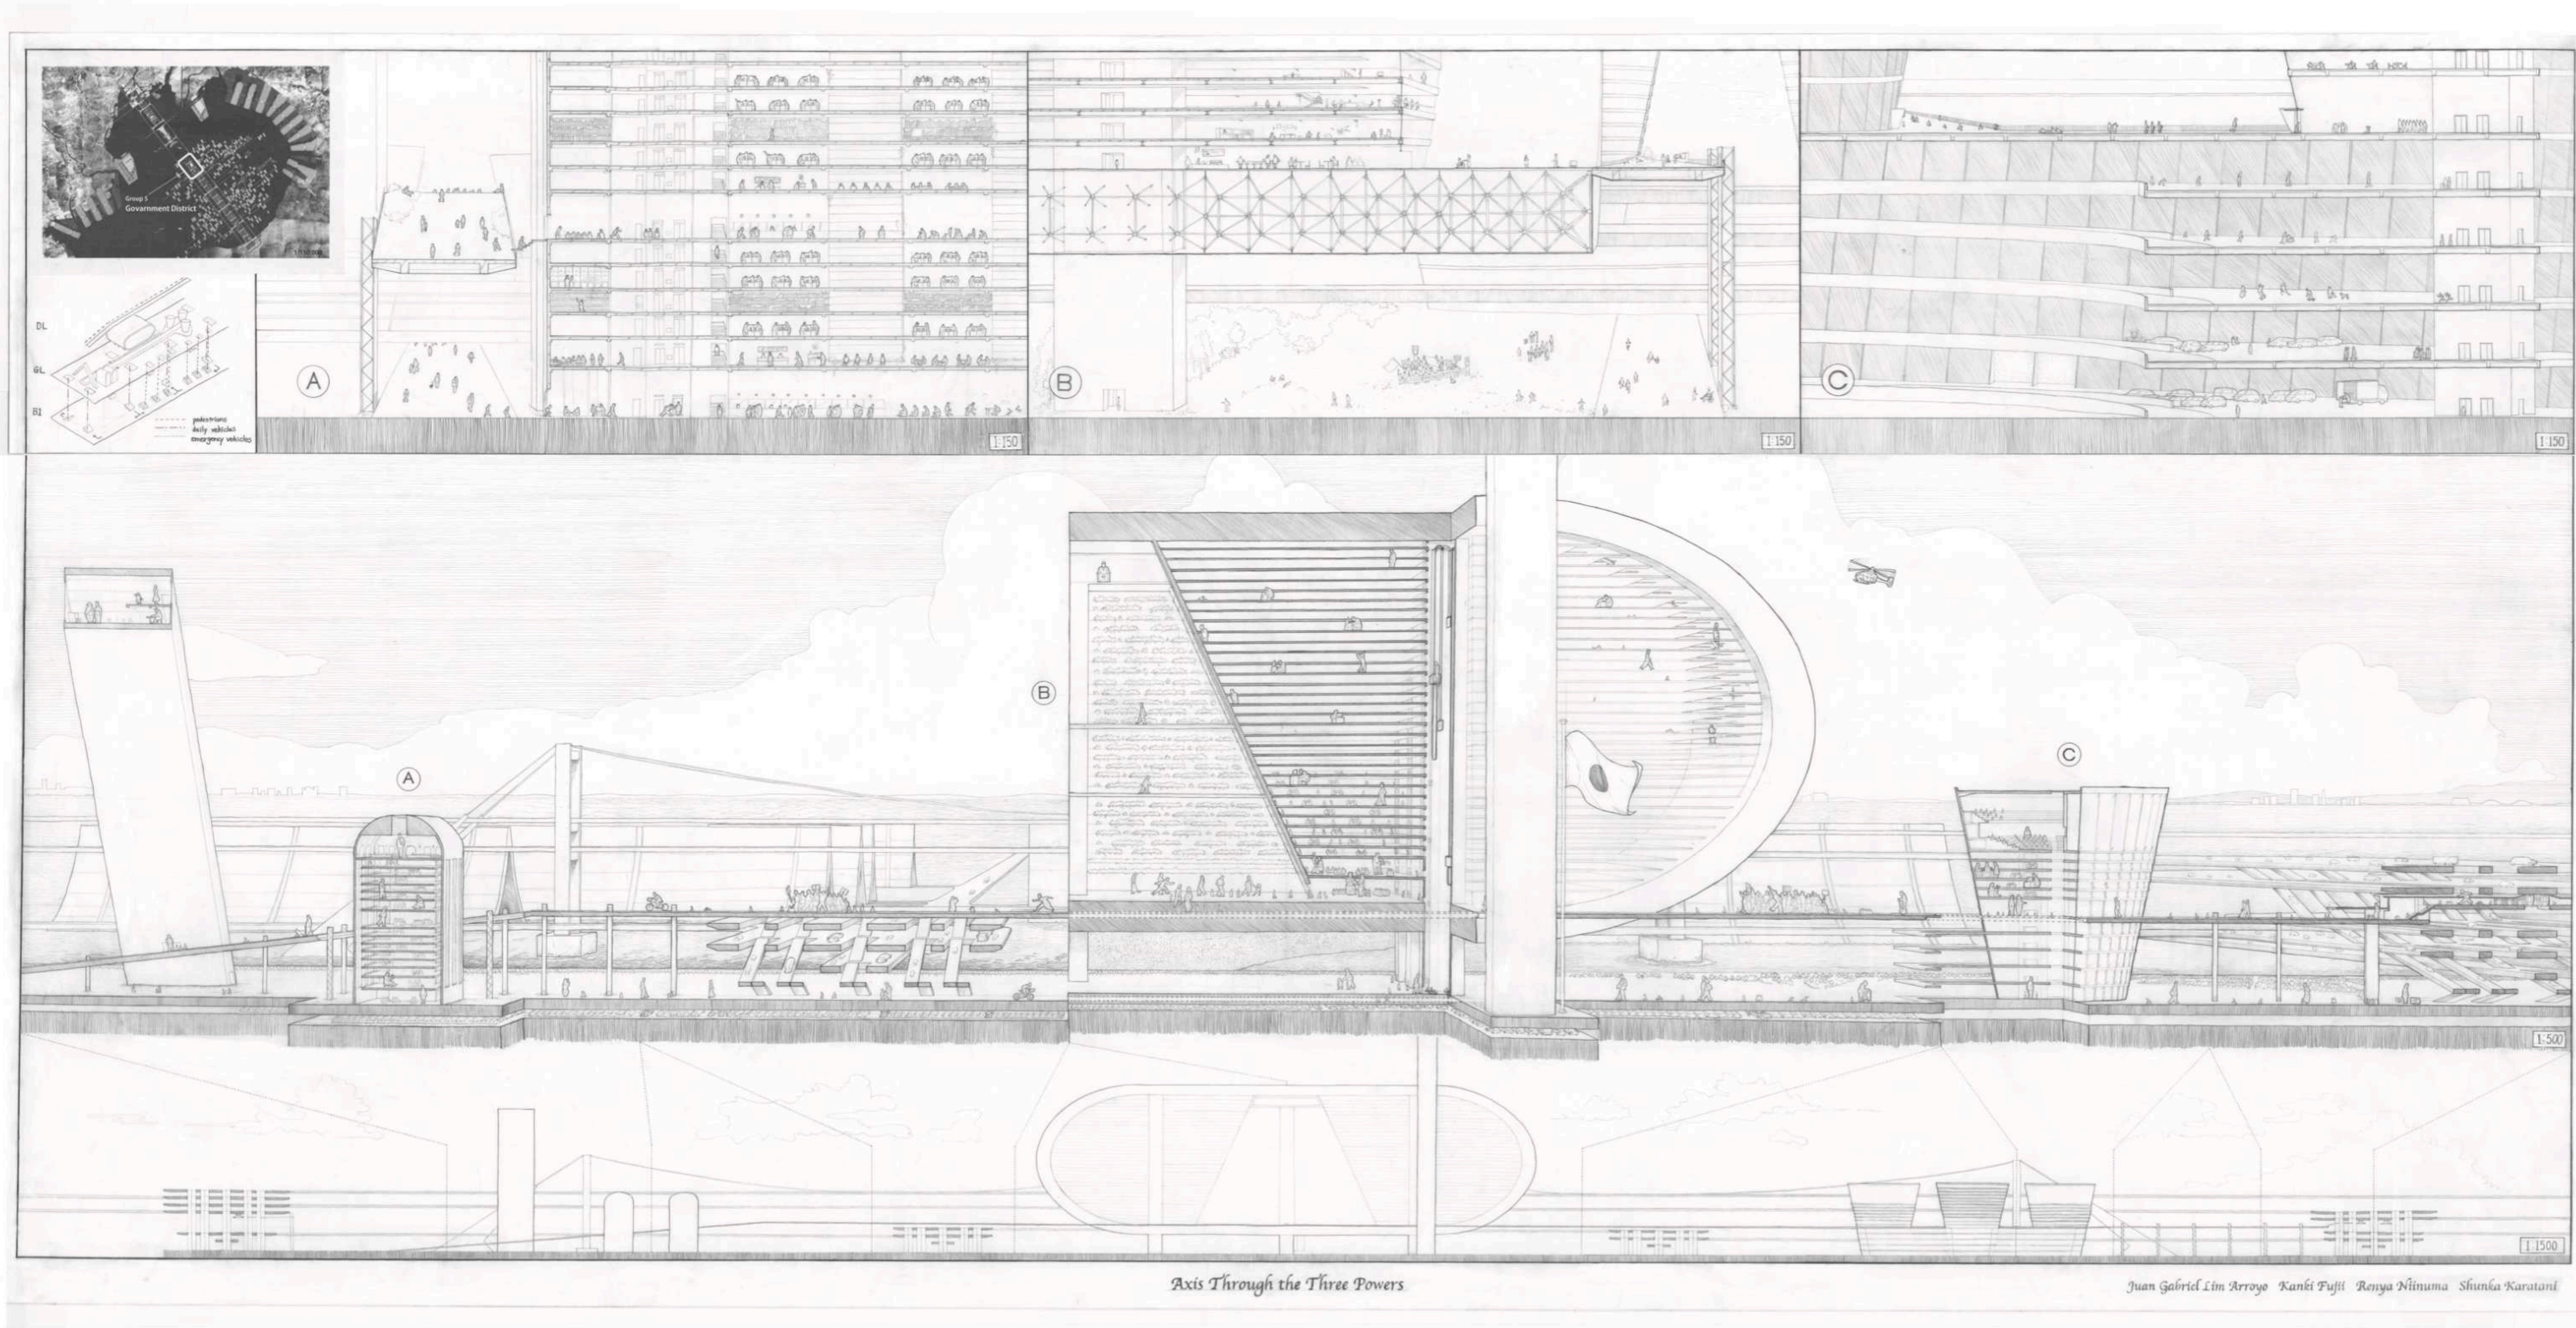

過去案の模型

Models of previous ideas

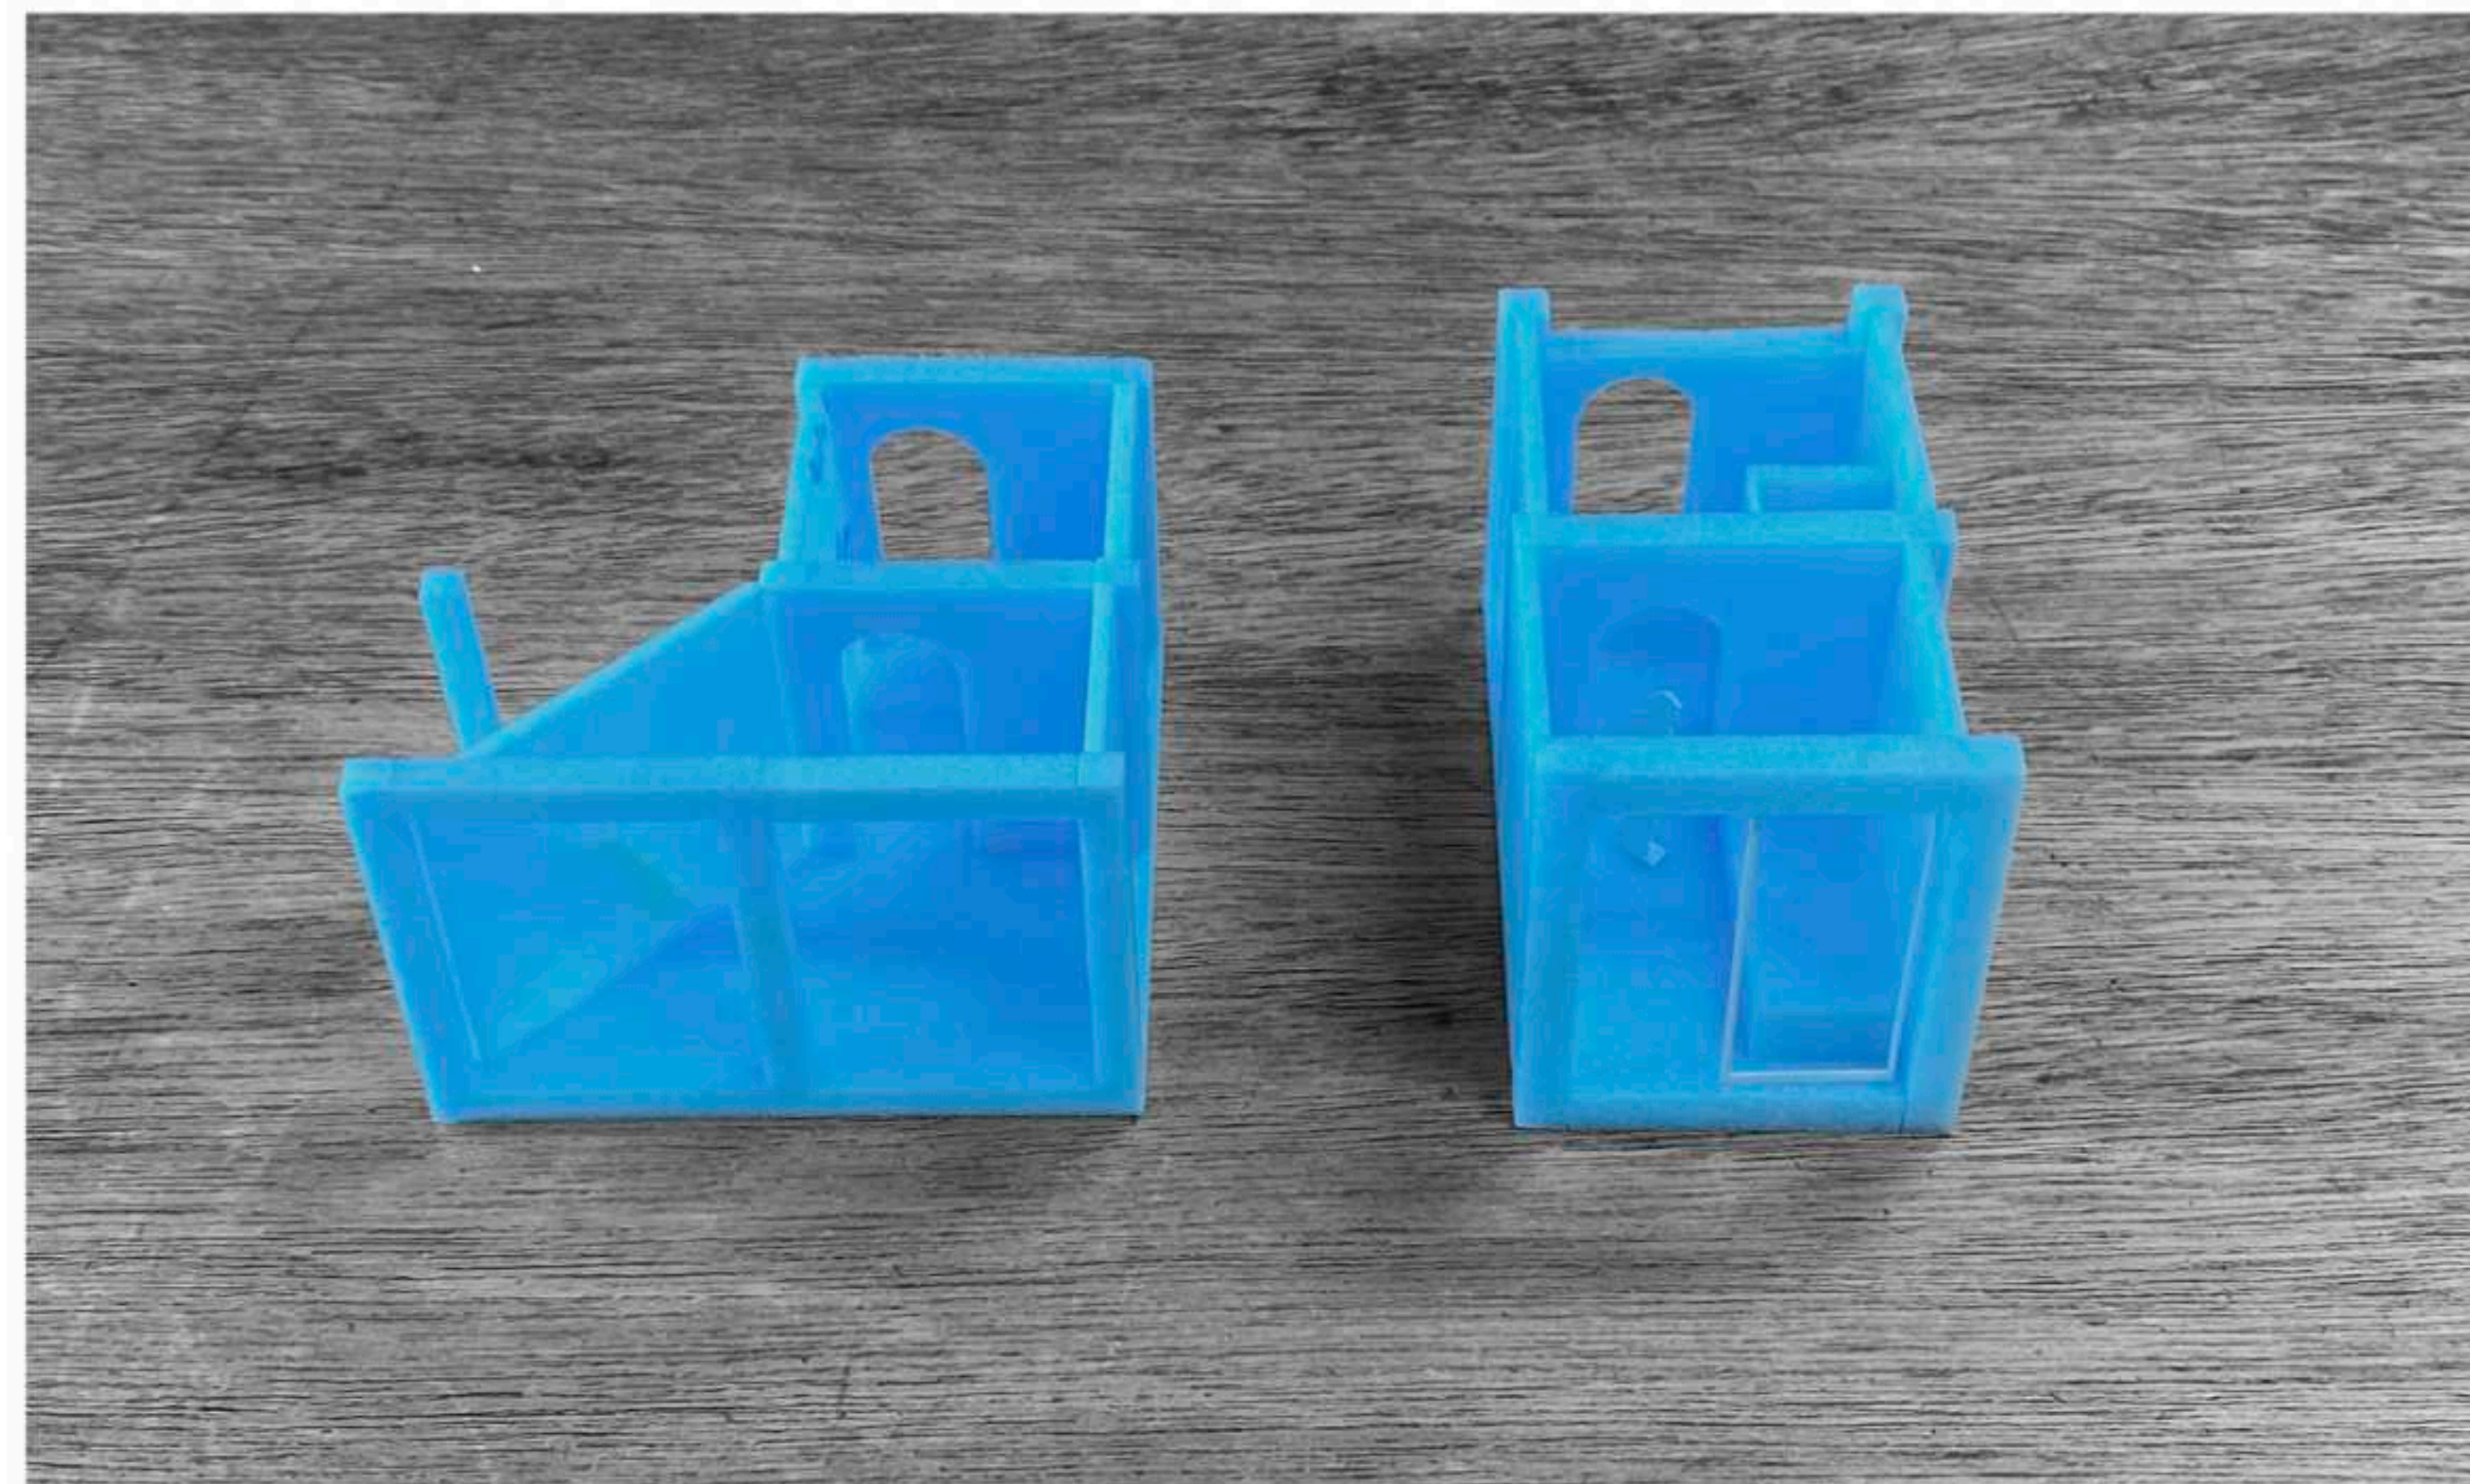

掲載作品のうち、学部2,3年次に作成した当時の案の模型をまとめた。


一ヶ月ほどのスタジオの期間のうちに、可能な限り抽象的で、かつ建築を構成するマテリアルのイメージが湧き上がる表現を目指した。

This section brings together models made at the time of the original proposals, produced during the second and third years of undergraduate study, selected from the works featured in this portfolio.

Within the studio period of approximately one month, the aim was to achieve representations that were as abstract as possible, while simultaneously evoking a tangible sense of the materials that would constitute the architecture.



A

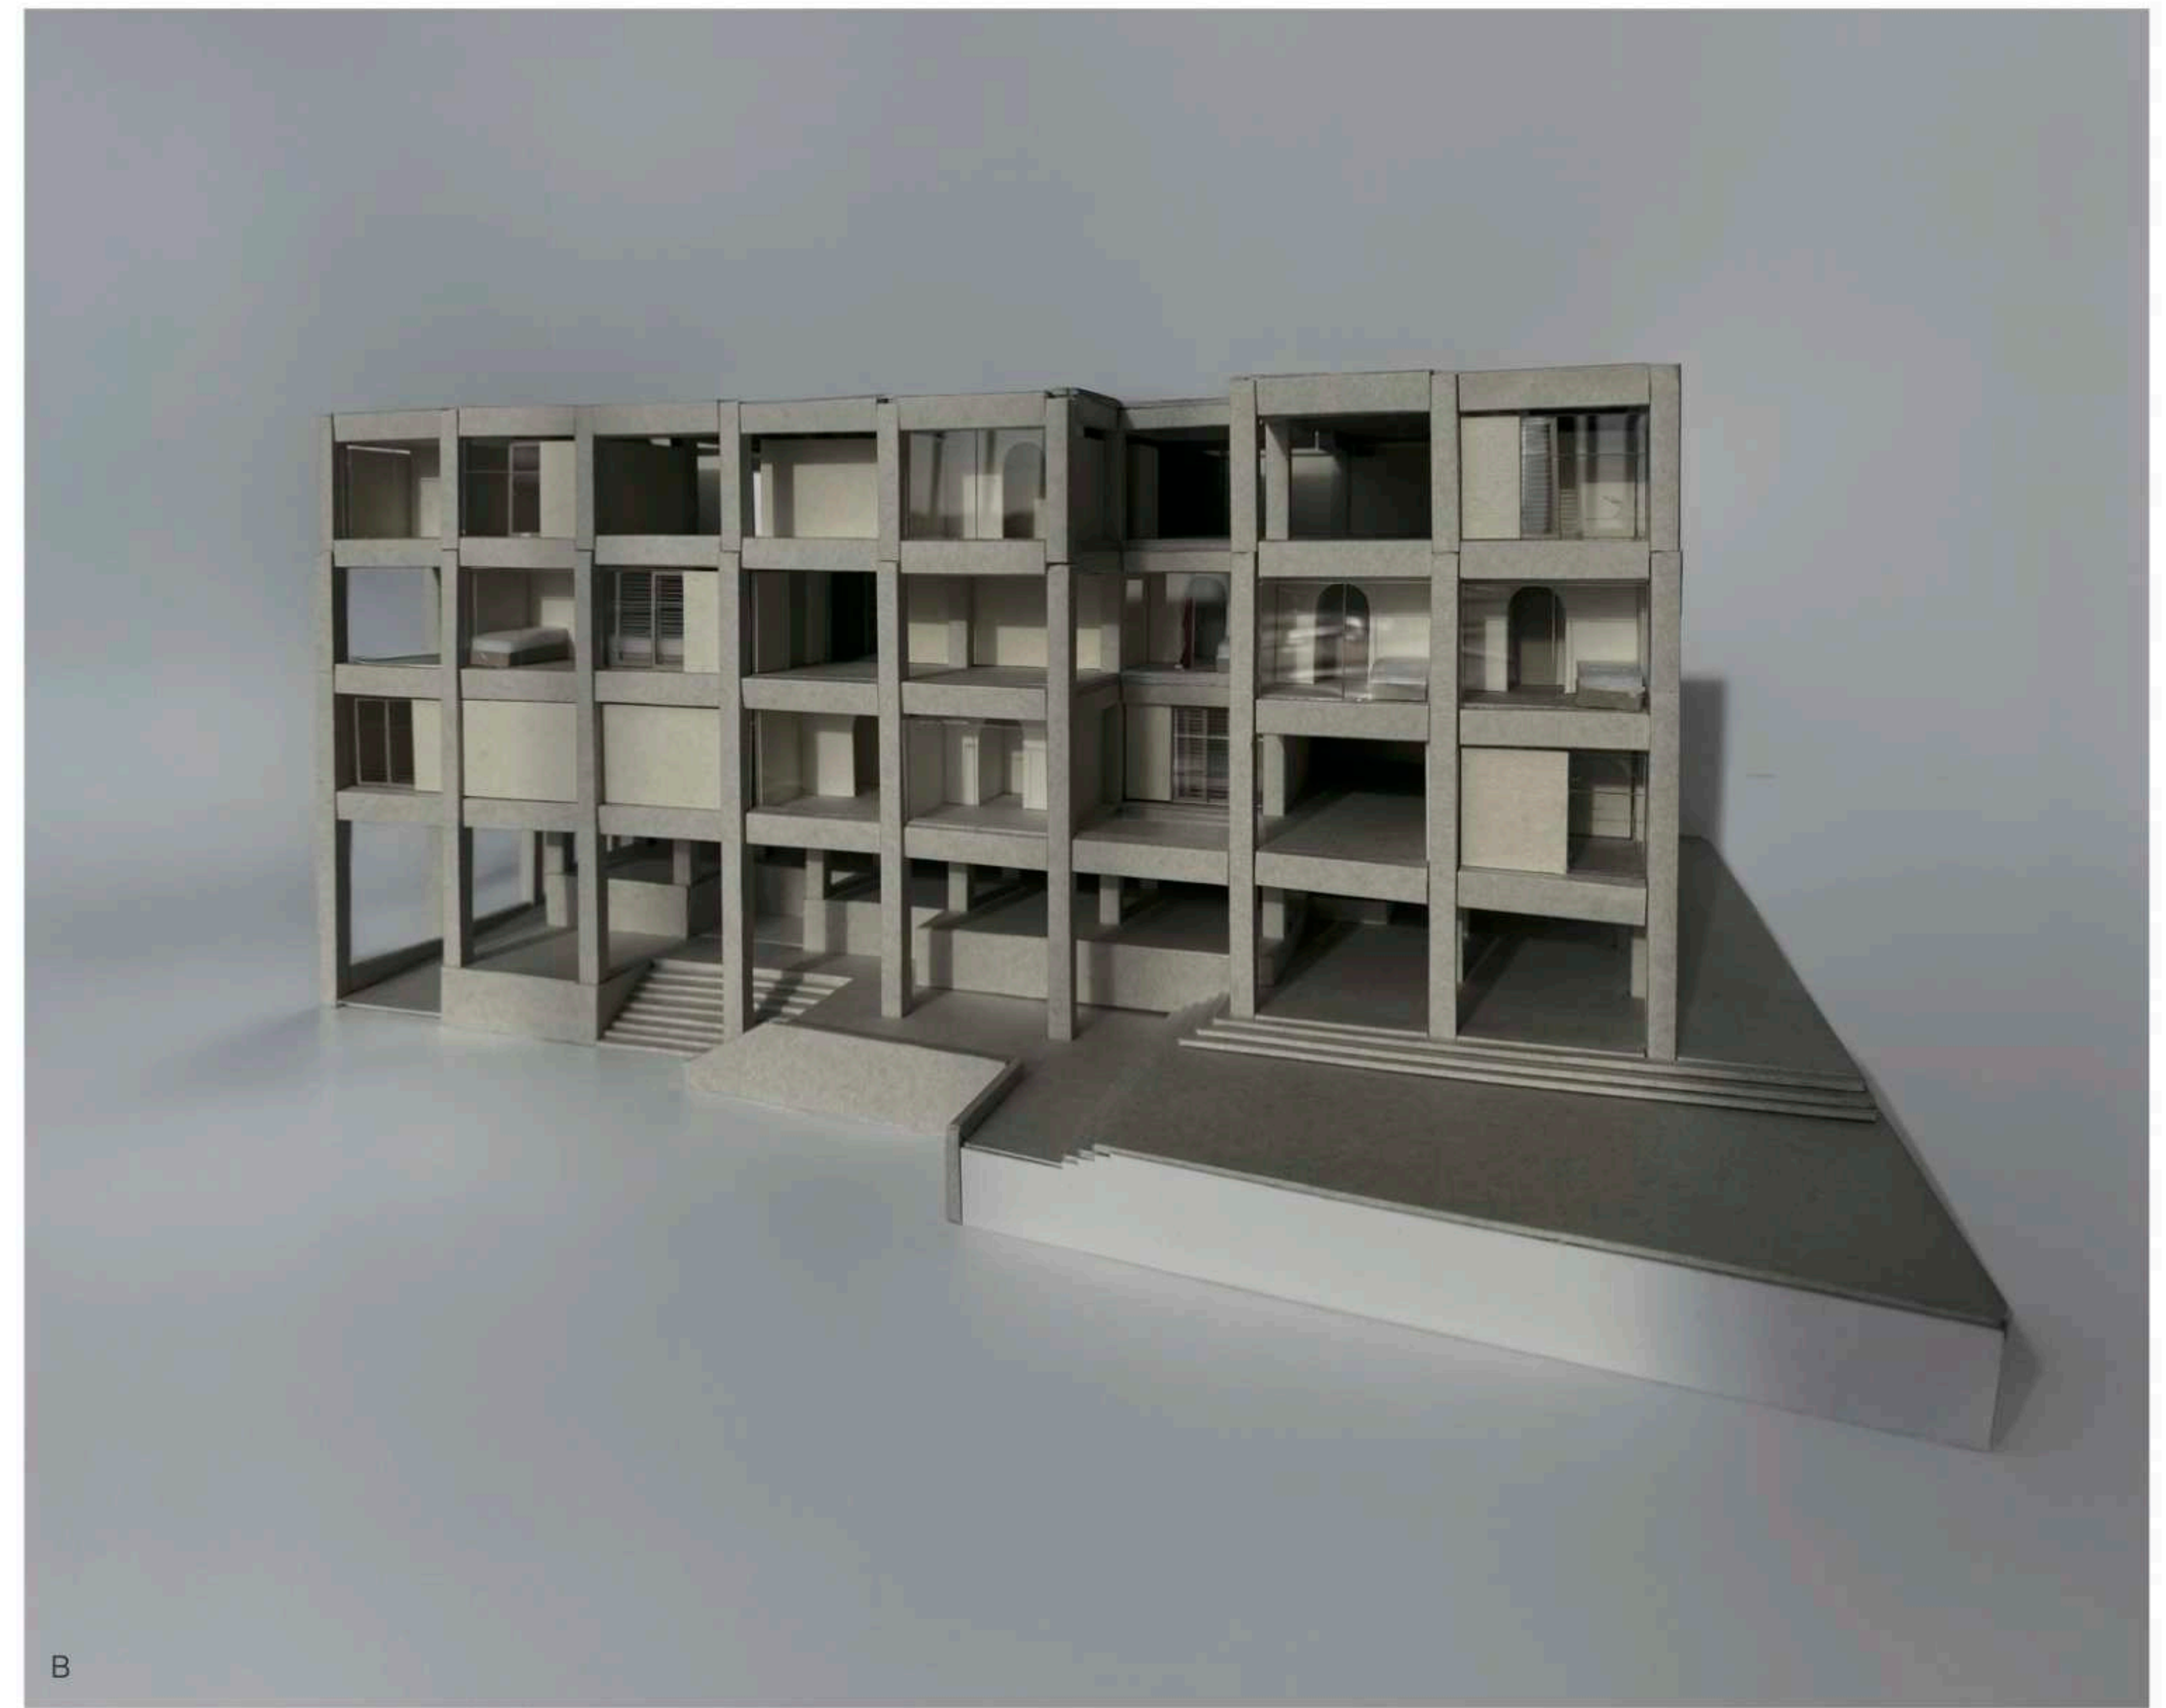

B



C

A. The previous idea of "Boundary Manners"
 B, C. The previous idea of "Lattice Dwelling"